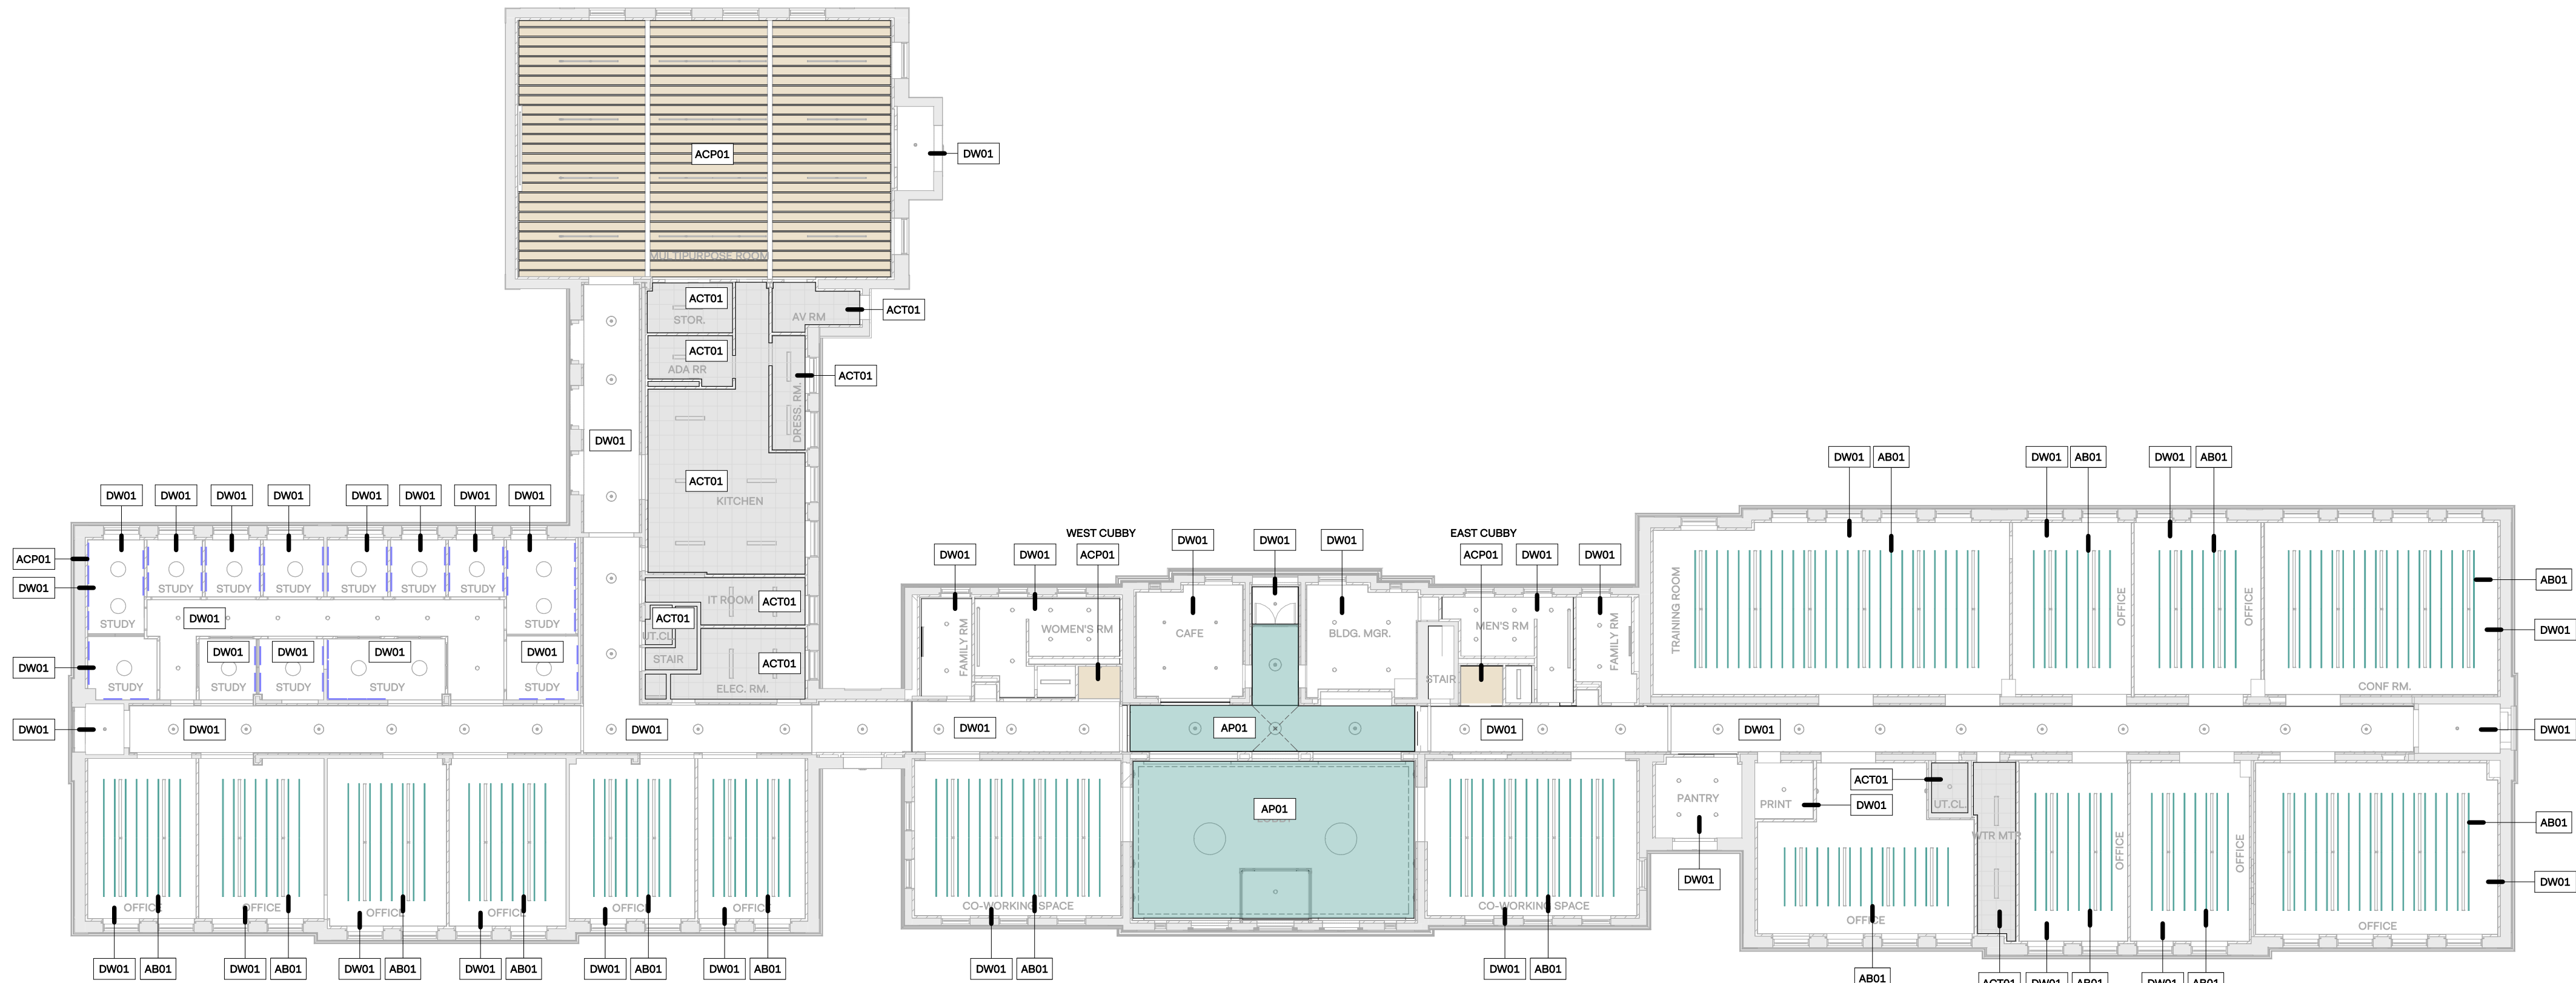


7/13/2025 6:13:22 PM



1 Interior Design - First Floor - Finish Ceiling Plan
1/16" = 1'-0"

 
 
 
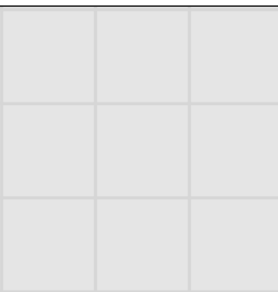
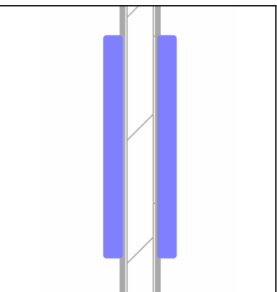
FINISH MATERIAL AND PRODUCT SUMMARY						
TAG	TYPE	MANUFACTURER	MODEL	FINISH	THICKNESS	NOTES
LN01	Linoleum Flooring	Duracryl	Corques Liquid Lino	Beige B312-S	2-2.5mm	
LN02	Linoleum Flooring	Duracryl	Corques Liquid Lino	Sage Green BL318-H	2-2.5mm	
LN03	Linoleum Flooring	Duracryl	Corques Liquid Lino	Salmon W302-M	2-2.5mm	
TR01	Terrazzo Flooring	Duracryl	Durabella Seamless Terrazzo	Beige Base, TBD glass & shell aggregate	TBD	WATERPROOF MEMBRANE AS REQUIRED
TR02	Restored Terrazzo Flooring	-	-	Restoration Match	TBD	
CR01	Concrete Flooring	-	-	Polished Concrete, Trowel Finish	TBD	REFER TO ARCHITECTURAL DRAWINGS
TL02	Tile Flooring	Nemo Tile	Rocco 24x24" Medium	Beige, Matte	9mm	
TL01	Wall Tile	Yi Design	YTile 158x158mm	Jade Green	10mm	
DW01	Drywall	USG	142220	White	5/8in	
CB01	Cement Board	Durock	5/8" Cement Board 170576	-	5/8in	
AP01	Acoustic Plaster	Pyrok	StarSilent System	White	TBD	
ACP01	Acoustic Panel	Filzfelt	Akustika 25 Ceiling & Wall Panel	110 Rohweiß	1 7/8in	
AB01	Acoustic Baffle	Filzfelt	Akustika 25 Baffle, Suspension Cable	110 Rohweiß, covered edge	1.25in	
ACT01	Acoustic Ceiling Tile	Rockfon	Rockfon Alaska	White, CDX Fully Concealed	7/8in	
SP01	Millwork Panel	Equitone	Natura	N661	12mm	
PL02	Lime Plaster Wainscot	BioLime	Cement Board Plaster	Match Benjamin Moore Mystical Blue 792	5/8in	
PL04	Lime Plaster Wainscot	BioLime	Cement Board Plaster	Match Benjamin Moore Nautilus Shell 064	5/8in	
PL05	Lime Plaster Wainscot	BioLime	Cement Board Plaster	Match Benjamin Moore Linen White 912	5/8in	
PL06	Lime Plaster Wainscot	BioLime	Cement Board Plaster	Match Benjamin Moore Feather Green 625	5/8in	
PT01	Paint	Benjamin Moore	-	Sweat Pear 389	-	
PT02	Paint	Benjamin Moore	-	Spring Break 627	-	
PT03	Paint	Benjamin Moore	-	Harbor Haze 2136-60	-	
PT04	Paint	Benjamin Moore	-	Myrtle Beach 061	-	
PT05	Paint	Benjamin Moore	-	Linen White OC-146	-	
PT06	Paint	Benjamin Moore	-	Chesapeake CW-595	-	
PT07	Intumescent Paint	-	-	Match PT06 Chesapeake CW-595	-	REFER TO ARCHITECTURAL DRAWINGS
WB01	Wall Base	Roppe	Pinnacle 2 1/2" Cove Rubber Wall Base	161 Snow	1/8in	

FINISH SCHEDULE						
ROOM TYPE	FLOOR	WALL (UPPER)	WALL (LOWER)	BASE	CEILING	NOTES
NORTH VESTIBULE	LN01	DW01	PL05	-	DW01	See ID-201 for interior elevations
EAST VESTIBULE	TR02	DW01	PL05	-	DW01	See ID-207 for interior elevations
WEST VESTIBULE	TR02	DW01	PL05	-	DW01	See ID-207 for interior elevations
MULTIPURPOSE VESTIBULE	TR02	DW01	PL02	-	DW01	See ID-202 for interior elevations
LOBBY	TR01	DW01	PL05	-	AP01	See ID-201 for interior elevations
LOBBY CORRIDOR	LN01	DW01	PL05	-	AP01	See ID-201 for interior elevations
EAST CORRIDOR	LN01	DW01	PL05	-	DW01	See ID-207 for interior elevations
WEST CORRIDOR	LN01	DW01	PL05	-	DW01	See ID-207 for interior elevations
NORTH CORRIDOR	LN01	DW01	PL05	-	DW01	See ID-207 for interior elevations
STUDY CORRIDOR	LN01	DW01	PL04	-	DW01	See ID-203 for interior elevations
CAFE	LN01	DW01	PL05	-	DW01	-
BLDG. MGR.	LN01	DW01	DW01	-	DW01	-
CO-WORKING	LN03	DW01	PL04	-	DW01 & AB01	See ID-203 for interior elevations
OFFICE	LN02	DW01	PL06	-	DW01 & AB01	See ID-204 for interior elevations
STUDY (SMALL OFFICE)	LN03	DW01	PL04	-	DW01	See ID-203 for interior elevations
TRAINING ROOM	LN01	DW01	PL05	-	DW01 & AB01	-
MULTIPURPOSE	LN01	DW01	PL02	-	ACP01	See ID-202 for interior elevations
WOMEN'S RM	TL02	DW01	TL01	-	DW01	See ID-205 for interior elevations
MEN'S RM	TL02	DW01	TL01	-	DW01	See ID-205 for interior elevations
FAMILY RM (ADA)	TL02	DW01	TL01	-	DW01	See ID-205 for interior elevations
WEST CUBBY	LN01	DW01	ACP01	-	ACP01	See ID-207 for interior elevations
EAST CUBBY	LN01	DW01	ACP01	-	ACP01	See ID-207 for interior elevations
PANTRY	LN01	DW01	PL05	-	DW01	See ID-206 for interior elevations
PRINT ROOM	LN01	DW01	PL05	-	DW01	-
BACK OF HOUSE	CR01	DW01	DW01	WB01	ACT01	BACK OF HOUSE SPACES INCLUDE: UT. CLOSET, WTR ROOM, ELEC. ROOM, IT ROOM, KITCHEN, DRESS ROOM, ADA RR, STORAGE, AV ROOM

NOTES

MATERIAL SAMPLE SUBMITTALS ARE REQUIRED FOR ALL SPECIFIED FINISH MATERIALS AND PAINT COLORS PRIOR TO PURCHASE.

LEGENDS

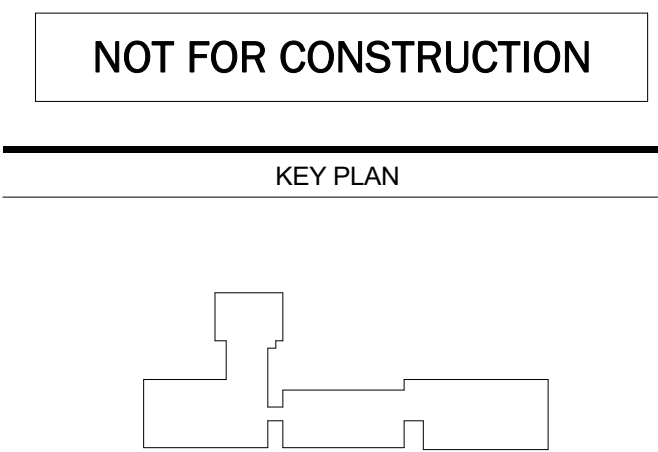
CEILING FINISHES	ACOUSTICAL DEVICES
	
DW01 DRYWALL	AB01 ACOUSTICAL BAFFLE
	
AP01 ACOUSTICAL PLASTER	ACP01 ACOUSTICAL PANEL
	
ACT01 ACT CEILING	ACP01 ACOUSTICAL PANEL

CLIENT

BUTTERMILK LABS LLC
610 WEST 26TH ST. SUITE 910
NEW YORK, NY 10001

CONSULTANTS

MEP/FP ENGINEER:
DERIVE ENGINEERS
665 BROADWAY, SUITE 701
NEW YORK, NY 10012
STRUCTURAL ENGINEER:
SILMAN
32 OLD SLIP, 10TH FLOOR
NEW YORK, NY 10005
INTERIOR DESIGN/ LIGHTING/SUSTAINABILITY CONSULTANT:
CO-ADAPTIVE ARCHITECTURE PLLC
63 FLUSHING AVE BUILDING 303, SUITE 603
BROOKLYN, NY 11205
ACOUSTICS/AV/IT/SECURITY:
CERAMI
1001 AVENUE OF THE AMERICAS, 4TH FLOOR
NEW YORK, NY 10018
CODE/FILING REPRESENTATIVE:
VITACCO
299 BROADWAY, SUITE # 5,
NEW YORK, NY 10007
GEOTECHNICAL, SURVEY:
LANGAN
360 WEST 31ST STREET, 8TH FLOOR
NEW YORK, NY 10001-2727
HISTORIC PRESERVATION TAX CREDITS:
GREGORY DIETRICH HPC
615 WEST 113TH STREET, #3
NEW YORK, NY 10025
LANDSCAPE DESIGN:
ELIZABETH KENNEDY LANDSCAPE ARCHITECT, PLLC
BROOKLYN NAVY YARD BUILDING 275, ROOM 202
63 FLUSHING AVENUE
BROOKLYN, NY 11205
ARCHAEOLOGY:
LINDA STONE ARCHAEOLOGICAL CONSULTING
248 EAST 48 STREET, #12B
NEW YORK, NY 10017



100% CD	11.04.2024
50% CD	10.04.2024
HPTC-PART 2 SUBMISSION	08.09.2024
REVISED 100% CD	07.12.2024
NO. DESCRIPTION	DATE

PROJECT:
BUILDING 301 GOVERNORS ISLAND
301 COMFORT ROAD, GOVERNORS ISLAND,
NEW YORK, NY 11231

REFLECTED CEILING PLAN - FINISHES AND ACOUSTICAL

DOB APPROVAL STAMP:

SEAL & SIGNATURE:	DATE: 1/13/25
	PROJECT NO: G301
	SCALE: AS NOTED
	DRAWN BY: Author
	CHECKED BY: Checker
	SHEET NUMBER: ID-110
	DWG. COUNT: 2 OF 13