



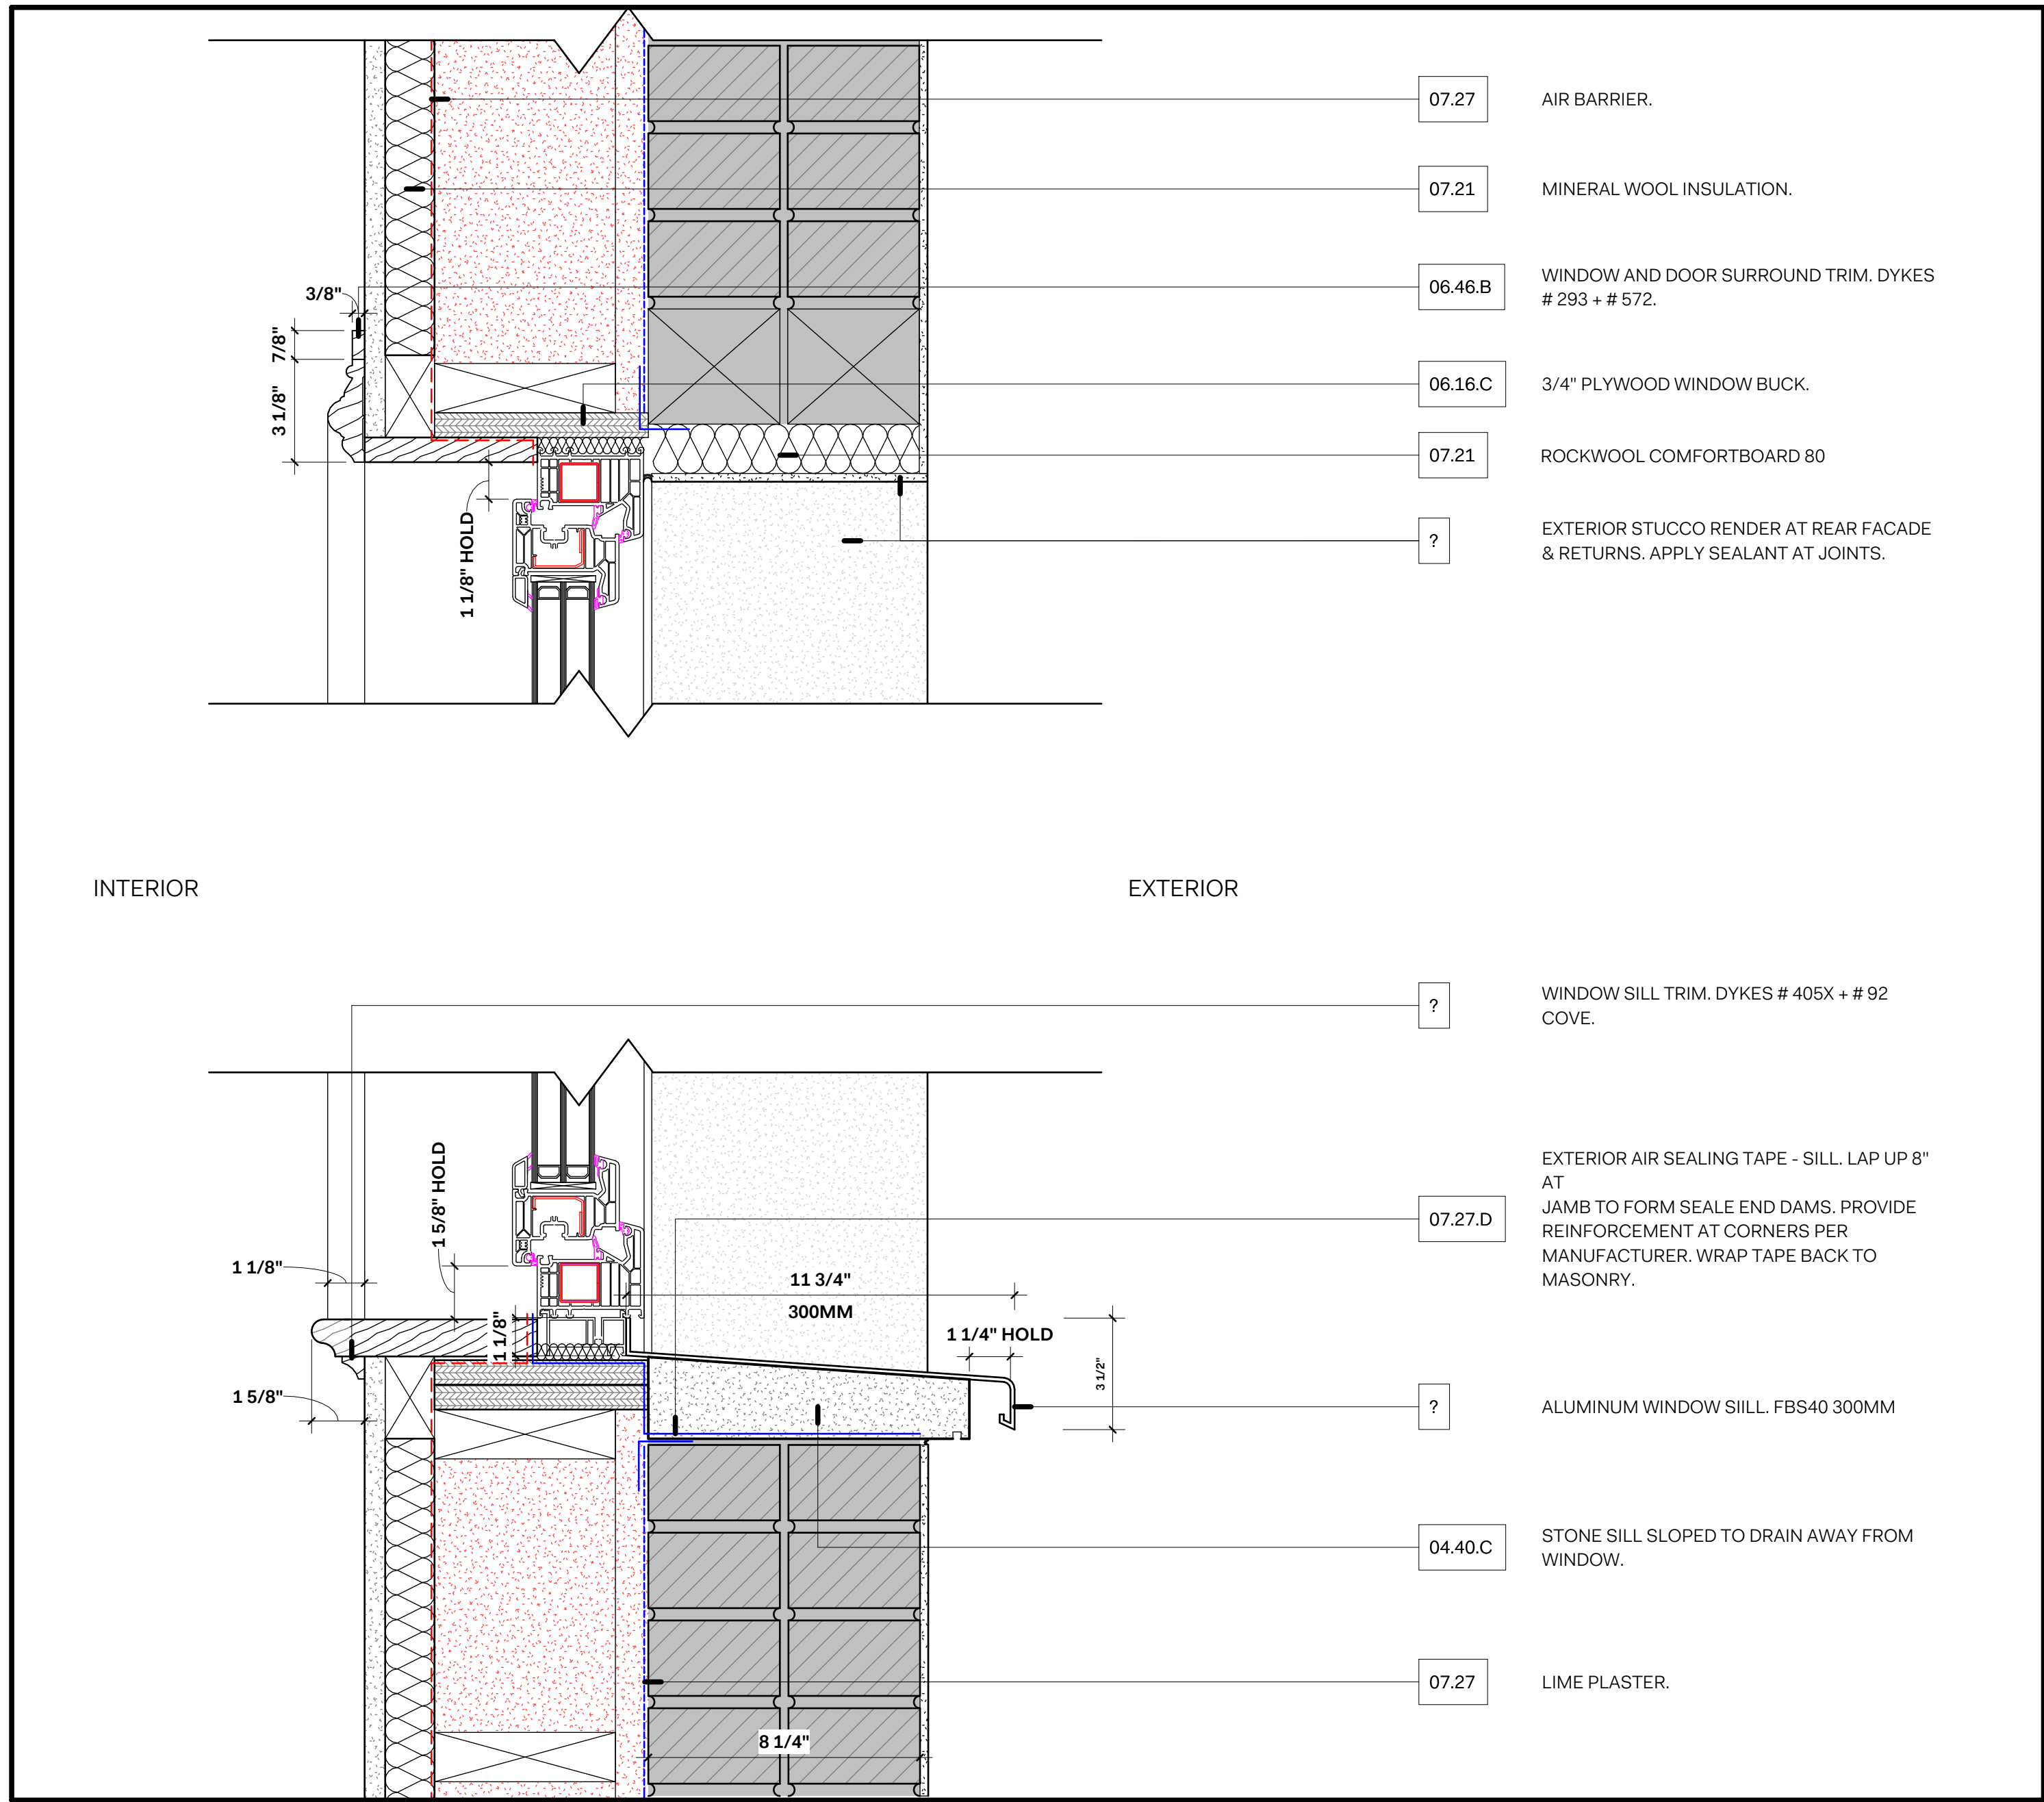

1 TYPICAL WINDOW - REAR FACADE - HEAD/SILL
3" = 1'-0"

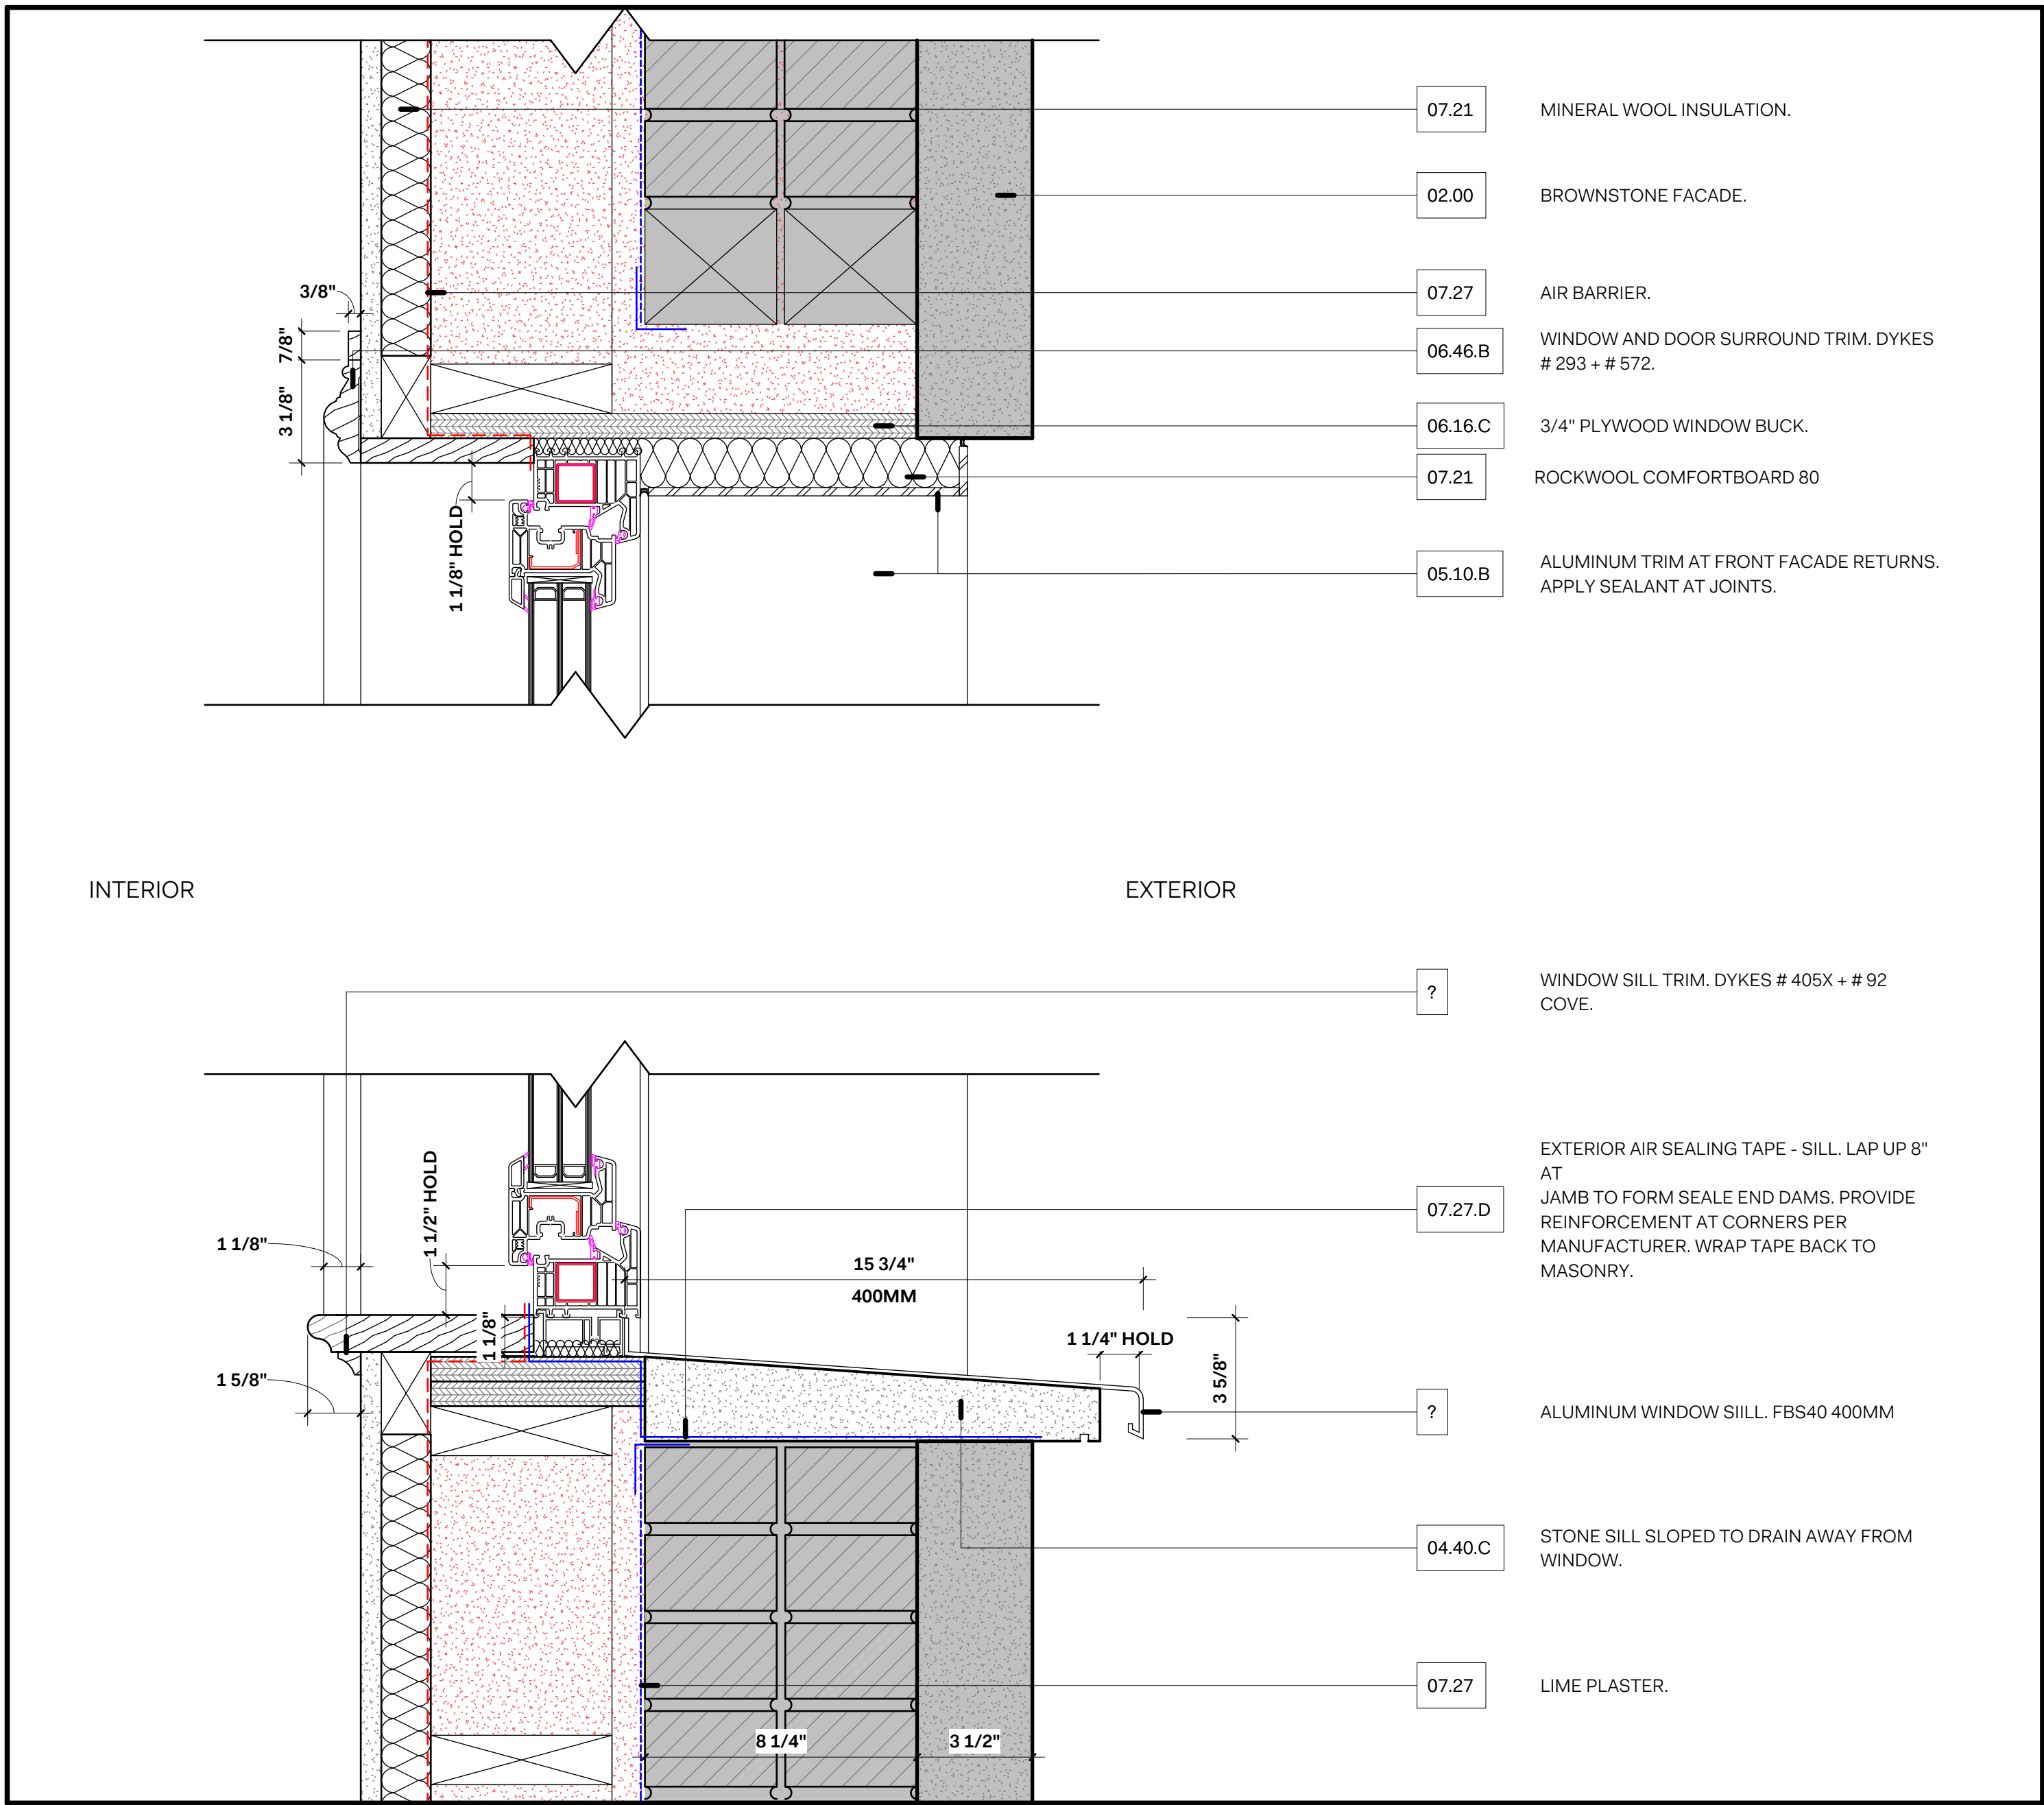

2 TYPICAL WINDOW - FRONT FACADE - HEAD/SILL
3" = 1'-0"

CO Adaptive

Architect
CO Adaptive Architecture PLLC
Building 303, Suite 603
63 Flushing Avenue
Brooklyn, NY 11235
t. 347.586.0455
hello@coadaptive.co

Mechanical/Electrical/Plumbing Engineer
ABS Engineering, PLLC
27 West 57th Street, 8th Floor
New York, NY 10018
t. 212.217.2361
info@absengineer.com

Structural Engineer
Nathaniel Bergan, P.E.
225 W. 34th Street, #922
New York, NY 10012
t. 860.586.0025
nathaniel.bergan@gmail.com

Rev. #	Date	Revision Description
4	08/27/2024	General Update

Owner & Project Information

Q142
142 QUINCY STREET, BROOKLYN, NY 11216
Ariel Azoff • Gabe Stein, Elizabeth Zehn • Will Cudney

DOB NOW #
B08048986

Drawing Title
**EXTERIOR DETAILS -
WINDOWS - HEAD/SILL
DETAILS**



Project Number

Q142

Issue Date

11-25-2024

Sheet Number

45 / 61

Drawing Number

A-525.00

Copyright 2021 CO Adaptive Architecture PLLC All rights reserved