



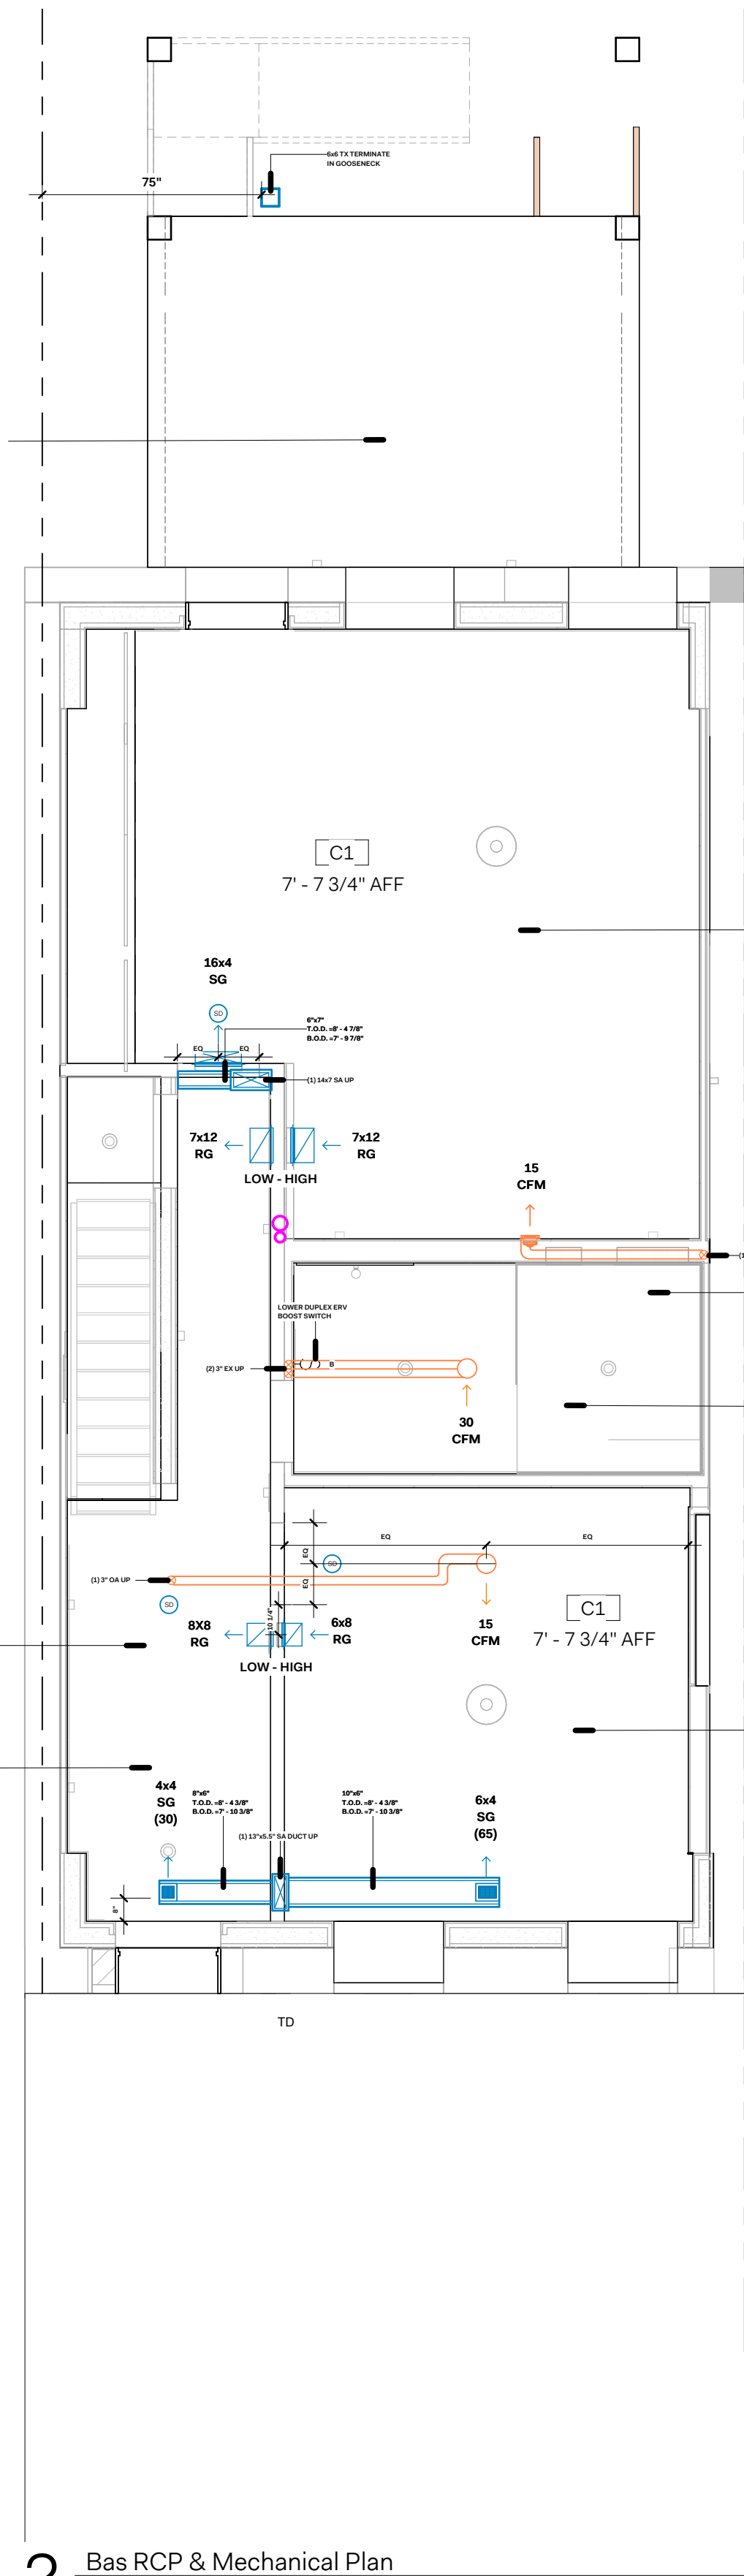

2 Bas RCP & Mechanical Plan
1/4" = 1'-0"

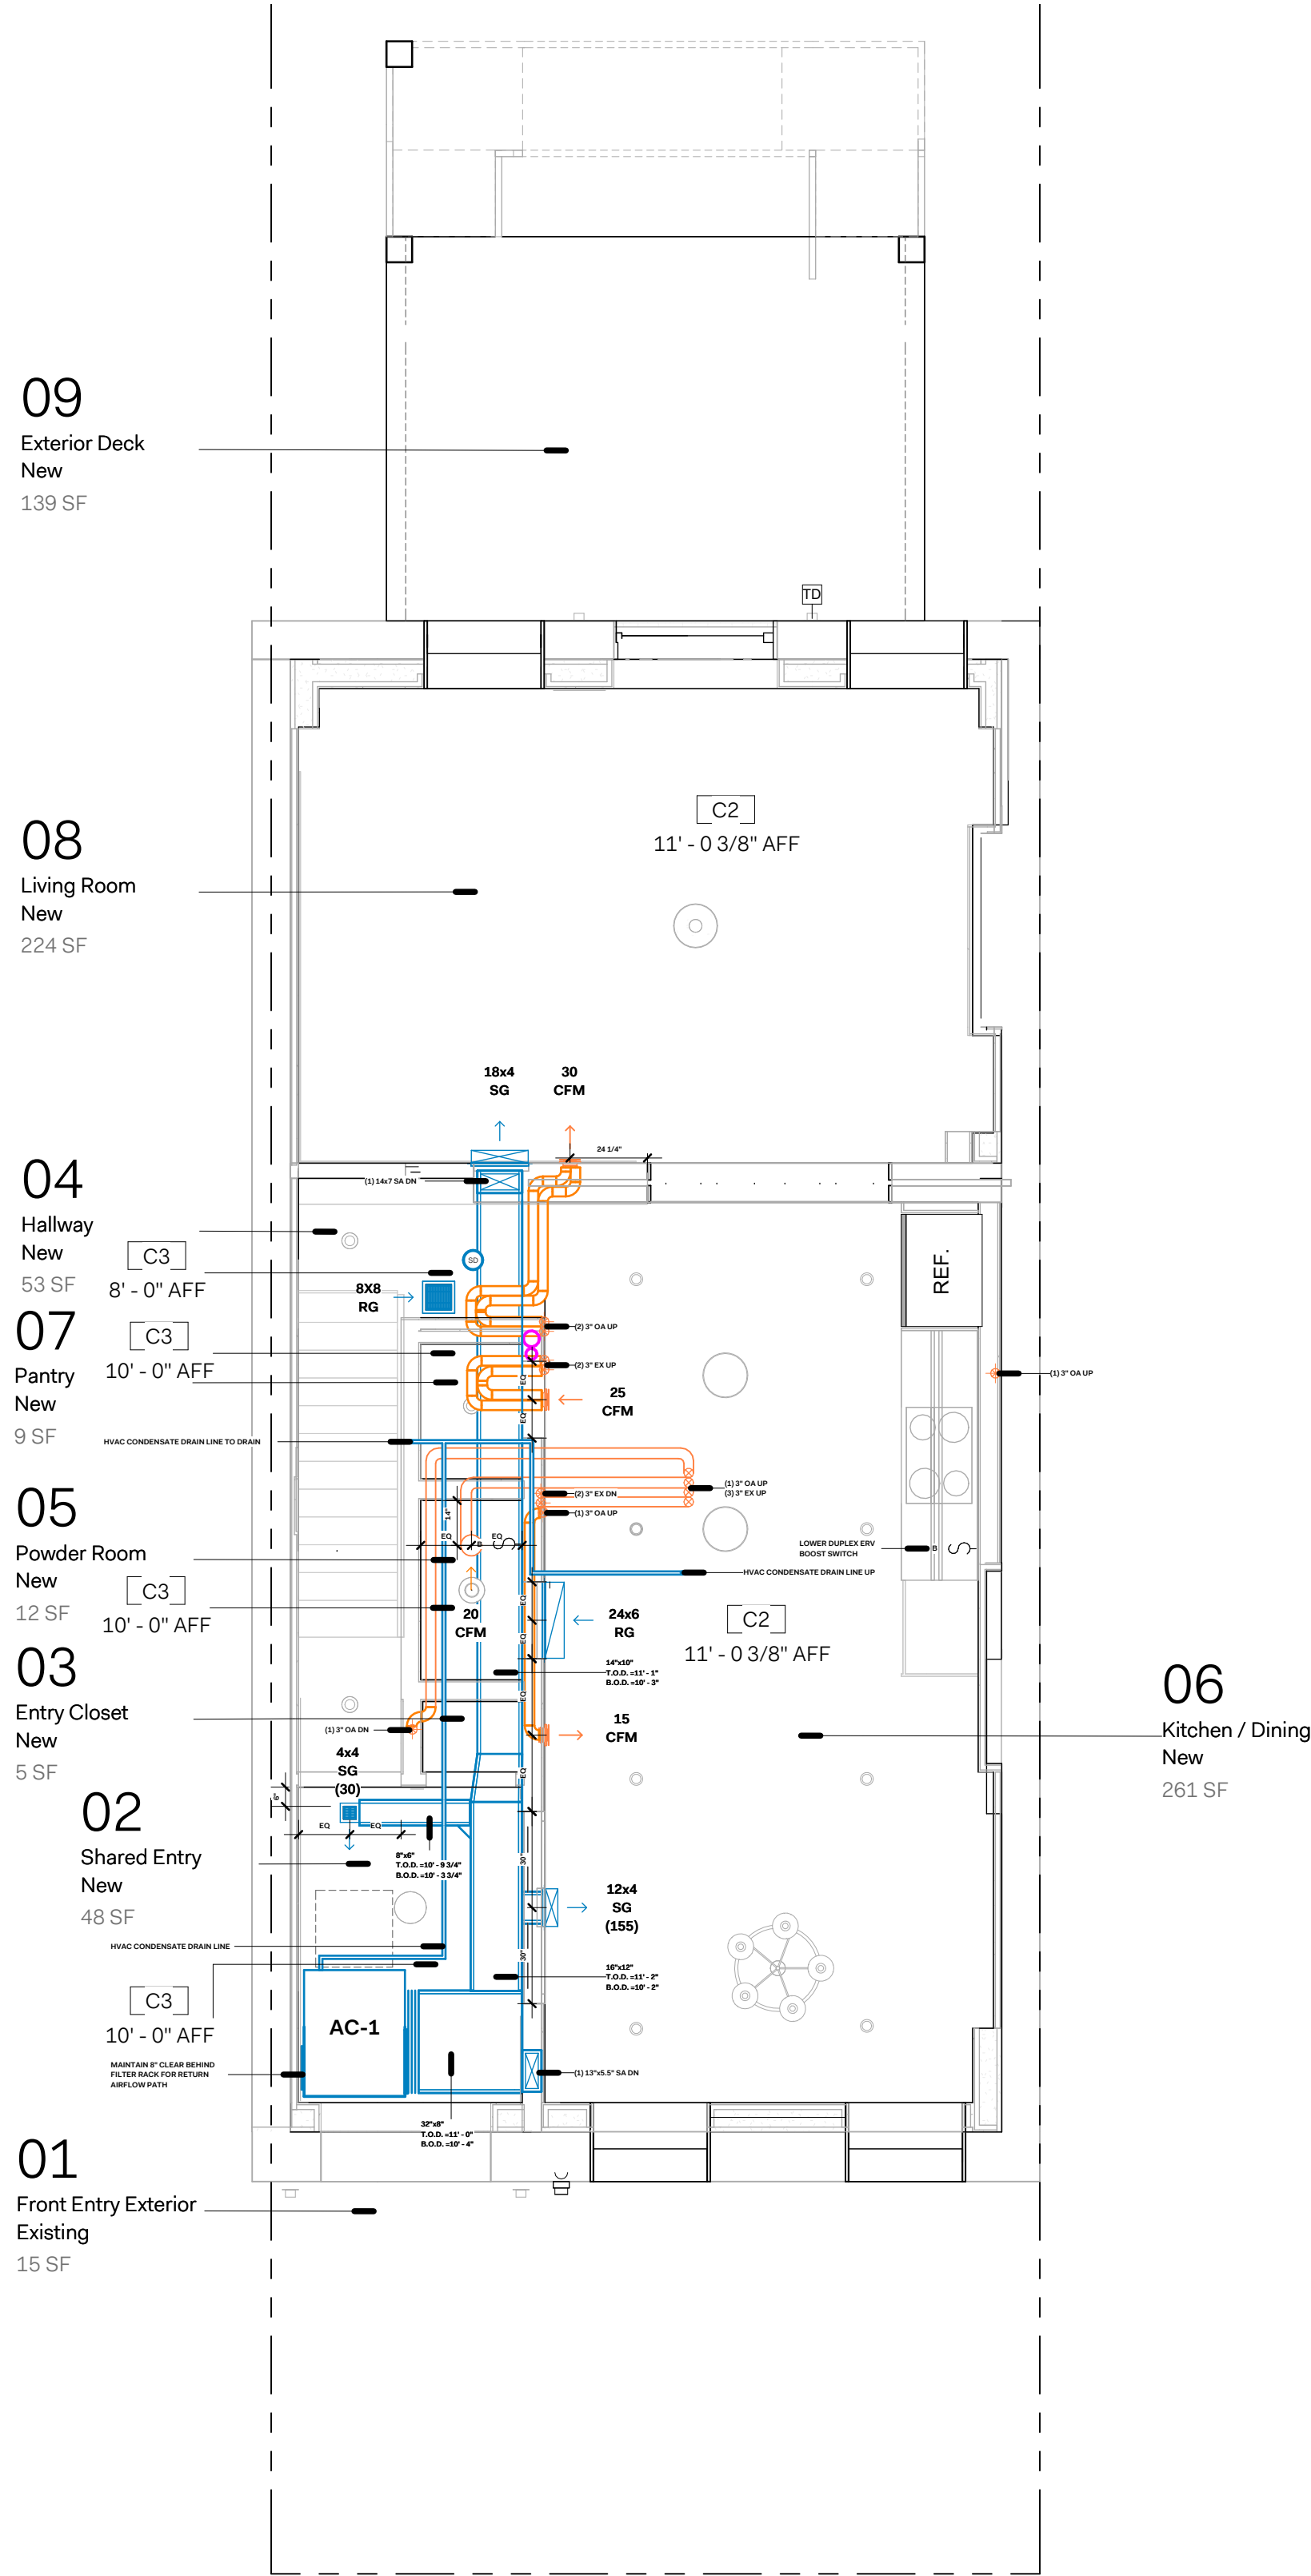

1 001 RCP & Mechanical Plan
1/4" = 1'-0"

MECHANICAL LEGEND

- HVAC RETURN/SUPPLY AIR GRILLE
- HVAC SUPPLY SHAFT
- HVAC RETURN SHAFT
- HVAC DUCTS (SIZE NOTED INDICATES OVERALL DIMENSION INCLUDING 1" INTERNAL INSULATION LINING)
- ZEHNDER ERV RETURN/SUPPLY AIR OUTLETS
- ZEHNDER ERV RETURN/SUPPLY AIR DUCTS

NOTES:

- ALL DUCT DIMENSIONS AND ELEVATIONS ARE OVERALL DIMENSION INCLUDING 1" INTERNAL INSULATION LINING
- ALL SQUARE MITERED ELBOWS (90 DEGREE) TO BE PROVIDED WITH DOUBLE THICKNESS TURNING VANES
- ALL SUPPLY OUTLETS TO BE PROVIDED WITH VOLUME DAMPERS. ALL DAMPERS TO BE CABLE OPERATED WITH CLIP ON THE FACE OF THE DIFFUSER FOR ADJUSTING
- ALL DUCT TAPS TO HAVE FLARED CONNECTIONS TYP.
- ALL SUPPORT DUCTWORK SHALL BE IN ACCORDANCE WITH SMACNA GUIDELINES
- ALL SHEET METAL GAUGES SHALL BE IN ACCORDANCE WITH SMACNA GUIDELINES

CO Adaptive

Architect
CO Adaptive Architecture PLLC
Building 303, Suite 603
63 Flushing Avenue
Brooklyn, NY 11235
t. 347.586.0455
hello@coadaptive.co

Mechanical Electrical Plumbing Engineer
ABS Engineering, PLLC
27 West 57th Street, 8th Floor
New York, NY 10018
t. 212.317.2361
info@absengineer.com

Structural Engineer
Nathaniel Bergan, P.E.
225 W. 34th Street, #922
New York, NY 10012
t. 860.598.0025
nathaniel.bergan@gmail.com

Rev. #	Date	Revision Description
4	08/27/2024	General Update

Owner & Project Information

Q142
142 QUINCY STREET, BROOKLYN, NY 11216
Ariel Azoff • Gabe Stein, Elizabeth Zehn • Will Cudney

DOB NOW

808048986

Drawing Title

RCP & MECHANICAL PLAN
BAS & 001
Drawing Scale: 1/4" = 1'-0"
100% @ A1 (24" x 36")

Project Number

Q142

Issue Date

03-04-2025

Sheet Number

18 / 61

Drawing Number

A-115.00