



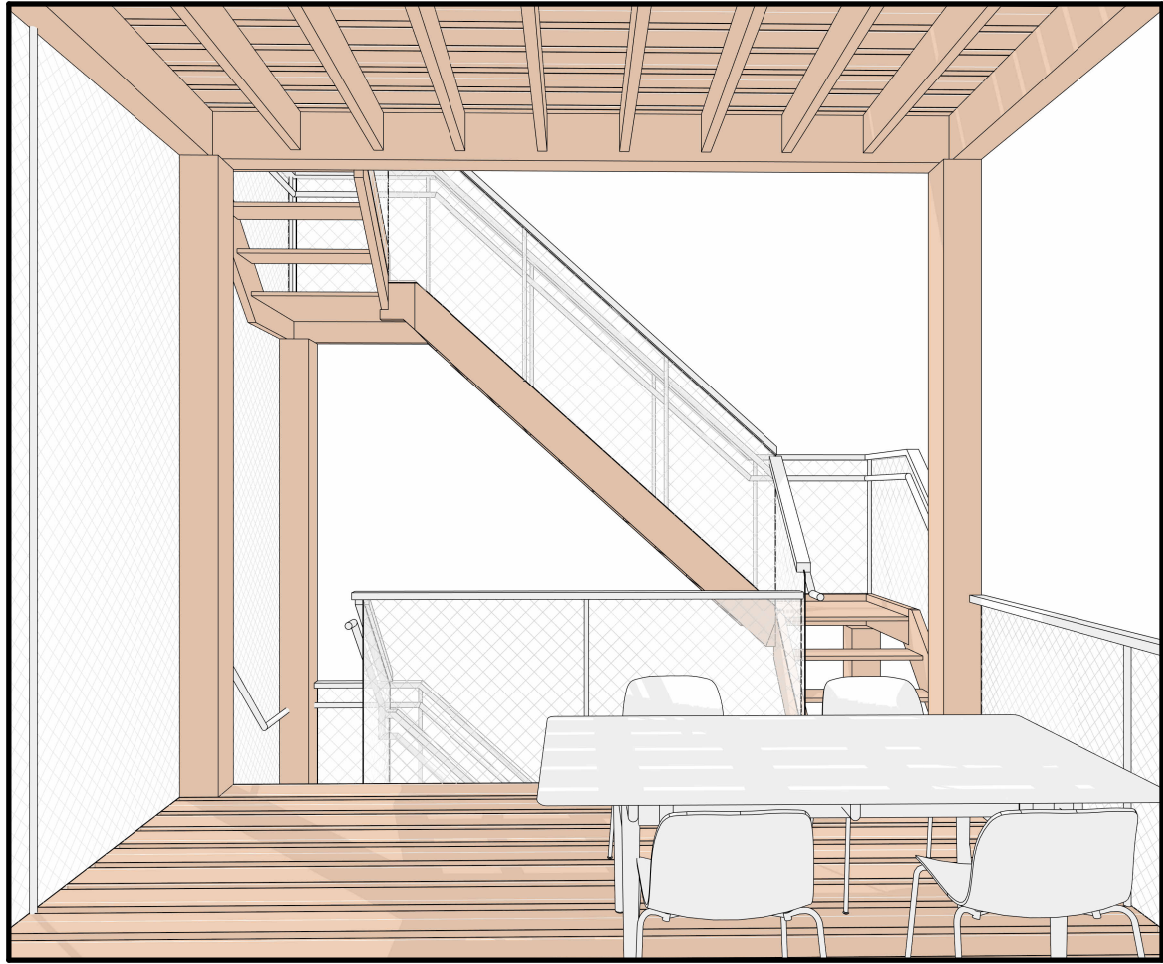


6 DECK OPTION 2 - PERSPECTIVE

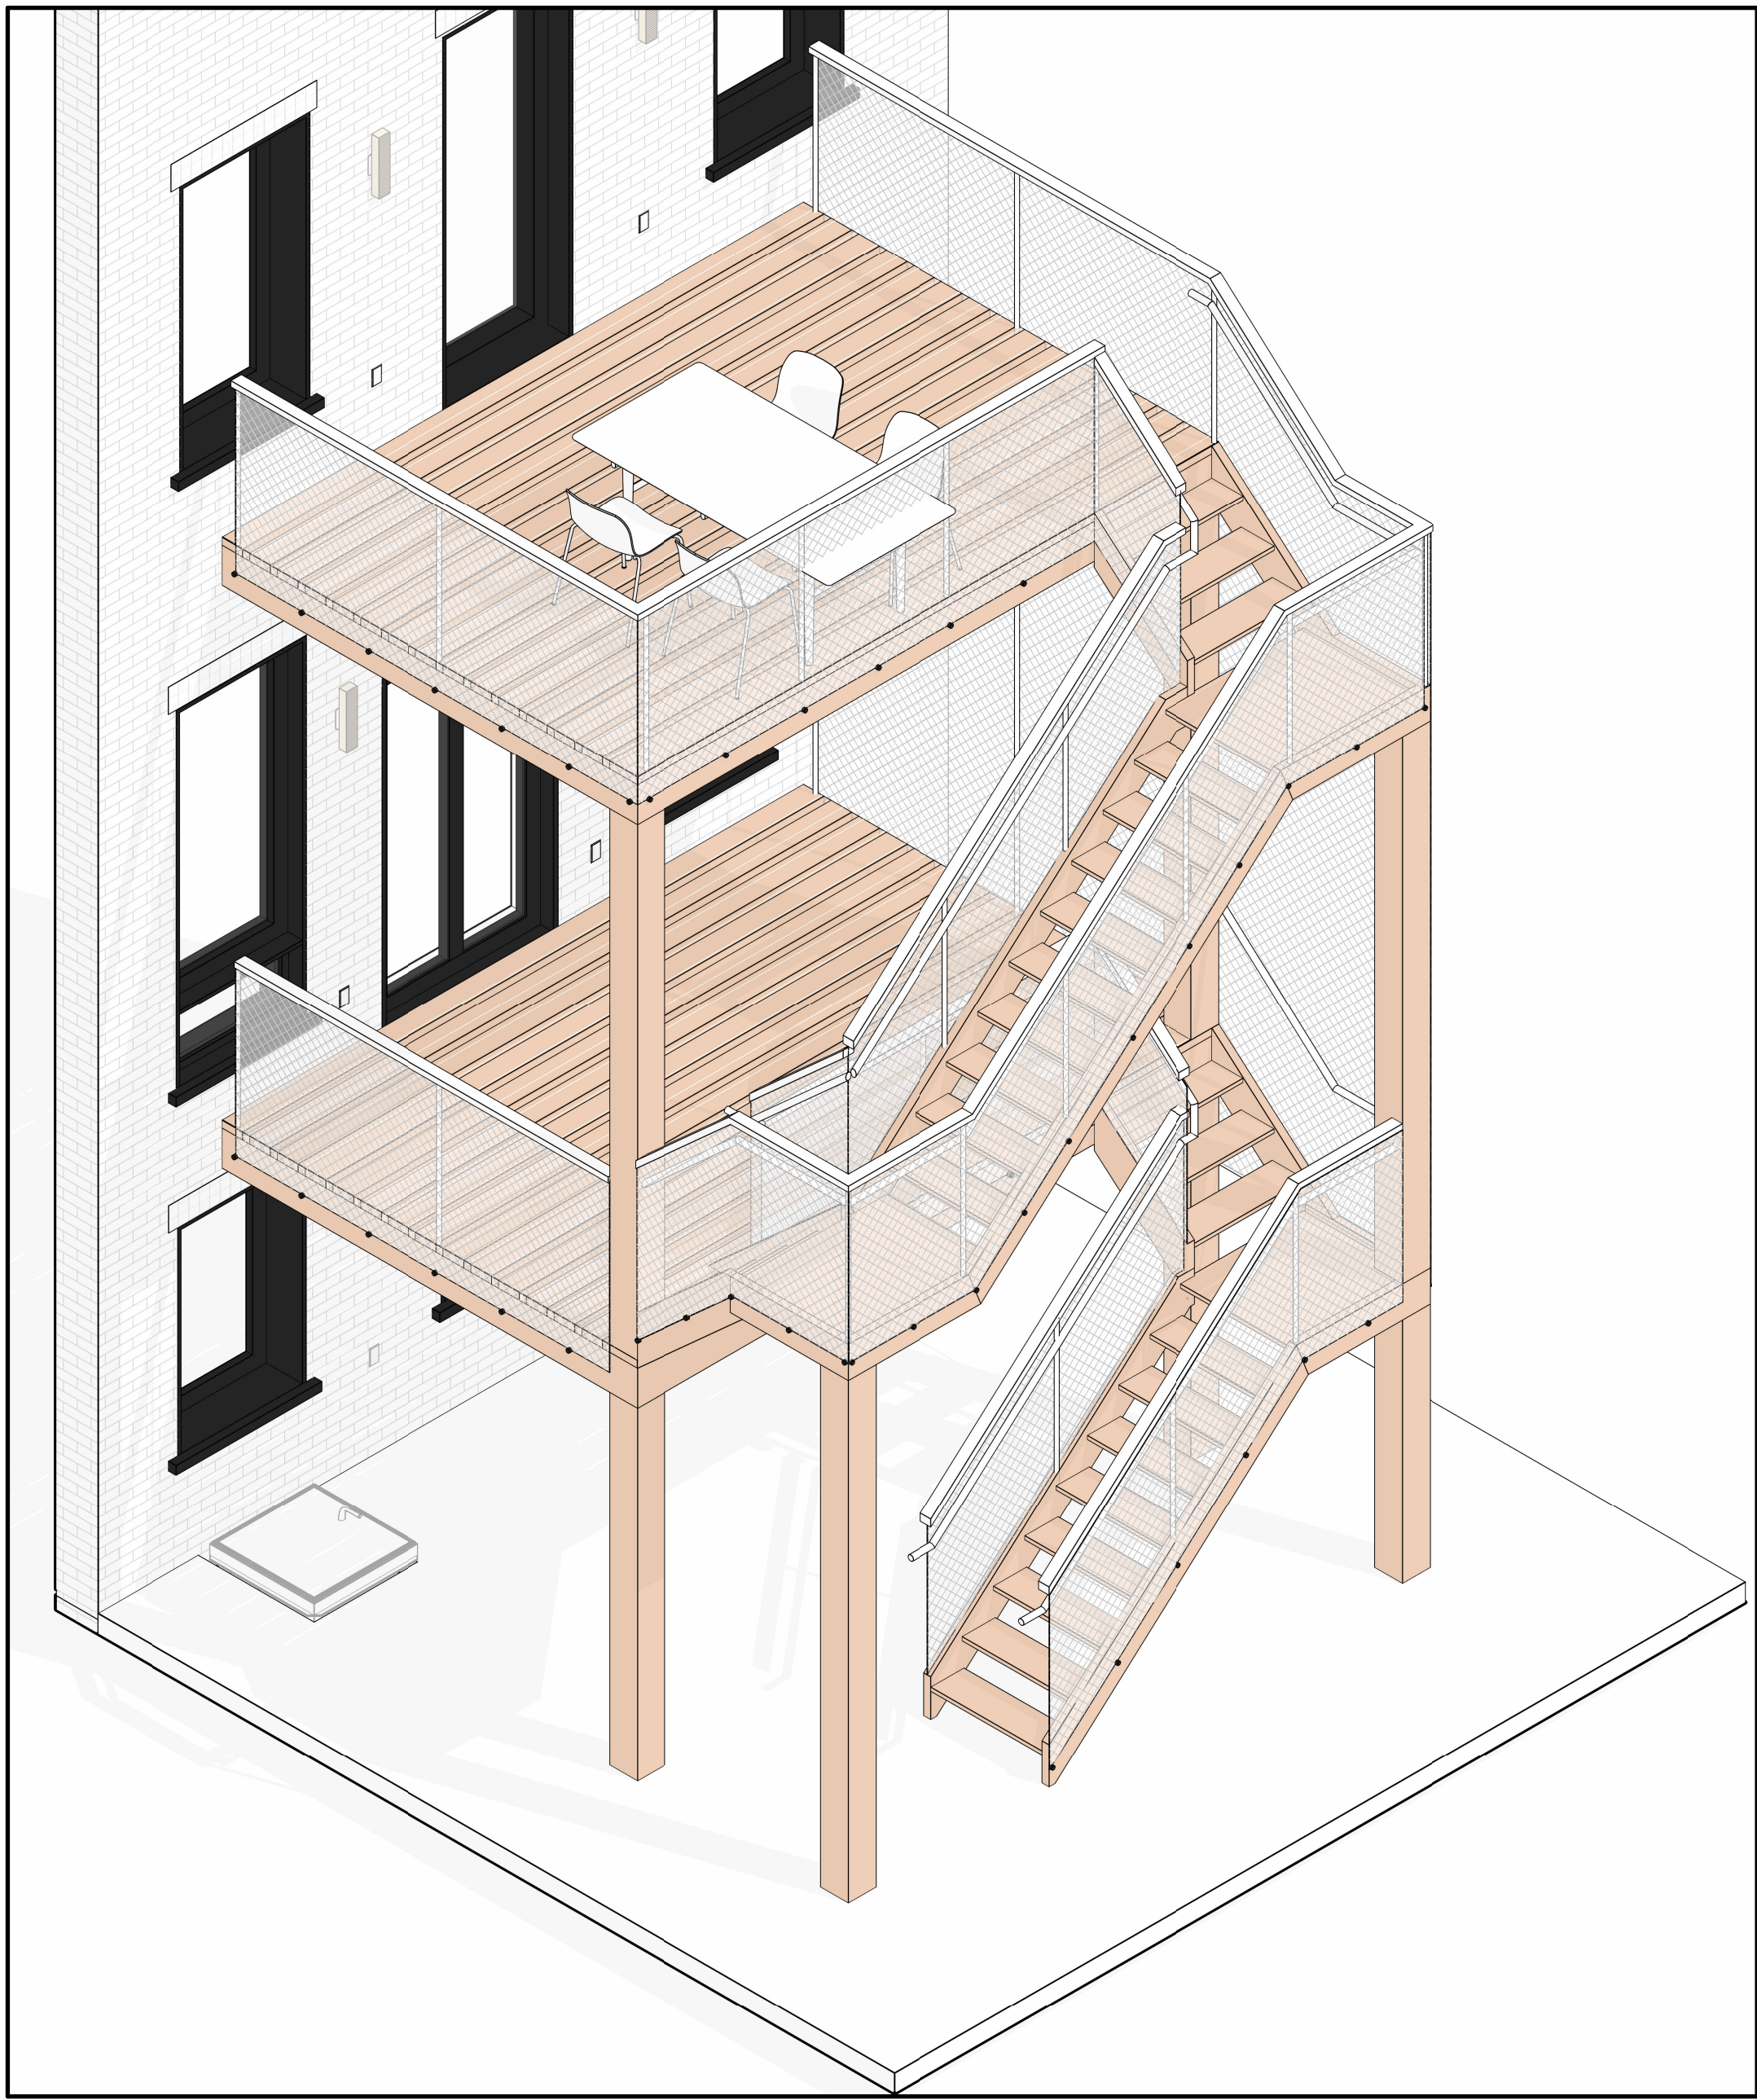


1 DECK OPTION 2 - AXON

STAIR CODE ANALYSIS & CALCULATIONS PER 1968 BUILDING CODE
TYPE: NEW CONSTRUCTION
CLEAR WIDTH: 36" MIN. WIDTH, APPLICABLE FOR INTERIOR STAIRS
SERVING LESS THAN FIFTY (50) OCCUPANTS, PER NYC BC §27-375.
HANDRAIL: 34"-38" AS PER NYC 2022 BC §1014.2


RISER & TREADS: PER NYC BC §27-375
MAXIMUM RISER HEIGHT: 8-1/4"
MINIMUM TREAD WIDTH: 9-1/2" + NOSING
NOSING: 1/2"

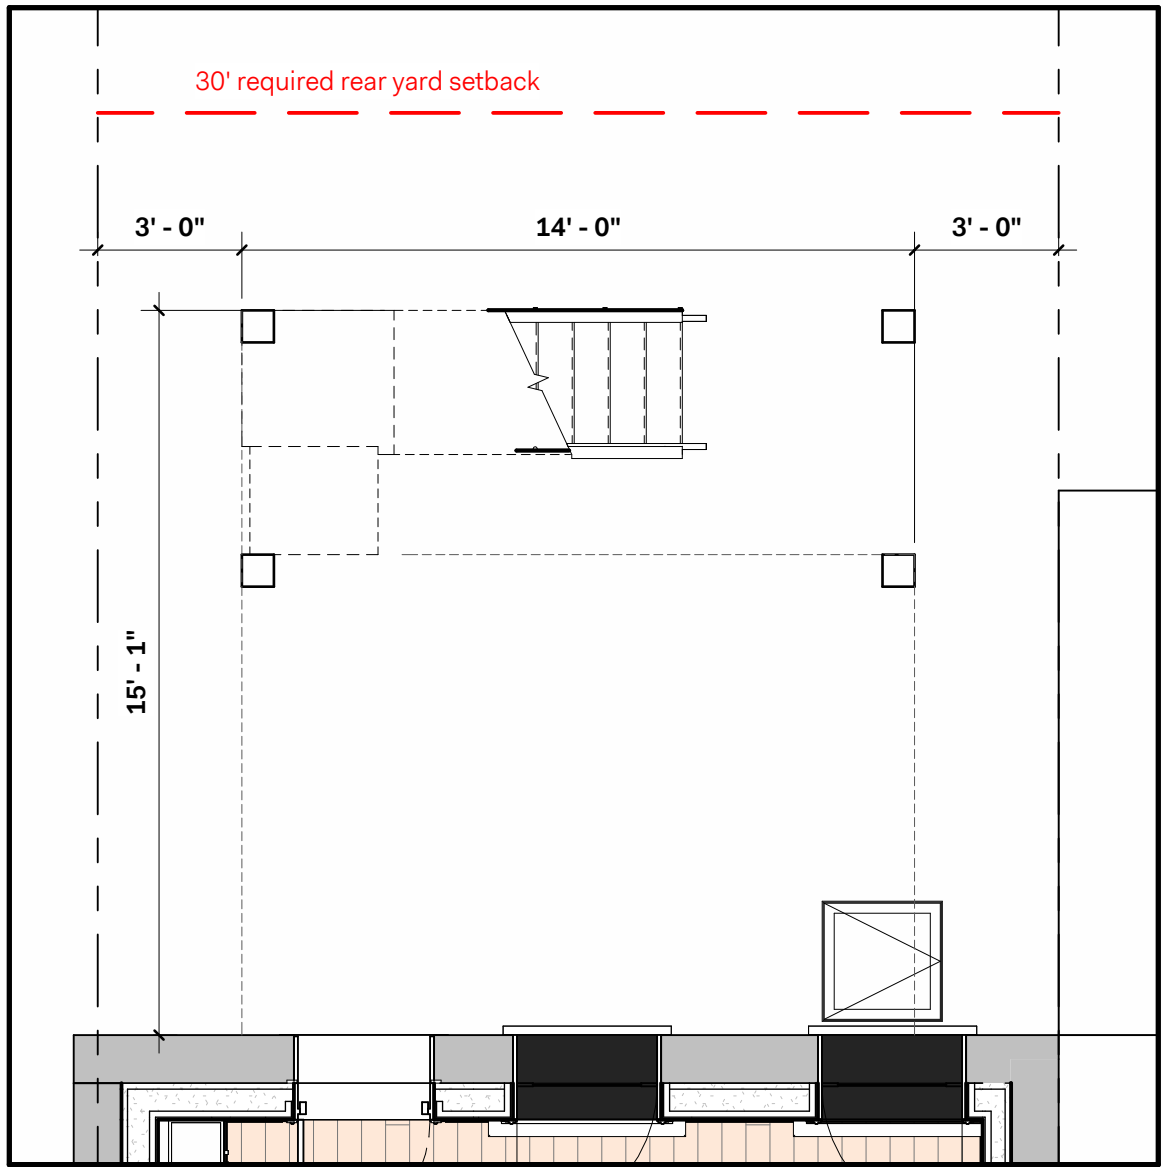


2 DECK OPTION 2 - BAS ENLARGED PLAN
1/4" = 1'-0"

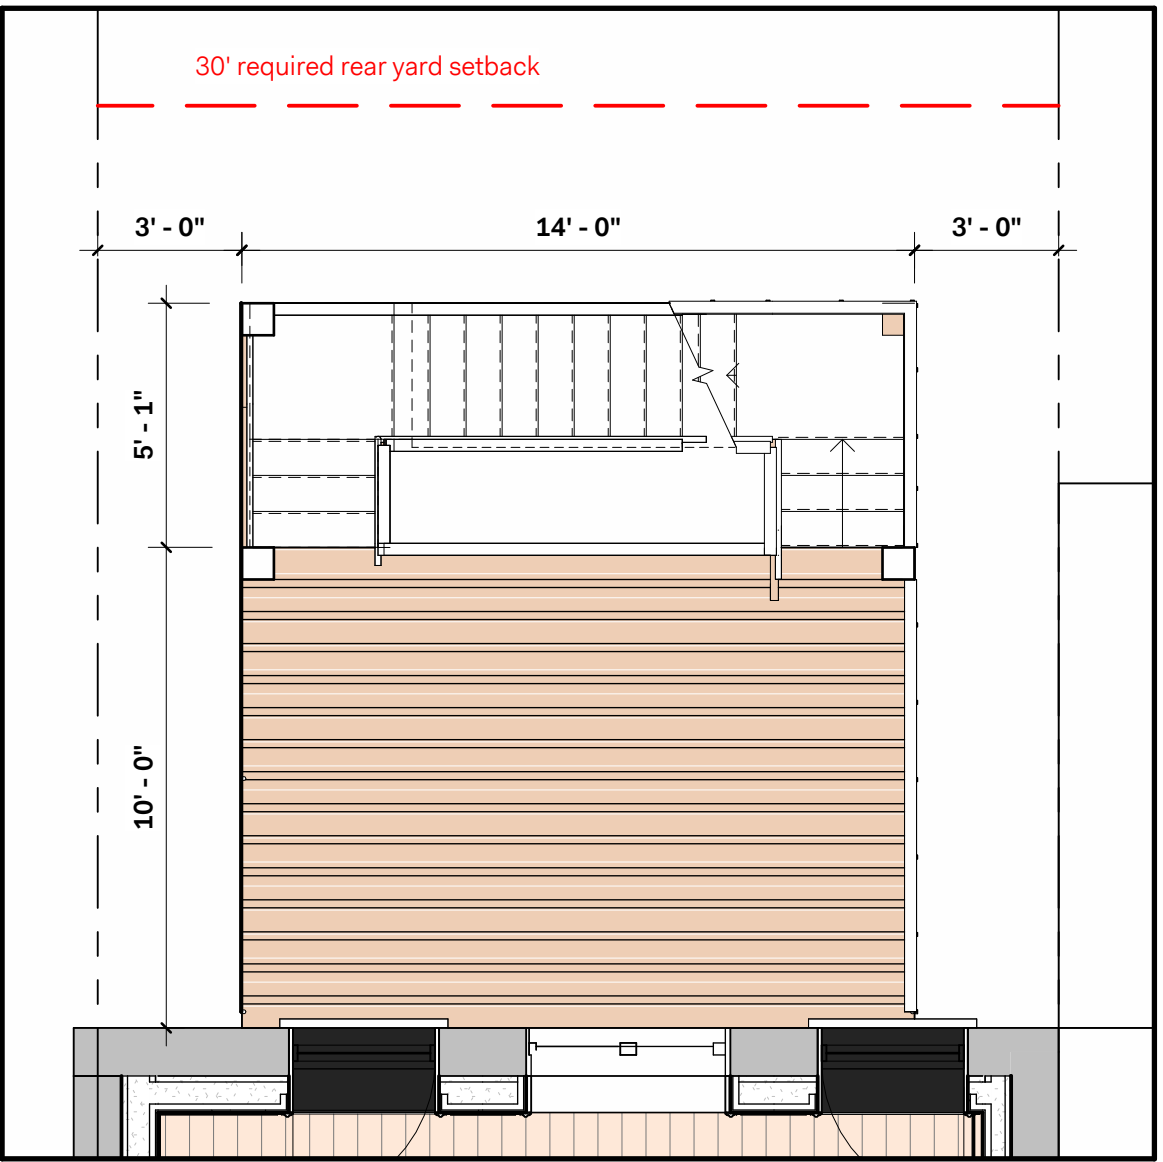

3 DECK OPTION 2 - 001 ENLARGED PLAN
1/4" = 1'-0"

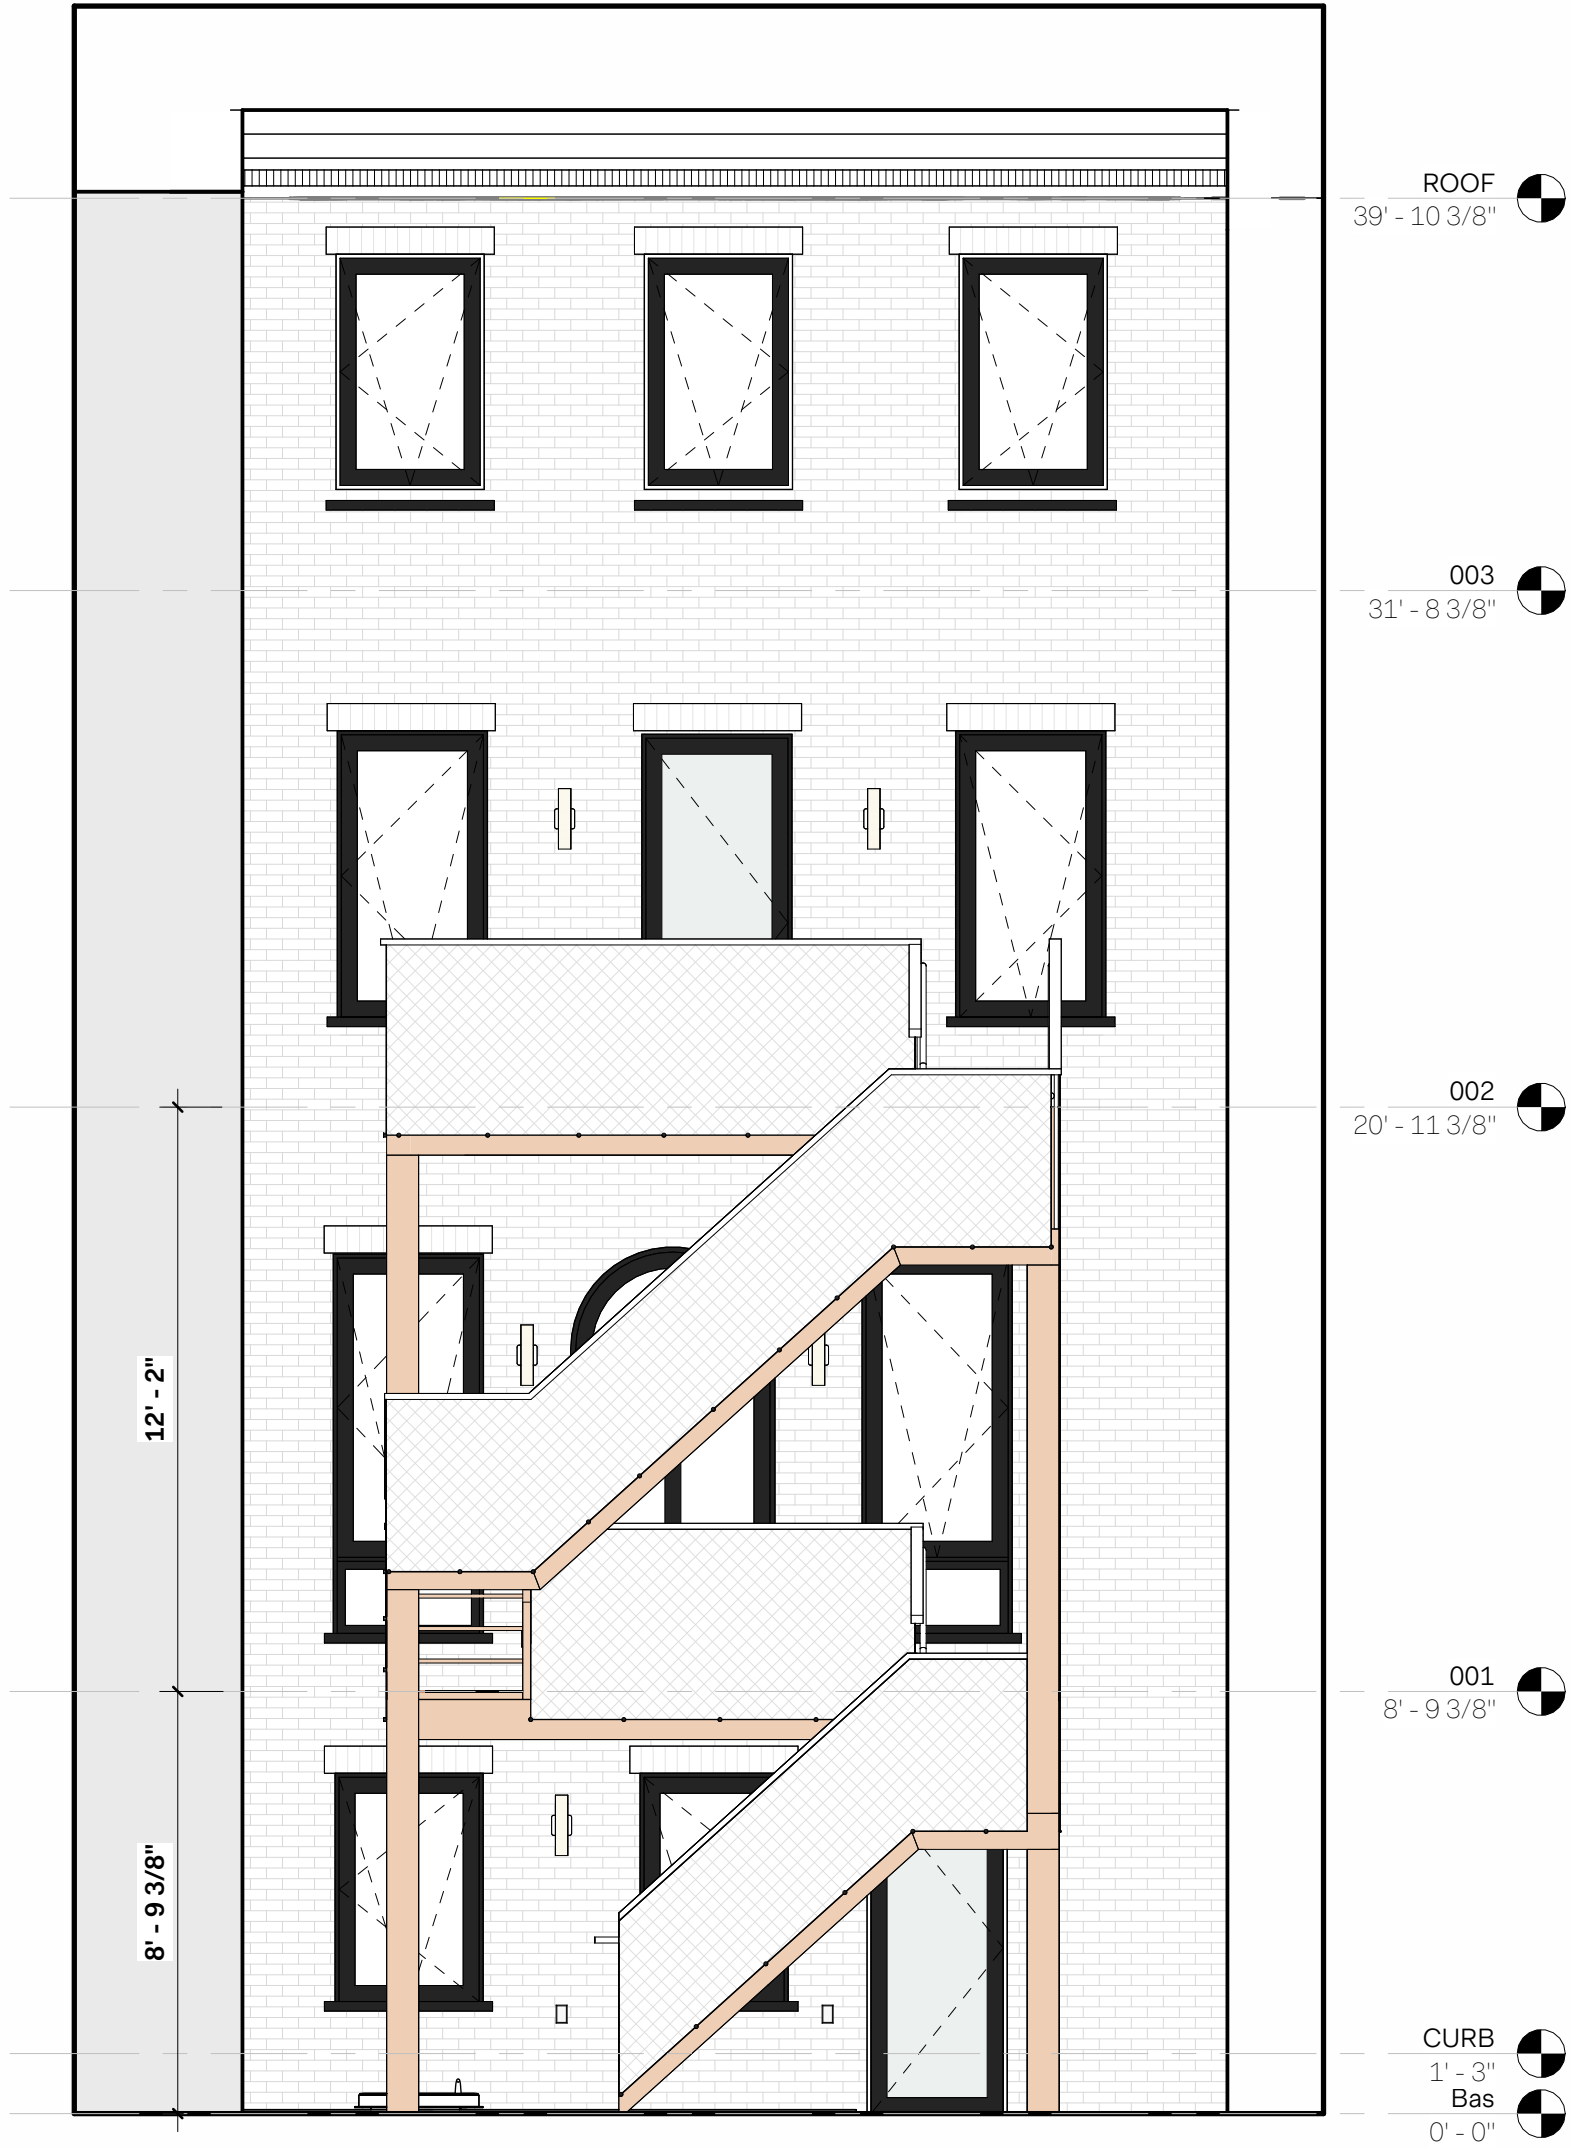

4 DECK OPTION 2 - ELEVATION
1/4" = 1'-0"

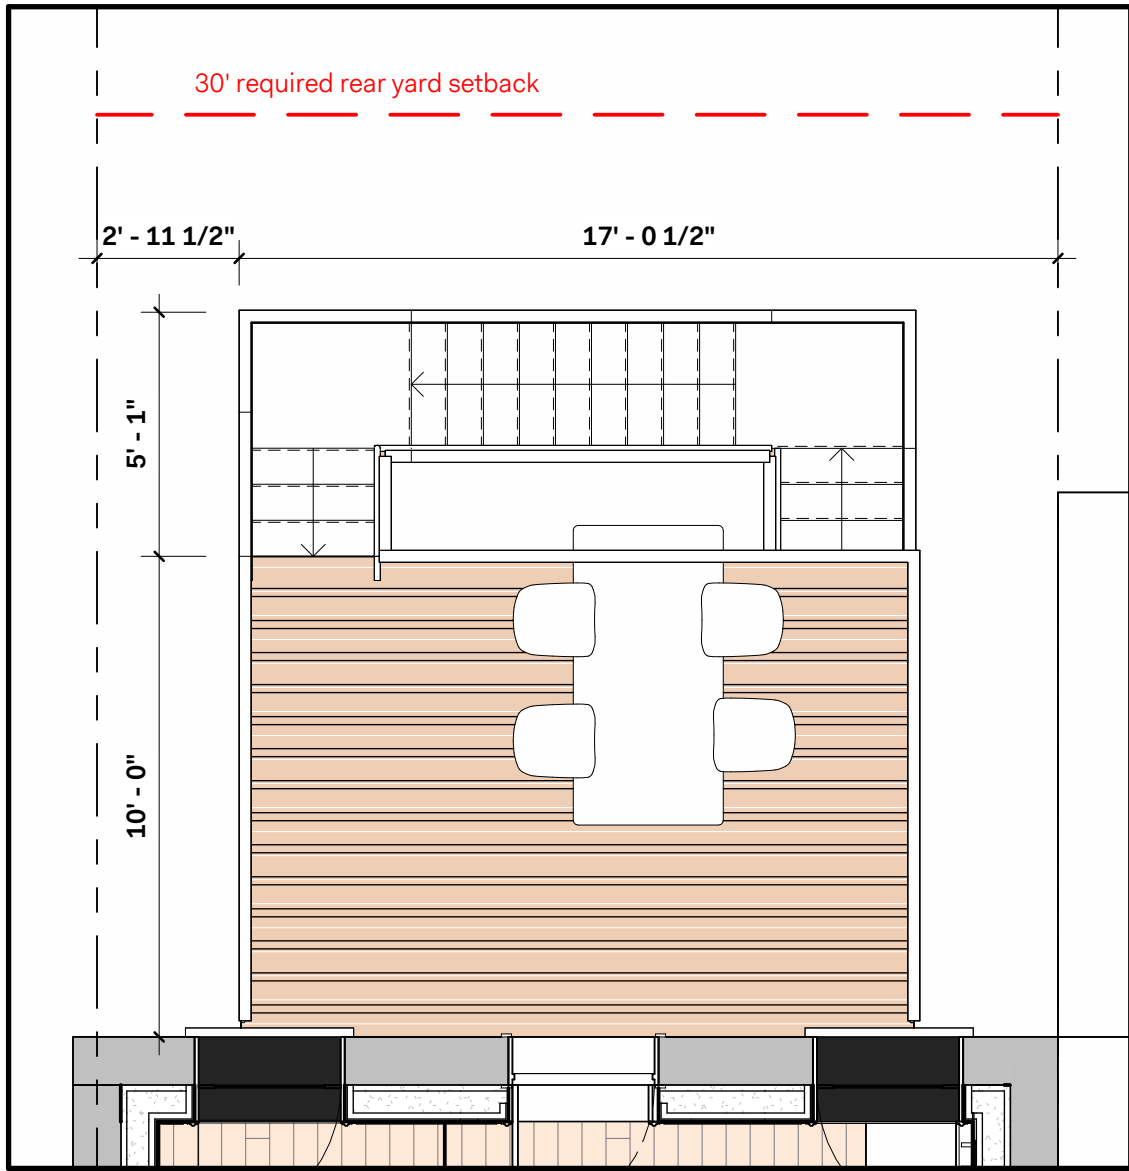

5 DECK OPTION 2 - 002 ENLARGED PLAN
1/4" = 1'-0"

CO Adaptive

Architect
CO Adaptive Architecture PLLC
Building 303, Suite 603
63 Flushing Avenue
Brooklyn, NY 11205
t. 347.588.0455
hello@coadaptive.co

Mechanical Electrical Plumbing Engineer
ABS Engineering, PLLC
37 West 37th Street, 6th Floor
New York, NY 10018
t. 212.317.2361
info@absengineer.com

Structural Engineer
Nathaniel Bergen, P.E.
225 W. 34th Street, #922
New York, NY 10012
t. 696.598.0025
nathaniel.bergen@gmail.com

Revision Number	Date	Revision Description
-----------------	------	----------------------

Owner & Project Information

Q142
142 QUINCY STREET, BROOKLYN, NY 11216
Ariel Azoff • Gabre Stein, Elizabeth Zehn • Will Cudney

DOB NOW #
B08048986

Drawing Title
EXTERIOR DETAILS - DECK & RAILING - OPTION 2
Drawing Scale: 1/4" = 1'-0"
100% @ A1 (24" x 36")

Project Number

Q142

Issue Date

11-25-2024

Sheet Number

48 / 61

Drawing Number

A-552.00

Copyright 2023 CO Adaptive Architecture PLLC All rights reserved