




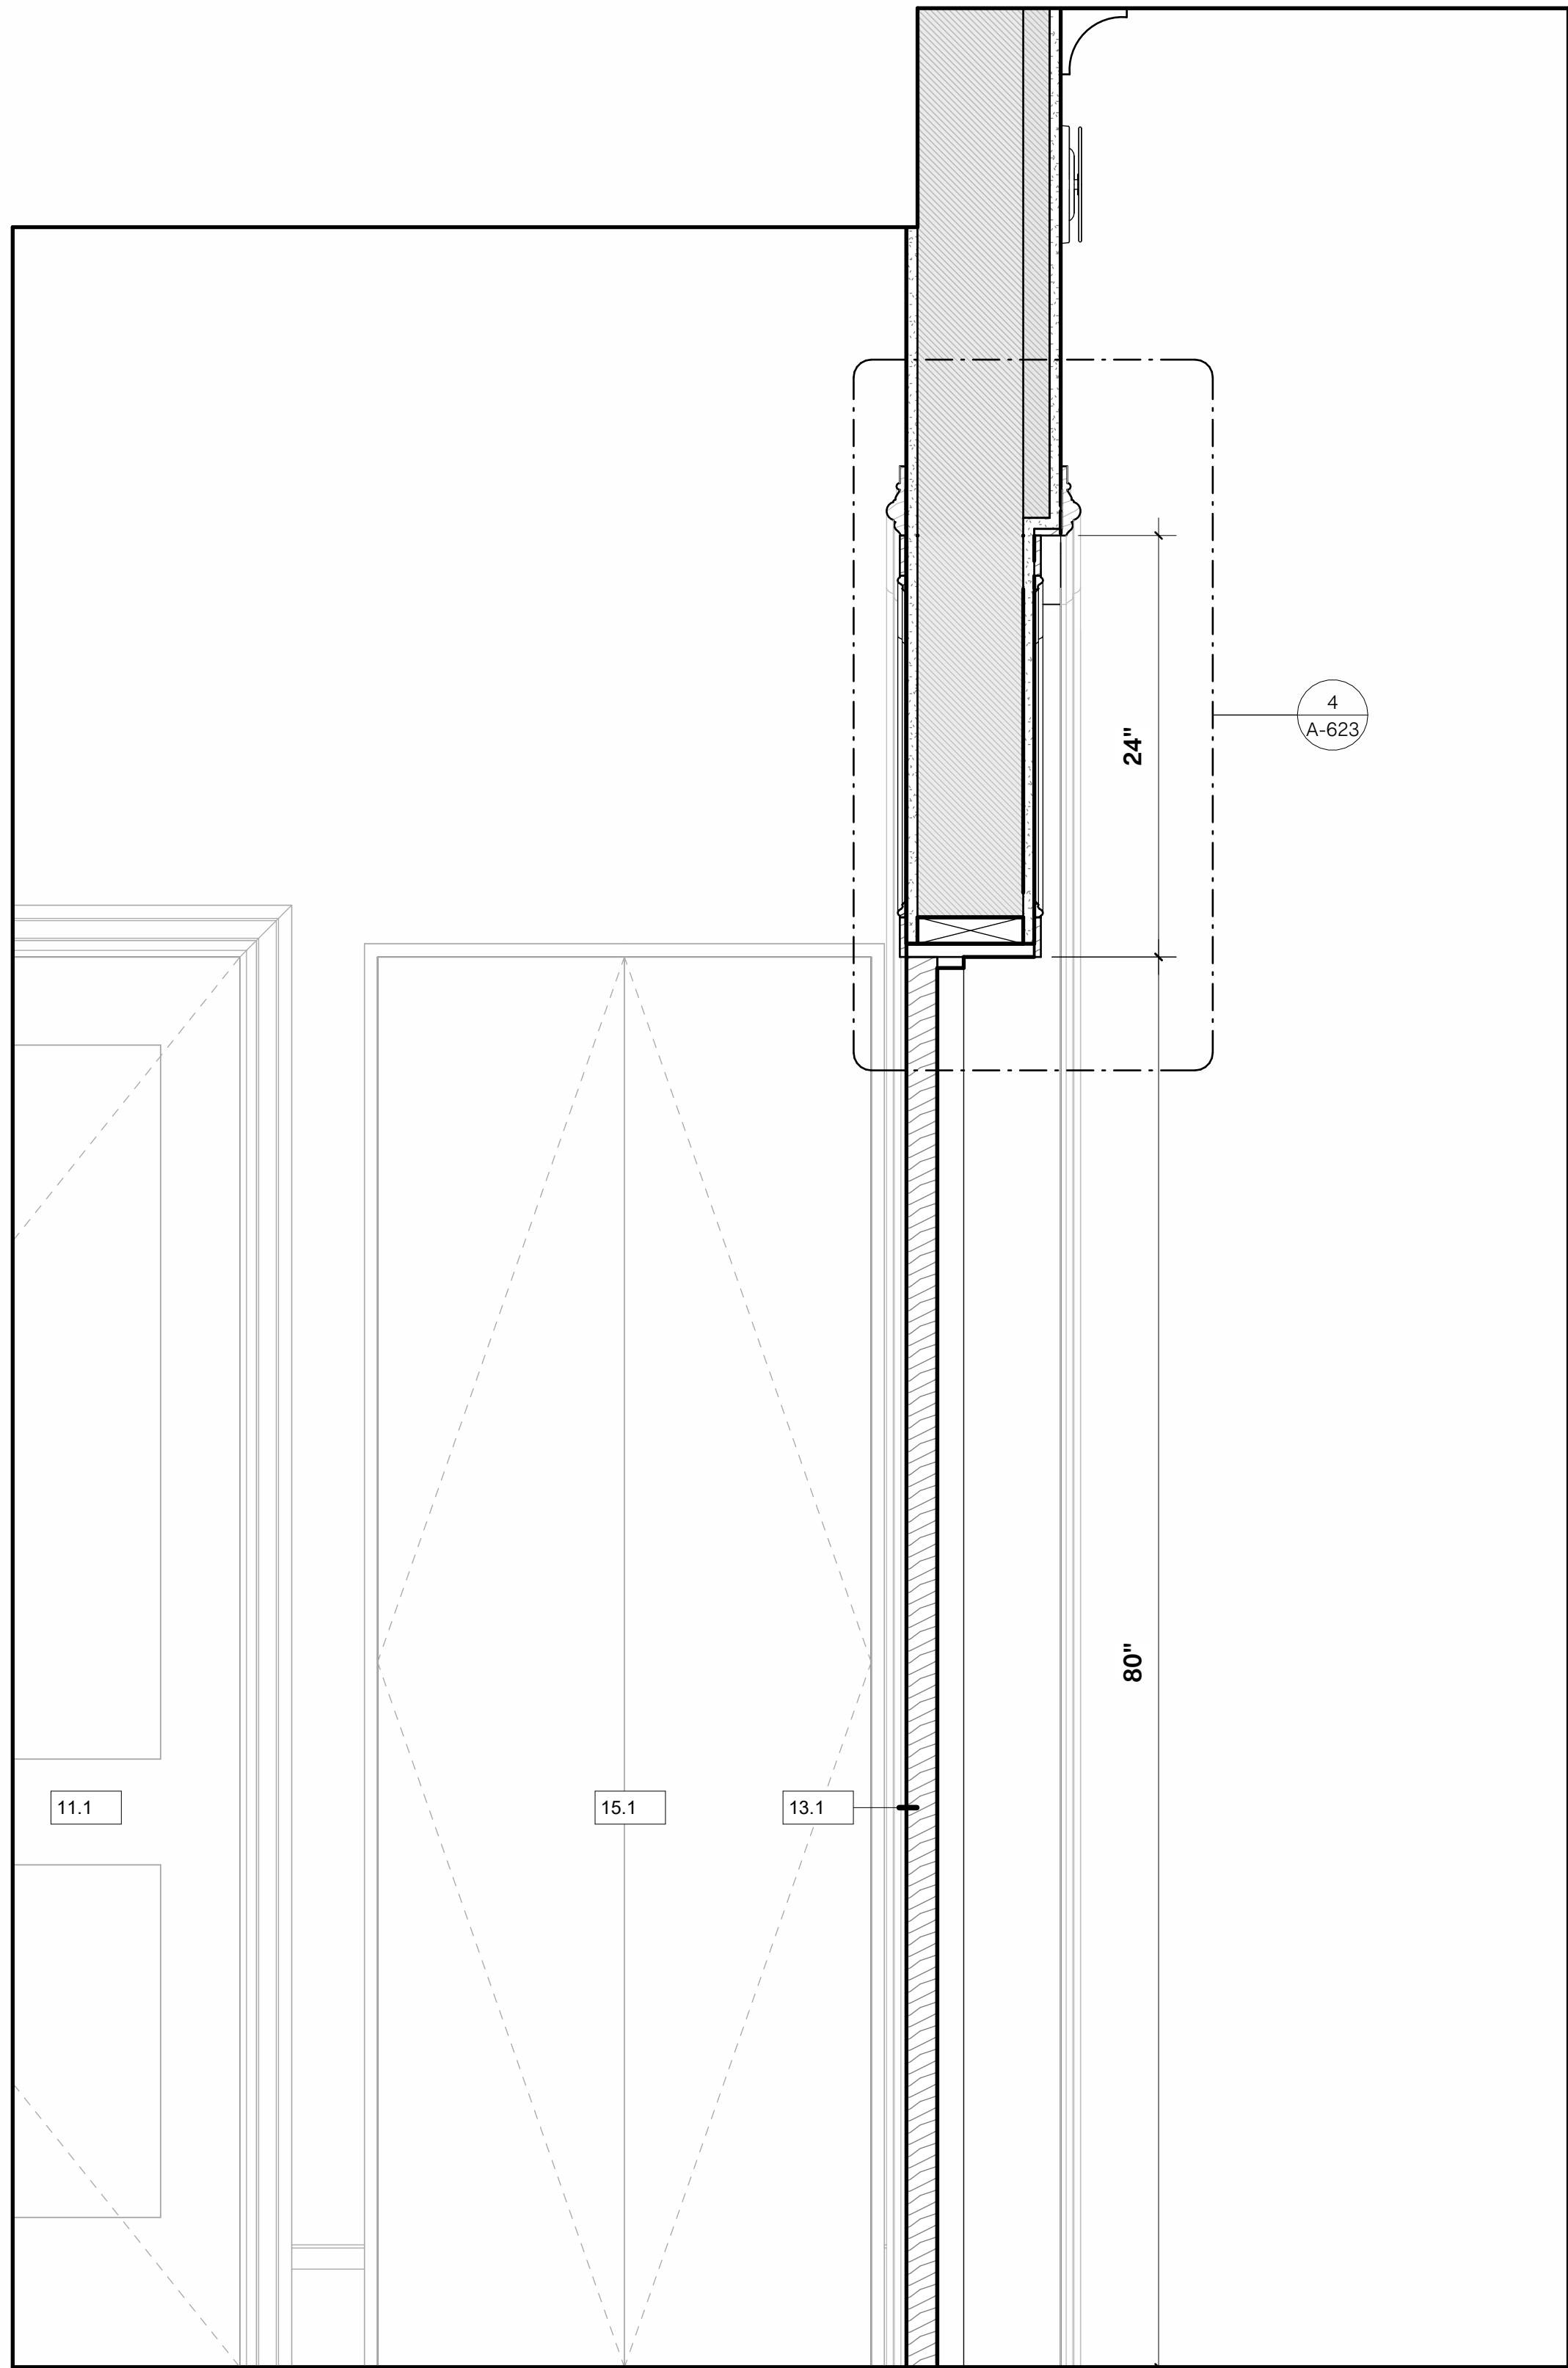


1 DOOR 13.1 SECTION DETAIL
1 1/2" = 1'-0"

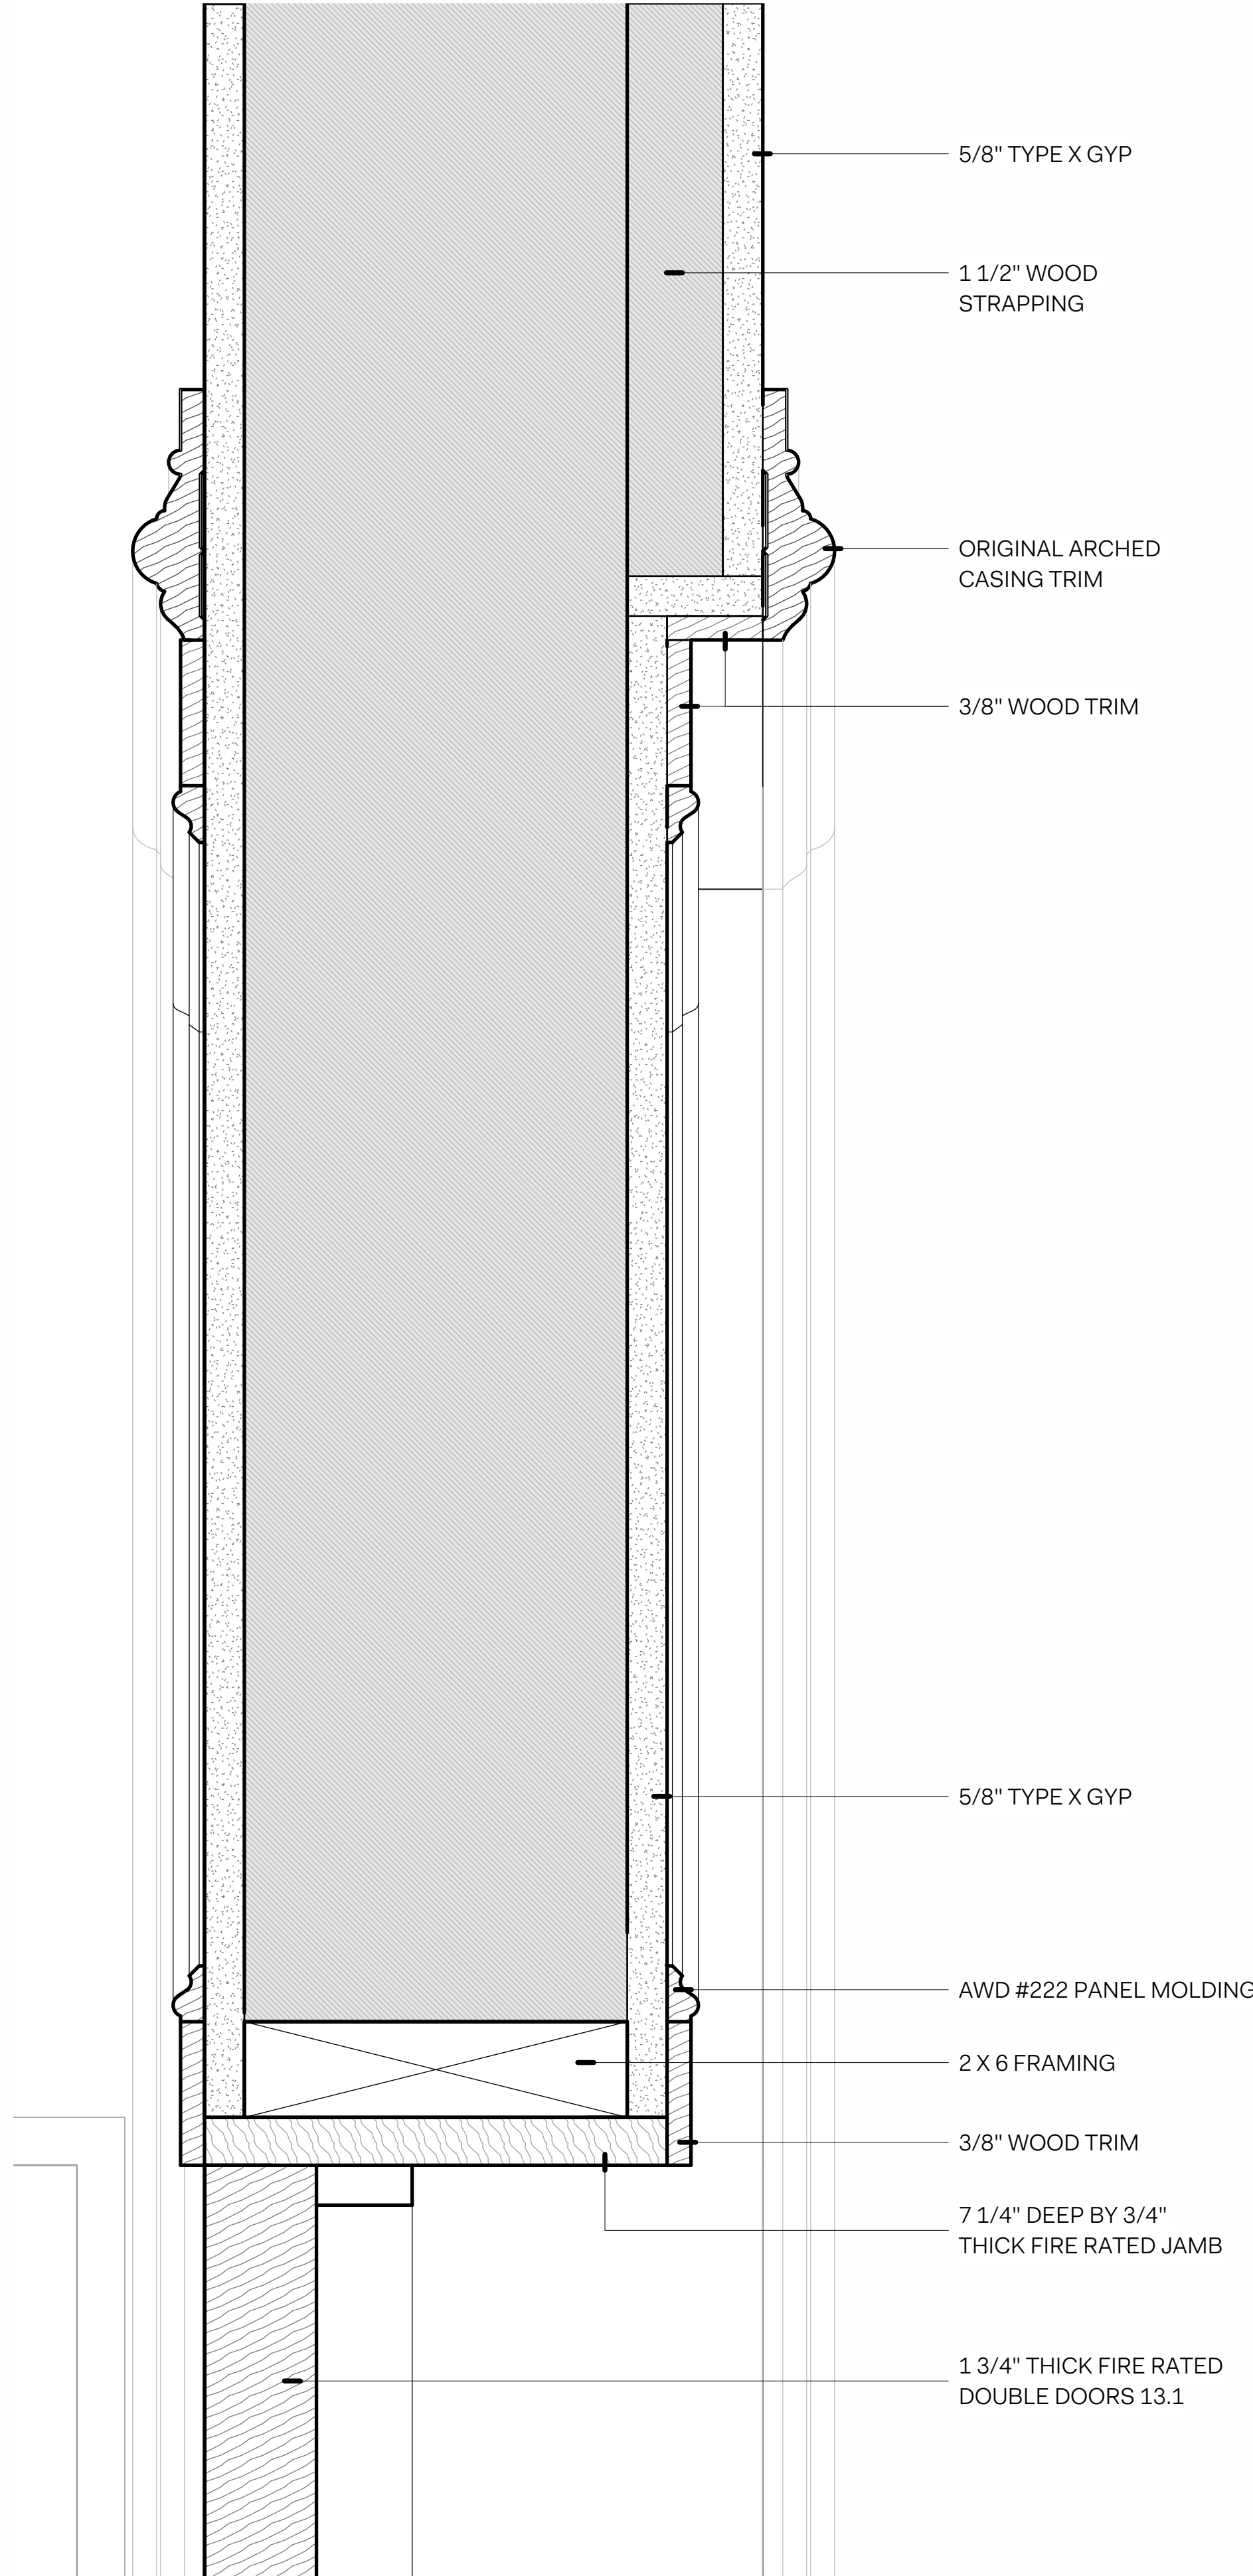

4 DOOR 13.1 TRANSOM SECTION DETAIL
6" = 1'-0"

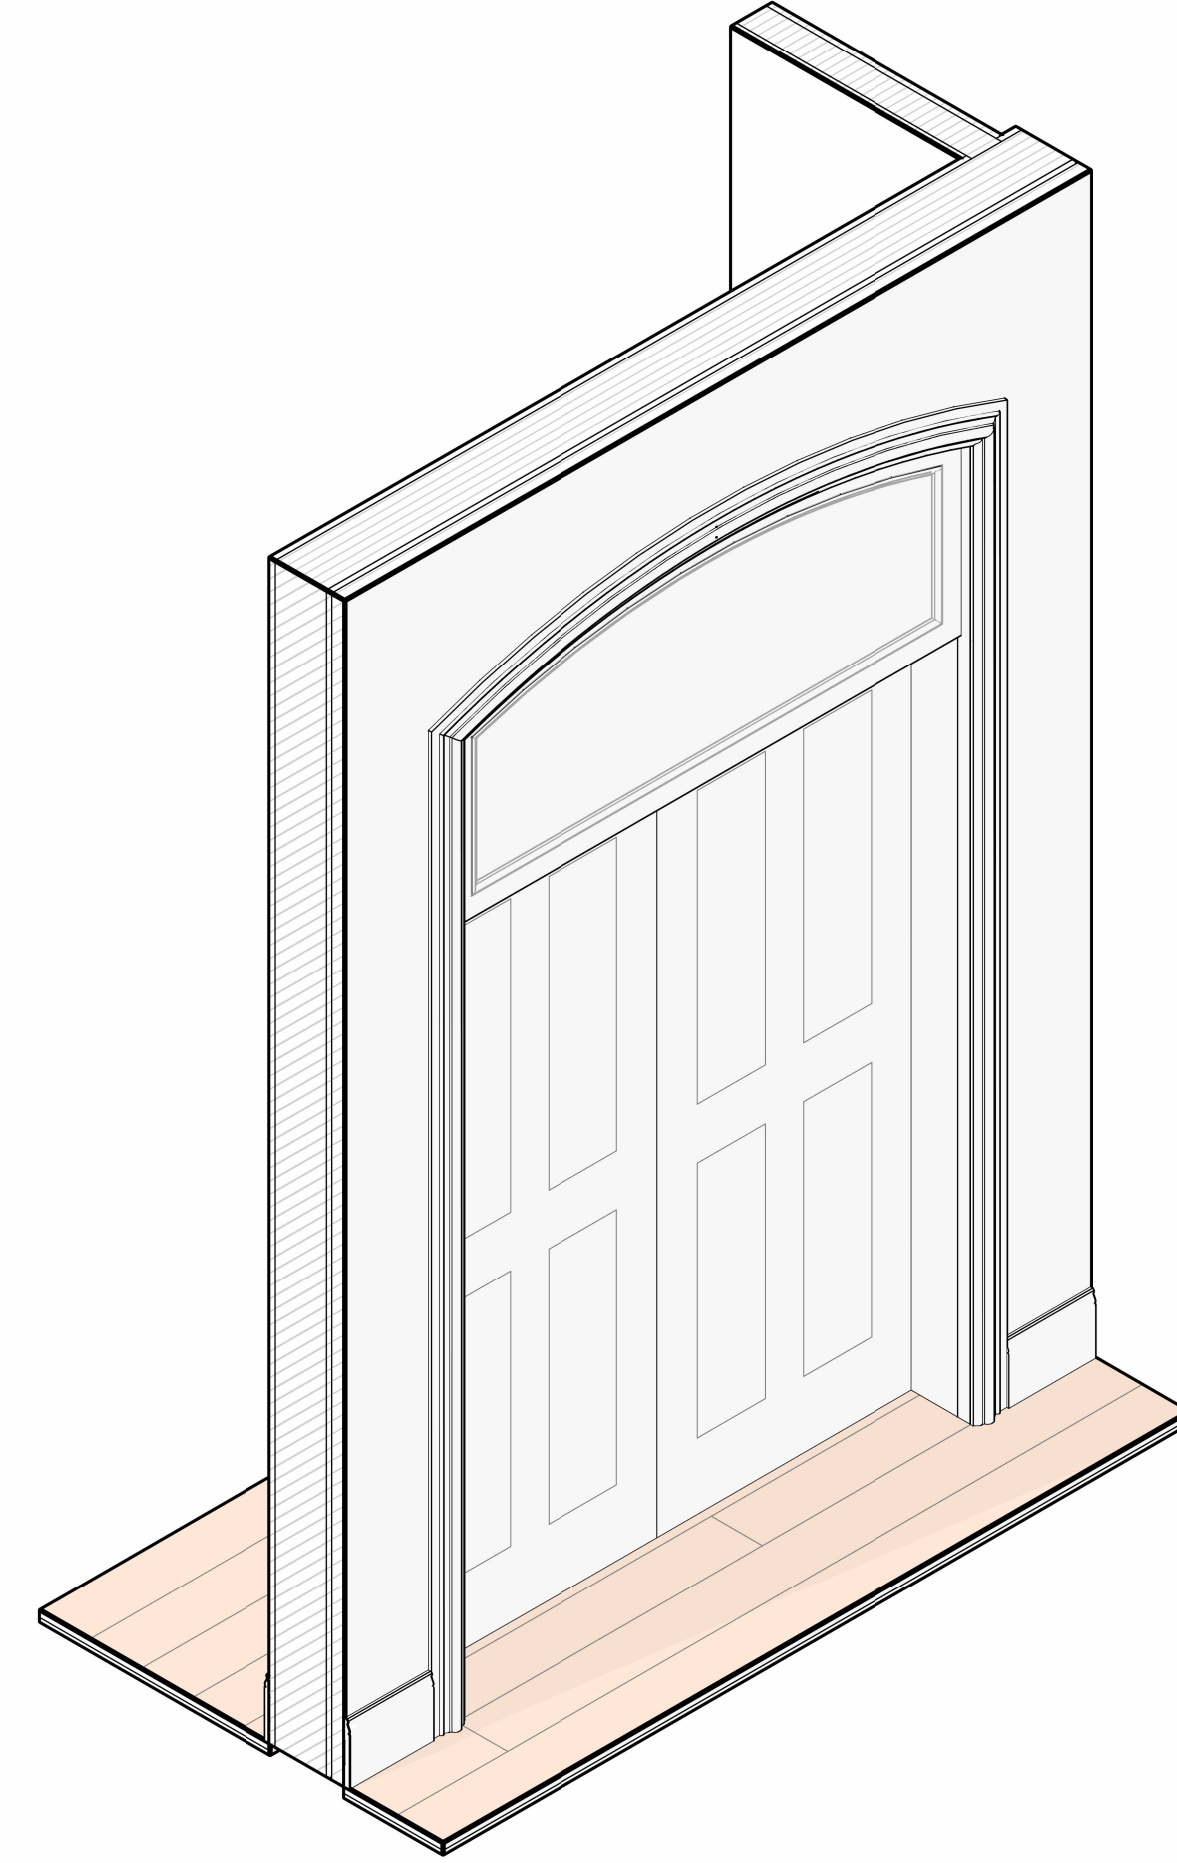

2 DOOR 13.1 - DINING ROOM SIDE AXON

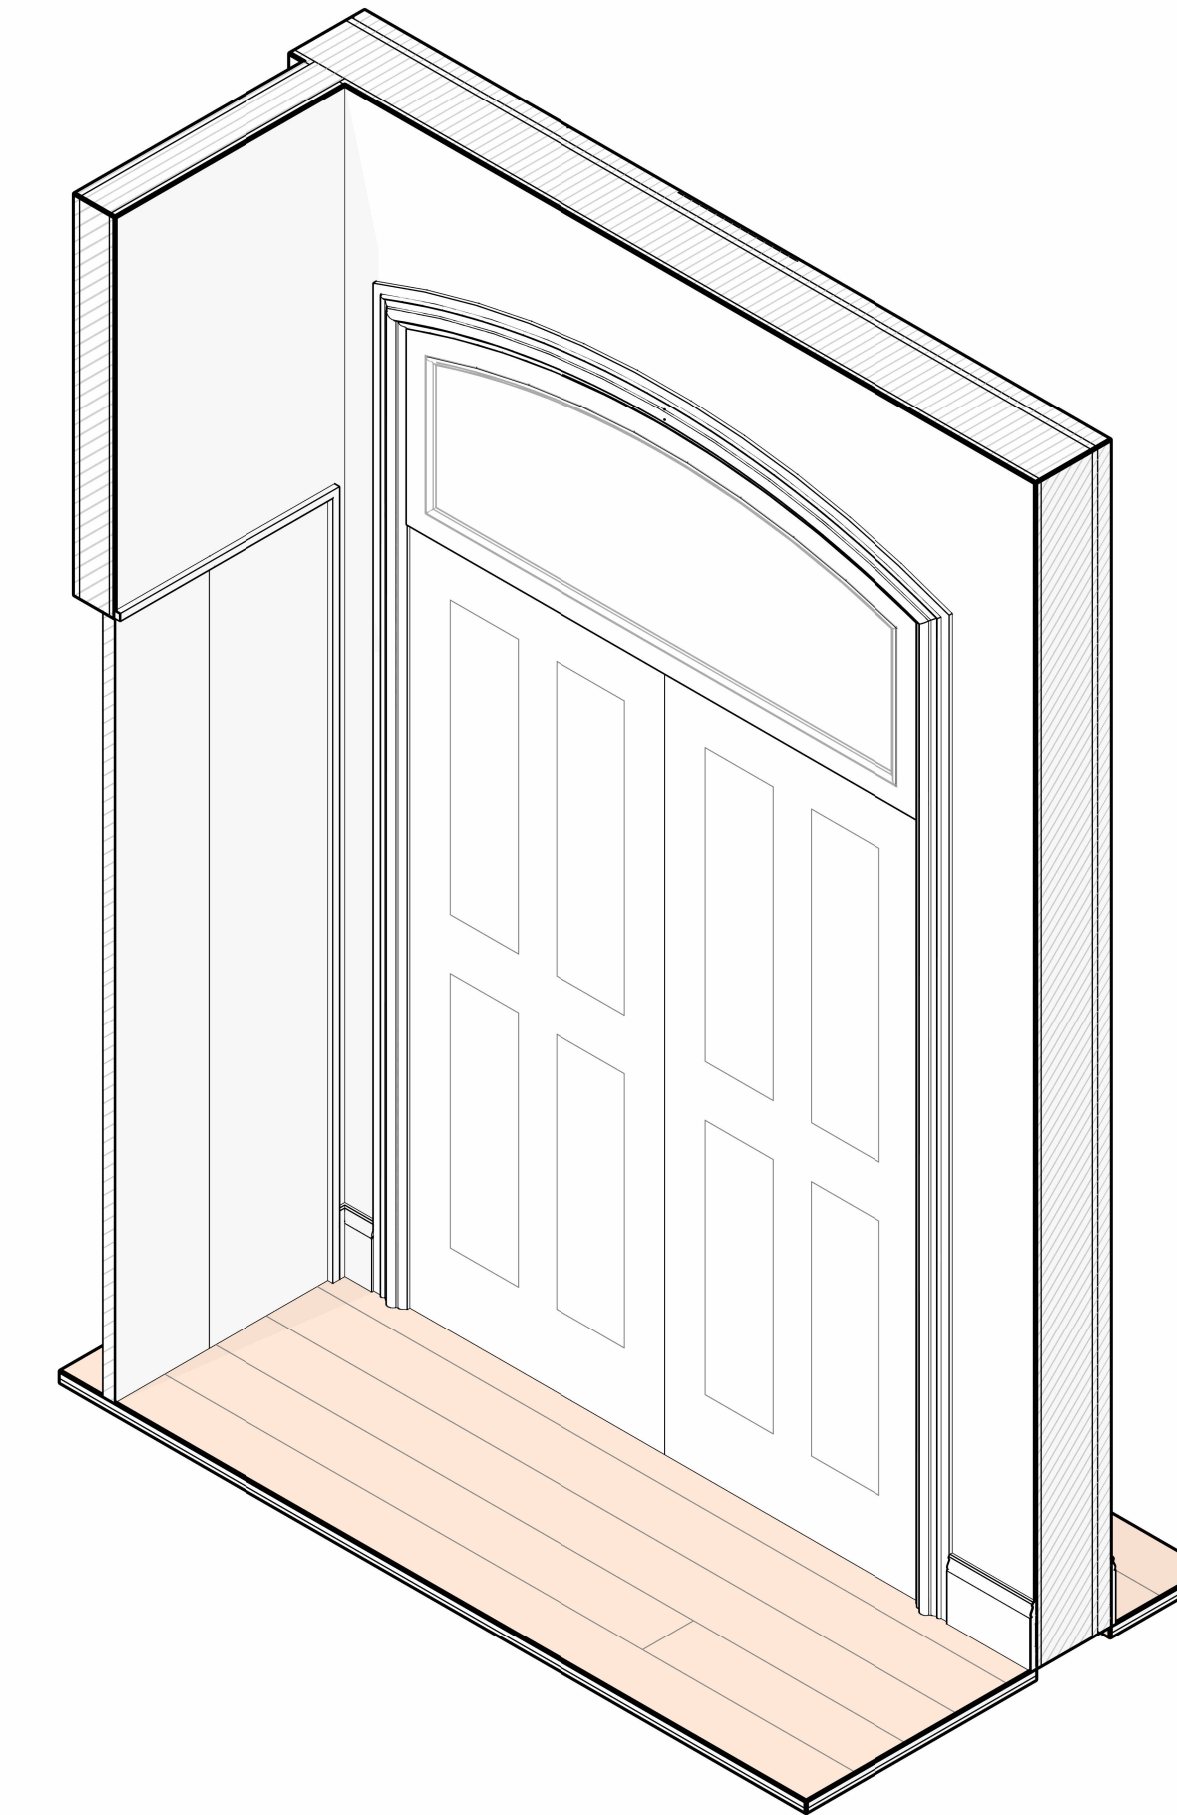

3 DOOR 13.1 - VESTIBULE SIDE AXON

CO Adaptive

Architect
CO Adaptive Architecture PLLC
Building 303, Suite 603
63 Flushing Avenue
Brooklyn, NY 11238
t. 347.686.0465
hello@coadaptive.co

Mechanical Electrical Plumbing Engineer
ABS Engineering, PLLC
37 West 57th Street, 8th Floor
New York, NY 10018
t. 212.217.2261
info@absengineer.com

Structural Engineer
Nathaniel Bergen, P.E.
225 W. 34th Street, #922
New York, NY 10012
t. 860.588.0025
nathaniel.bergen@gmail.com

Rev. #	Date	Revision Description
8	03-10-2025	General Update

Owner & Project Information

Q142
142 QUINCY STREET, BROOKLYN, NY 11216

Ariel Azoff • Gabe Stein, Elizabeth Zehn • Will Cudney

DOB NOW #

800048986

Drawing Title

**INTERIOR DETAILS - FIRE
RATED DOOR 13.1 DETAILS**

Drawing Scale As indicated

100% @ Amax D (24" x 36")

Project Number

Q142

Issue Date

03-10-2025

Sheet Number

57 / 61

Drawing Number

A-623.00