




RAILINGS HIDDEN FOR VISIBILITY

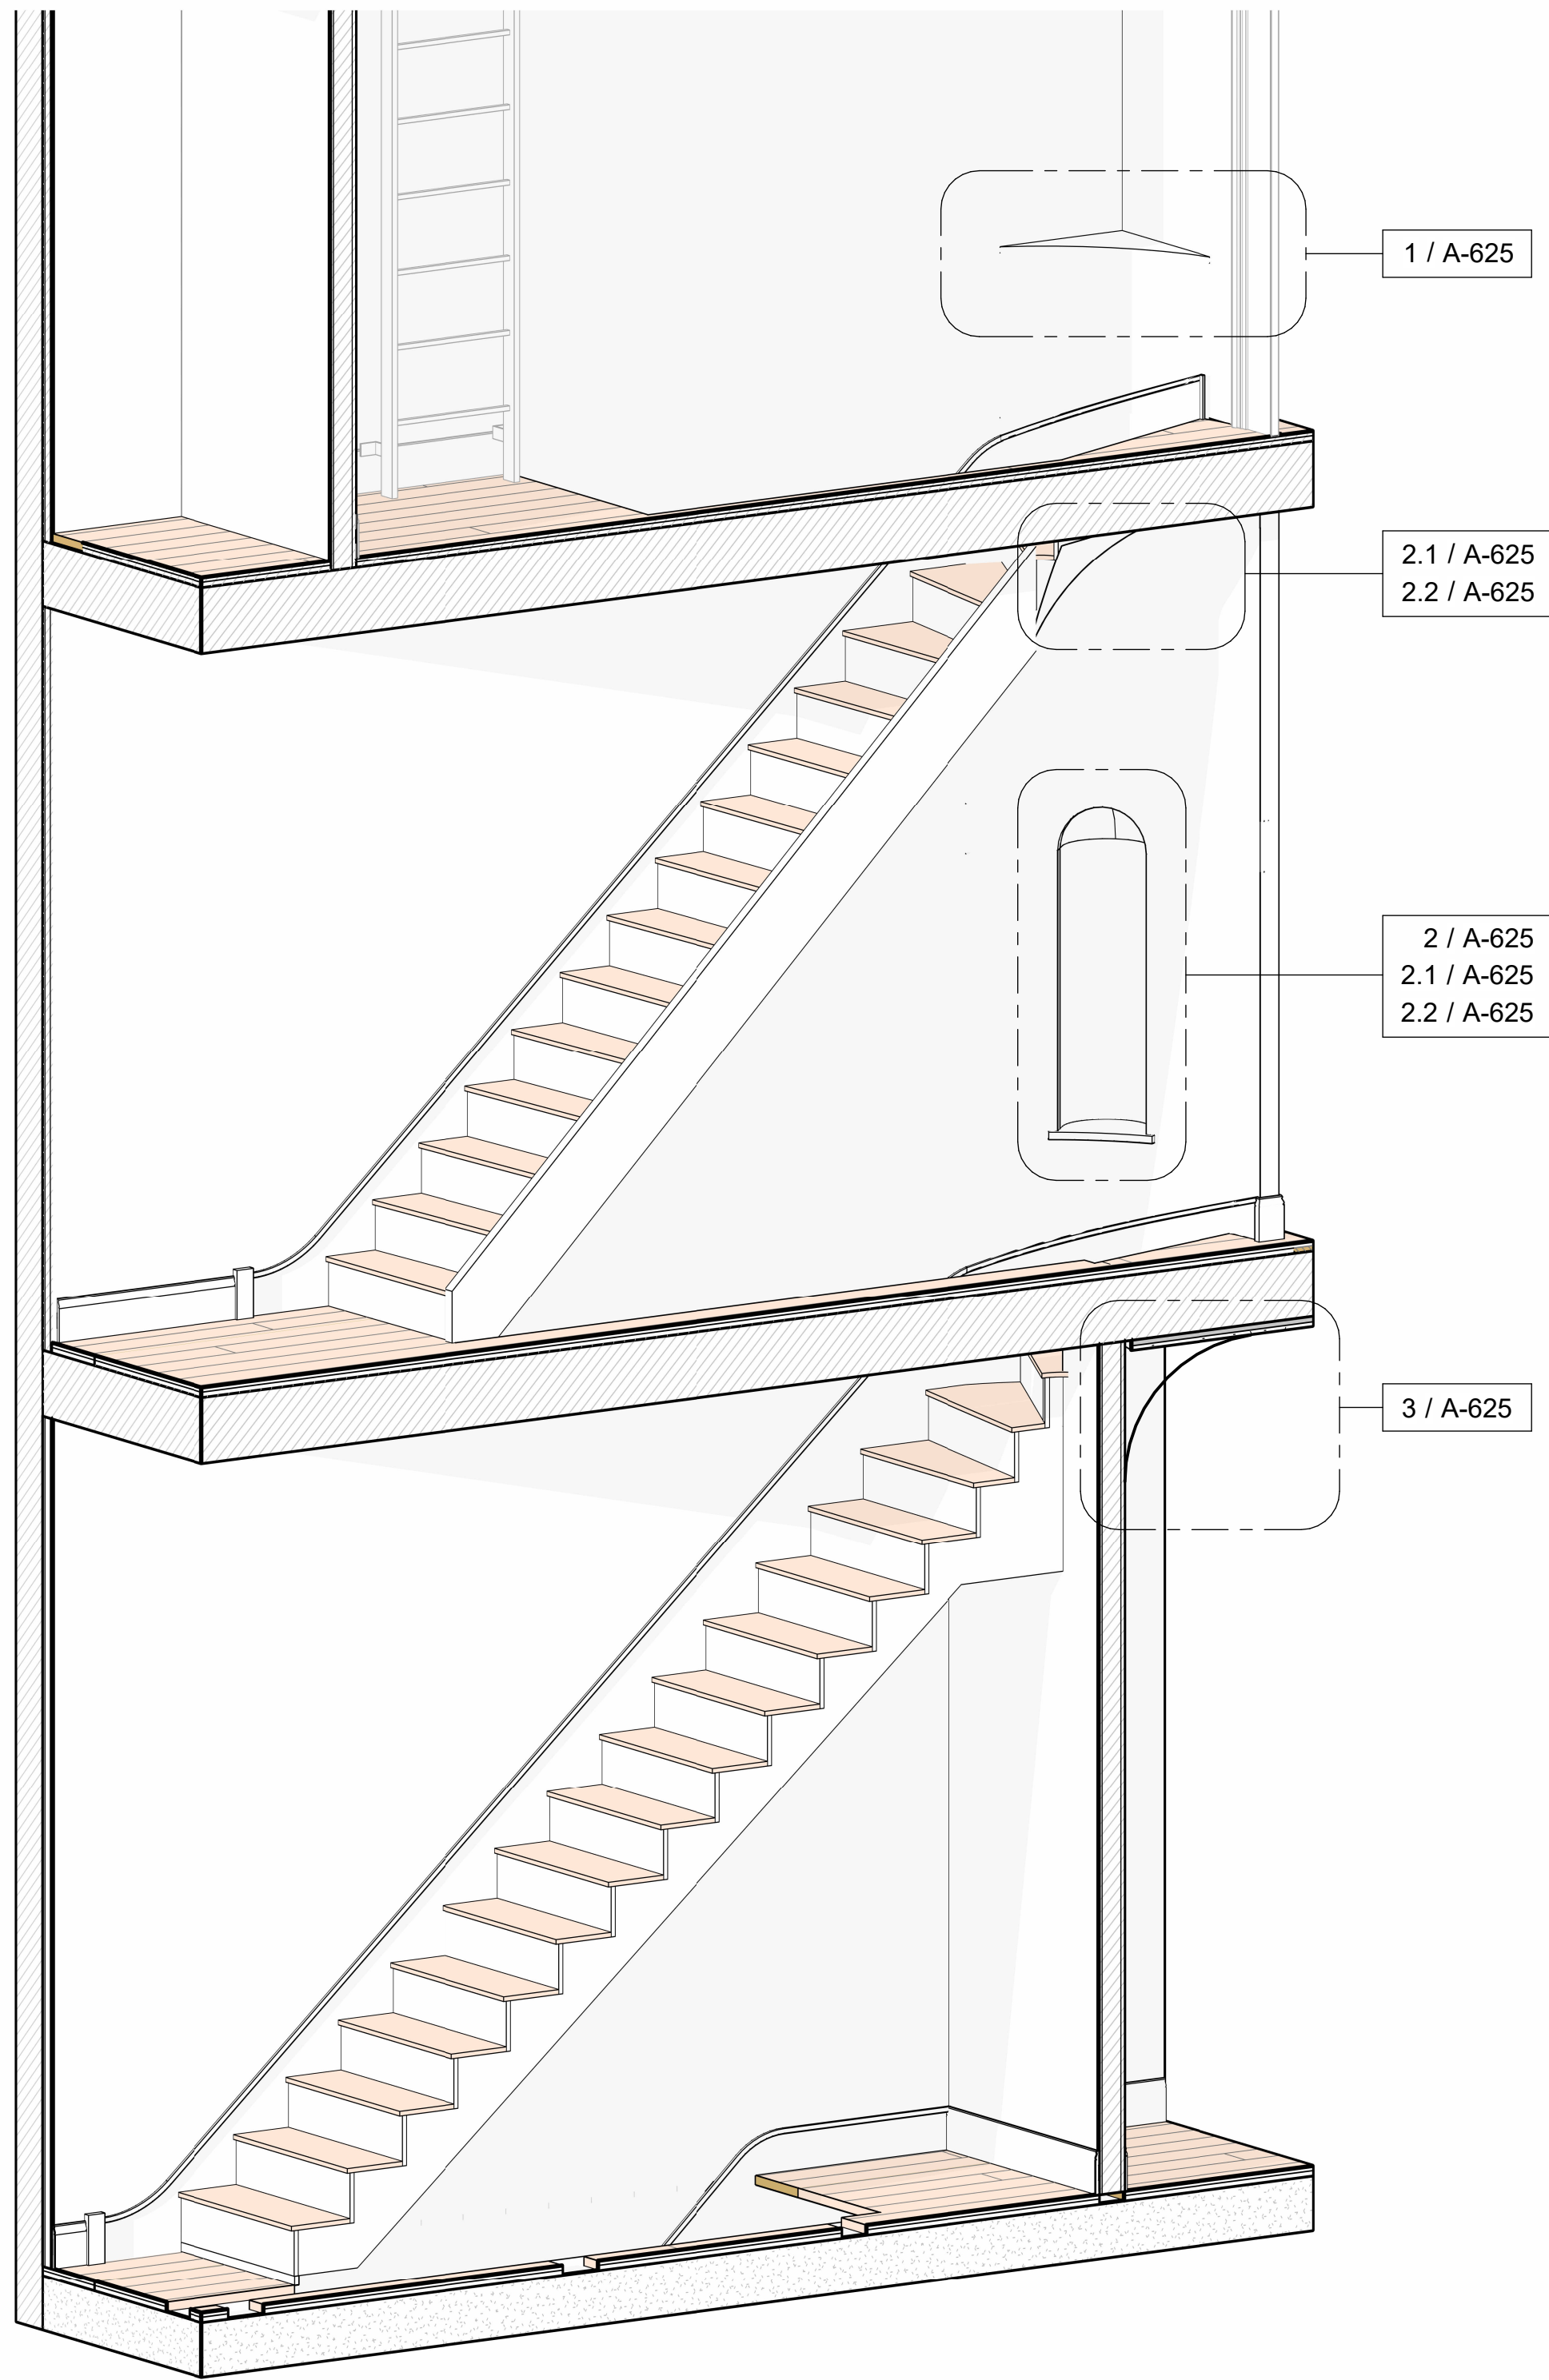


0 001, 002, 003 - STAIRWAY AXON

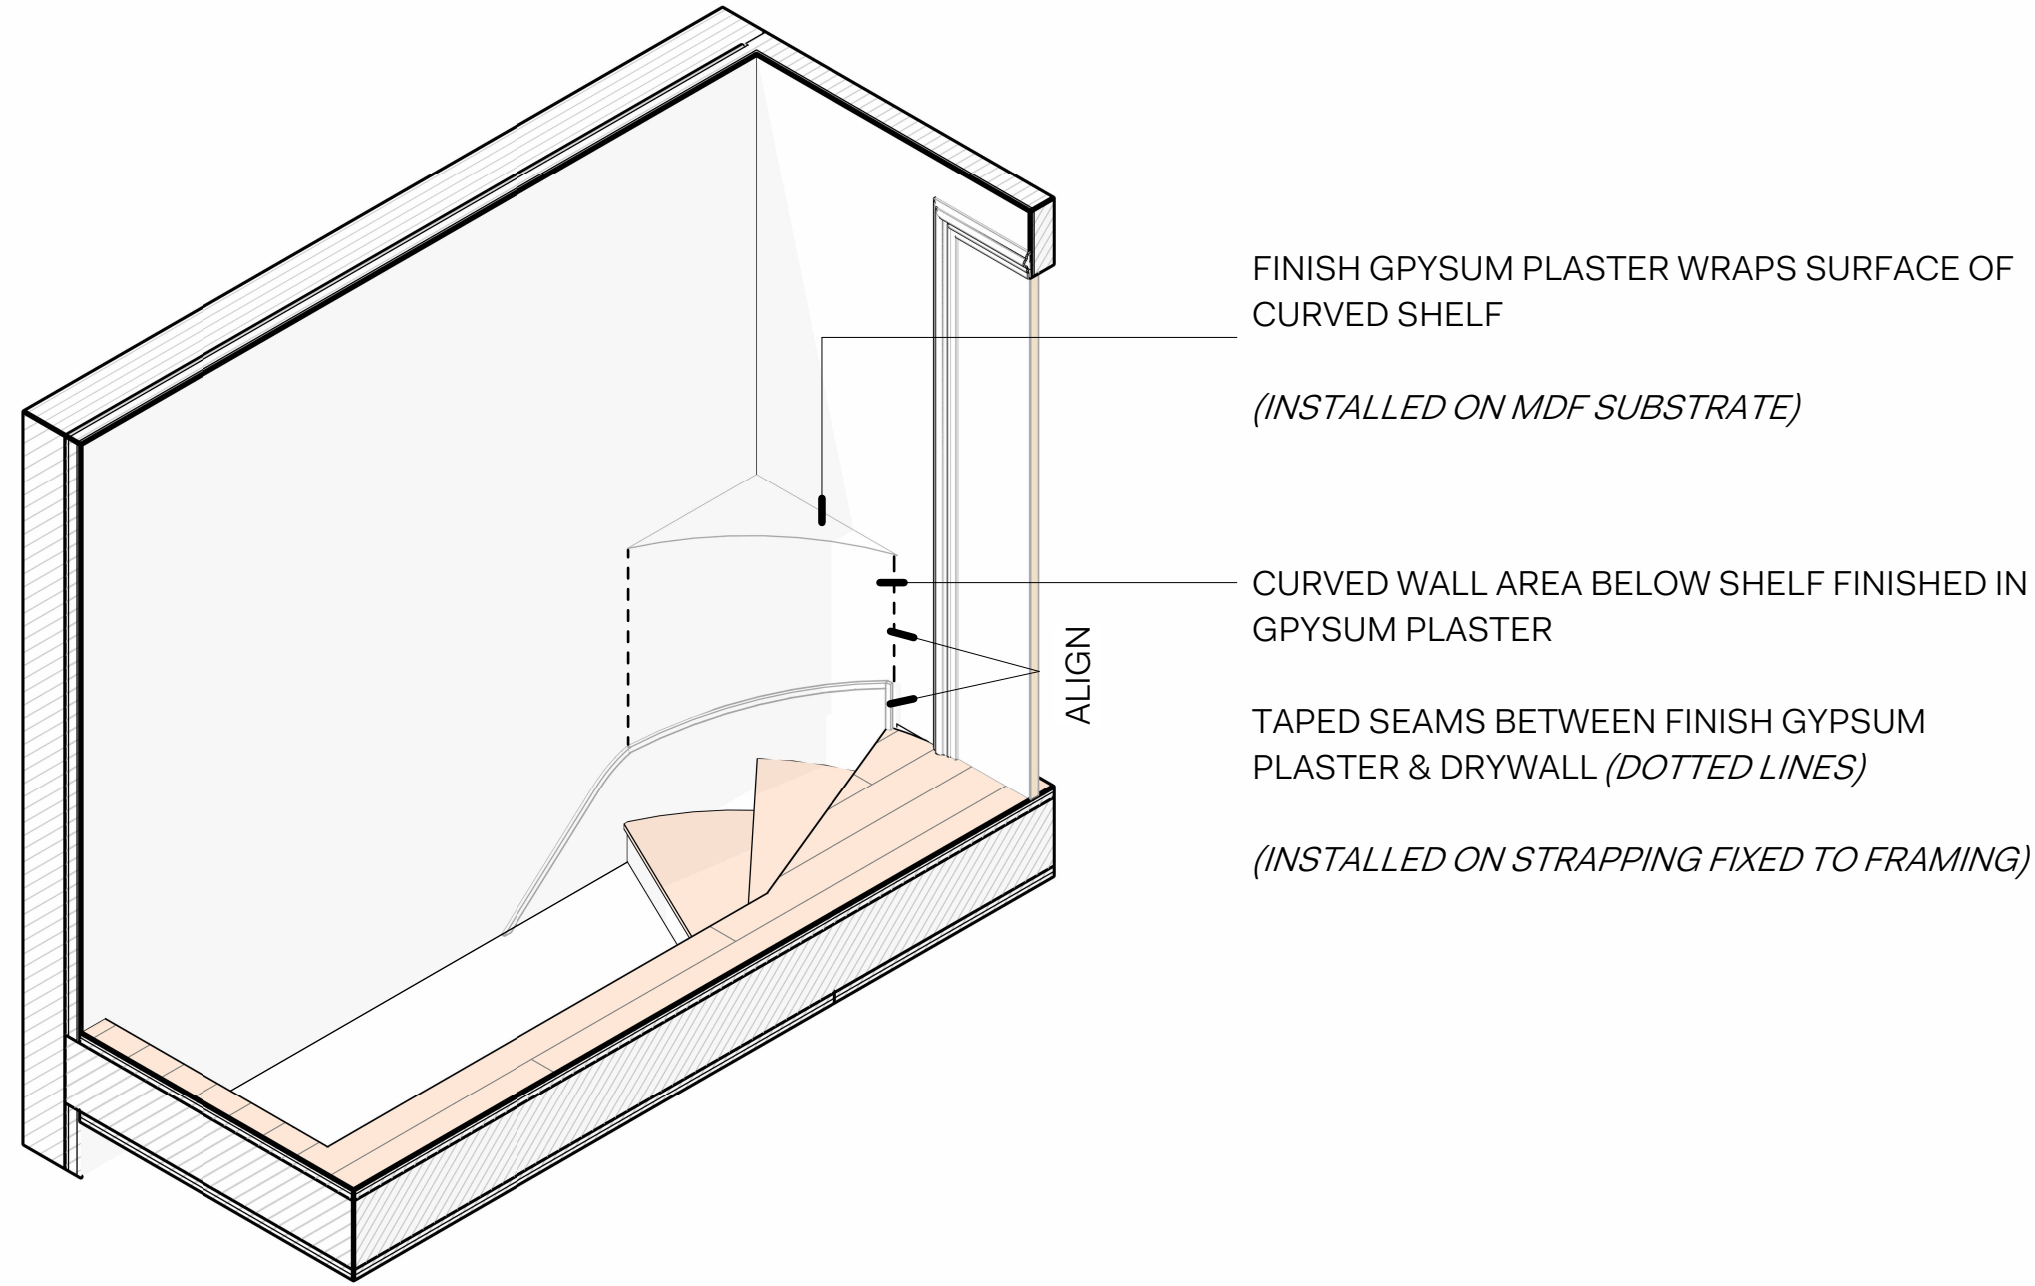

1 003 - UPPER STAIR LANDING CURVED SHELF & WALL PLASTER DETAIL

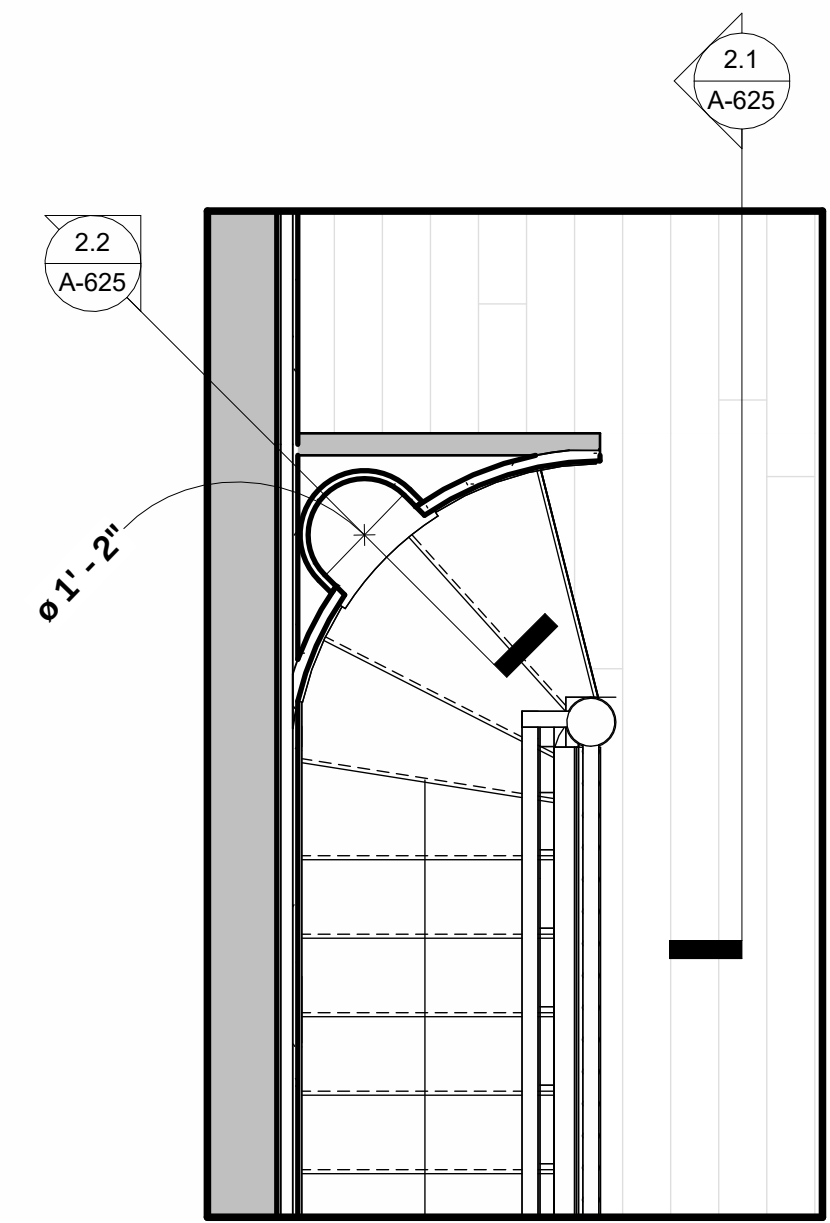


2 002 - UPPER STAIR LANDING PLAN
1/2" = 1'-0"

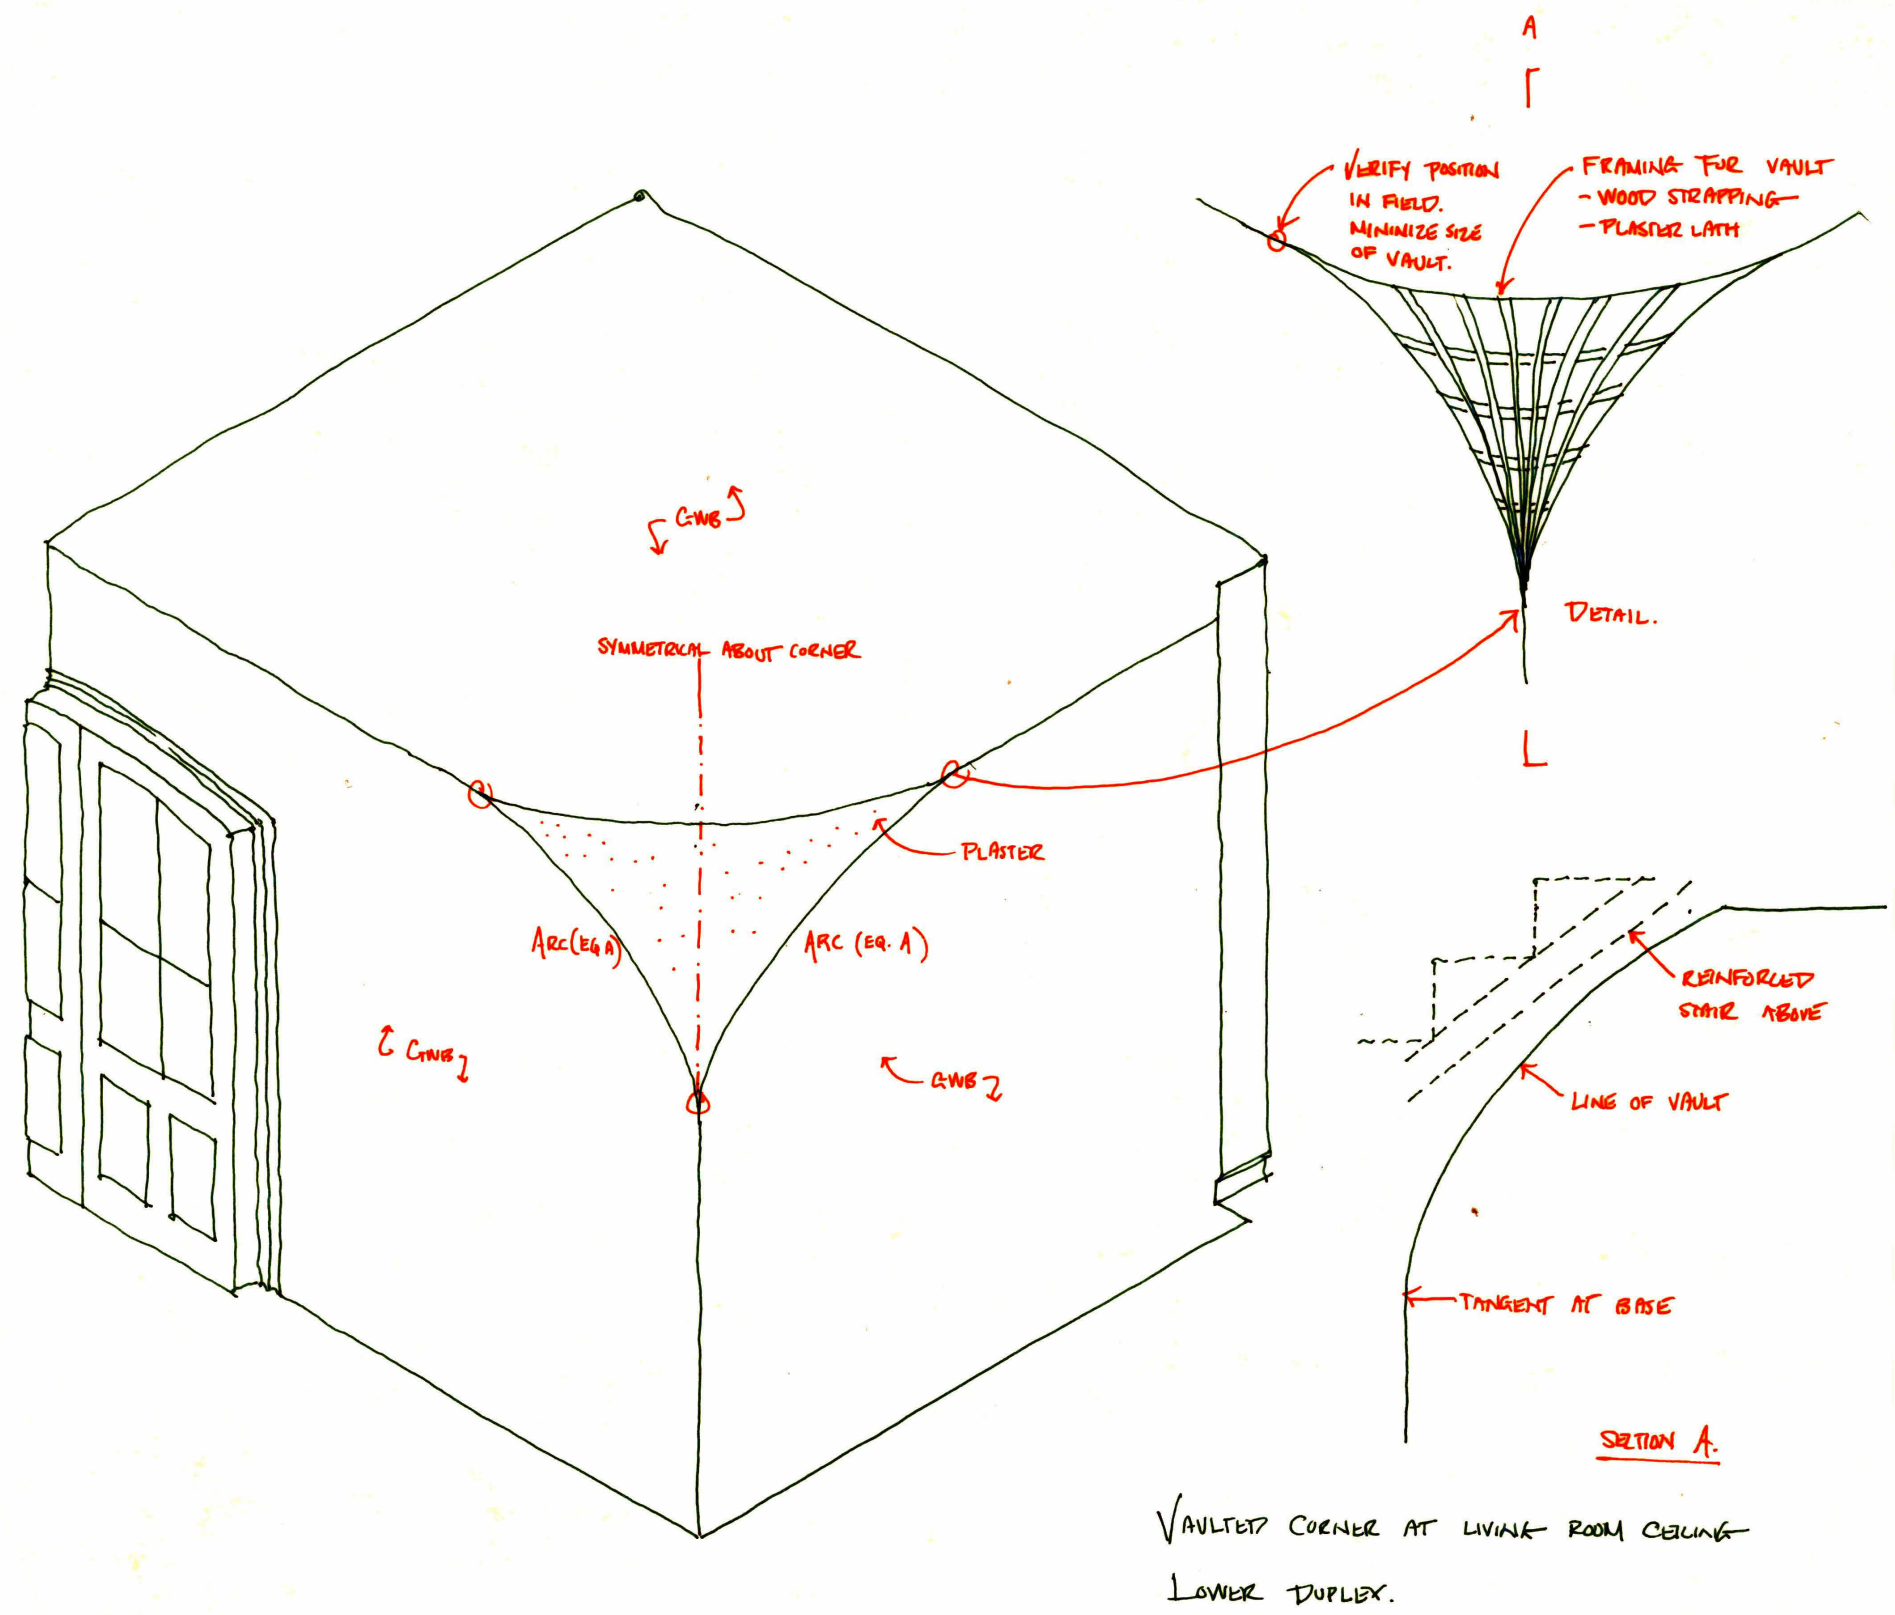

3 001 - LIVING ROOM UNDERSTAIR PLASTER DETAIL
3/8" = 1'-0"

FINISH GYPSUM PLASTER FOLLOWING UNDERSIDE OF STAIR CURVE
(INSTALLED ON STRAPPING FIXED TO STAIR FRAMING)

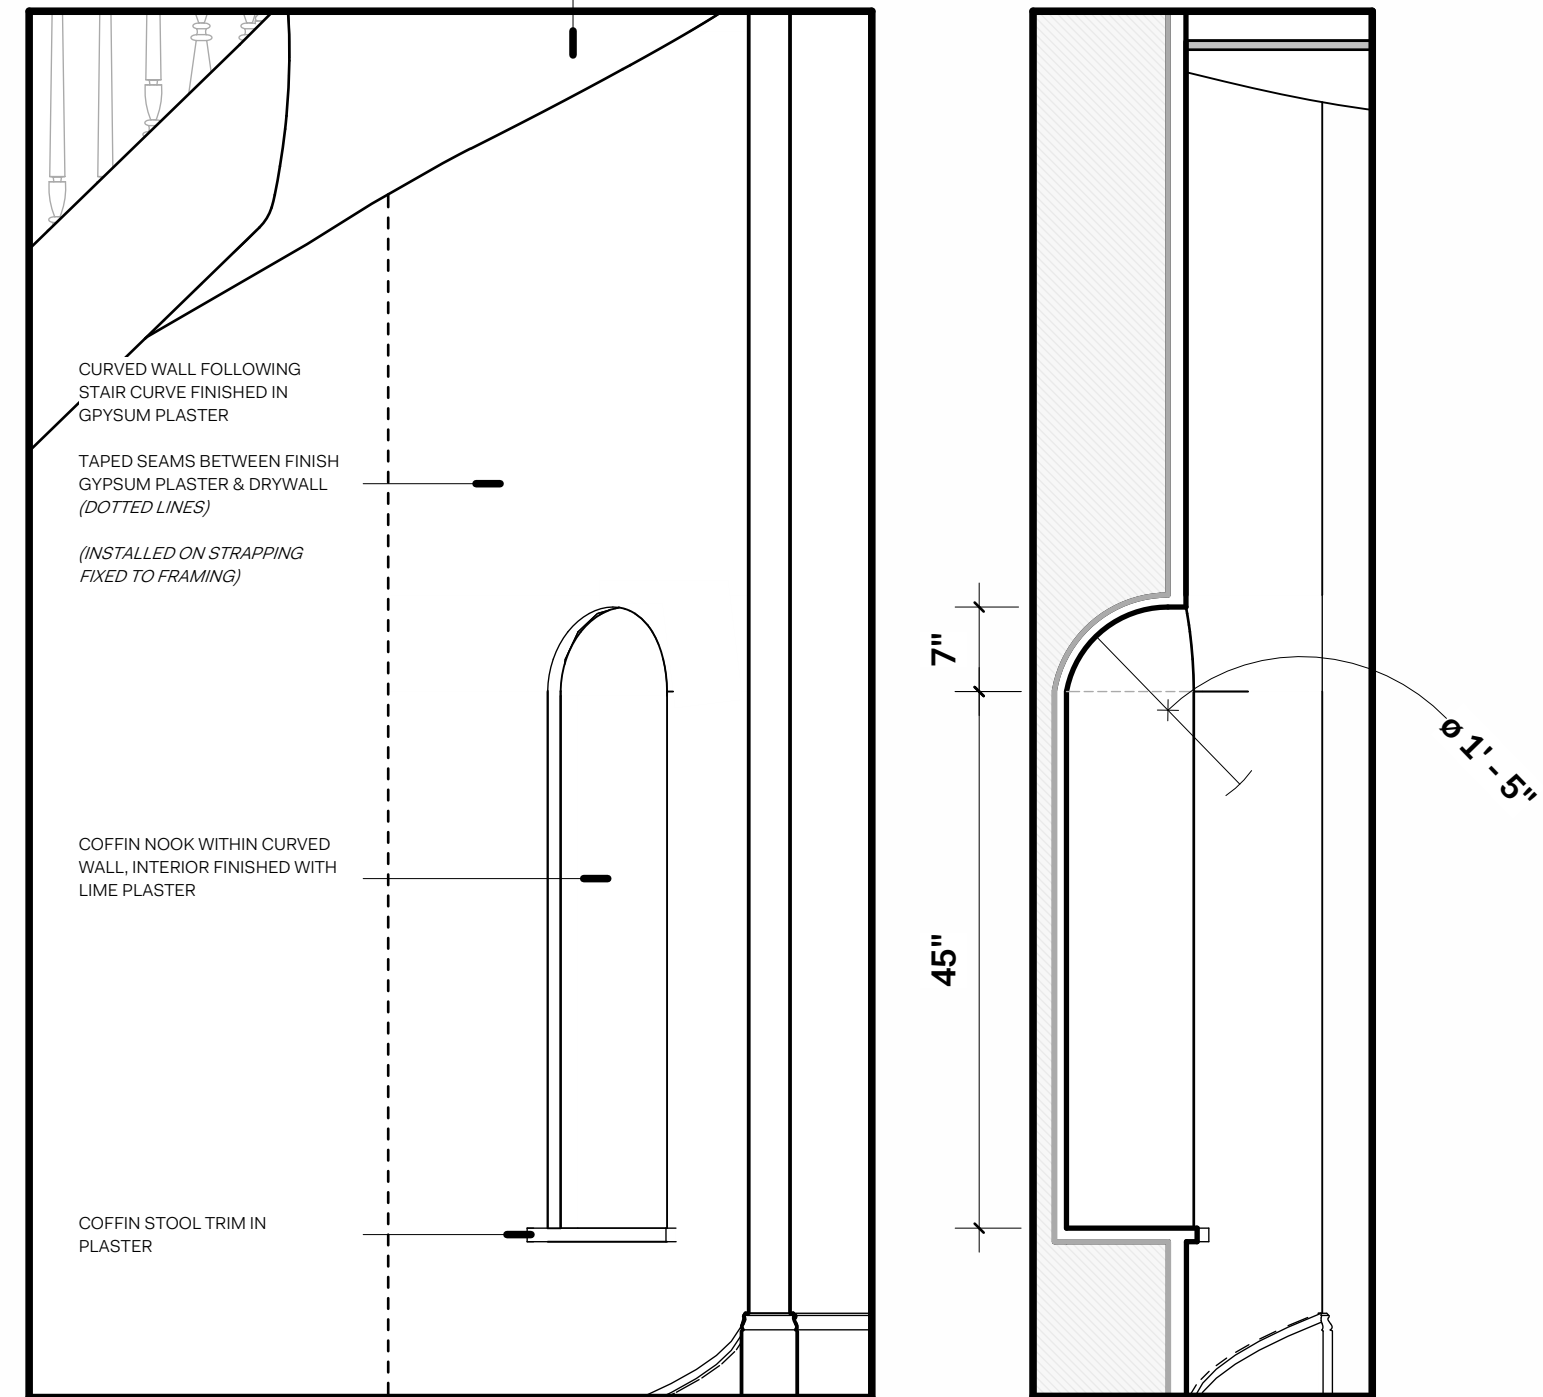

2.1 002 - UPPER STAIR LANDING SECTION 1
3/4" = 1'-0"

2.2 SECTION 2
3/4" = 1'-0"

CO Adaptive

Architect
CO Adaptive Architecture PLLC
Building 303, Suite 603
63 Flushing Avenue
Brooklyn, NY 11235
t. 347.586.0455
hello@coadaptive.co

Mechanical Electrical Plumbing Engineer
ABS Engineering, PLLC
37 West 57th Street, 8th Floor
New York, NY 10018
t. 212.217.2361
info@absengineer.com

Structural Engineer
Nathaniel Bergen, P.E.
225 W. 34th Street, #922
New York, NY 10018
t. 860.586.0025
nathaniel.bergen@gmail.com

Rev. #	Date	Revision Description
4	08/27/2024	General Update
8	03/20/2025	General Update

Owner & Project Information
Q142
142 QUINCY STREET, BROOKLYN, NY 11216
Ariel Azoff • Gabe Stein, Elizabeth Zehe • Will Cudney
DOB NOW #
B08048986

Drawing Title
**INTERIOR DETAILS - FINISH
PLASTER**
Drawing Scale: As indicated
100% @ A1 (24" x 36")

Project Number
Q142
Issue Date
03-10-2025
Sheet Number
31 / 61
Drawing Number

A-625.00

Copyright 2025 CO Adaptive Architecture PLLC All rights reserved