

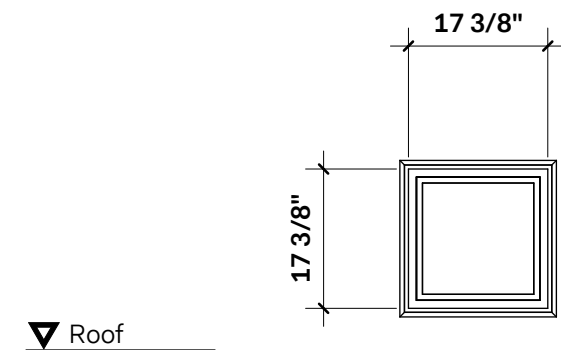
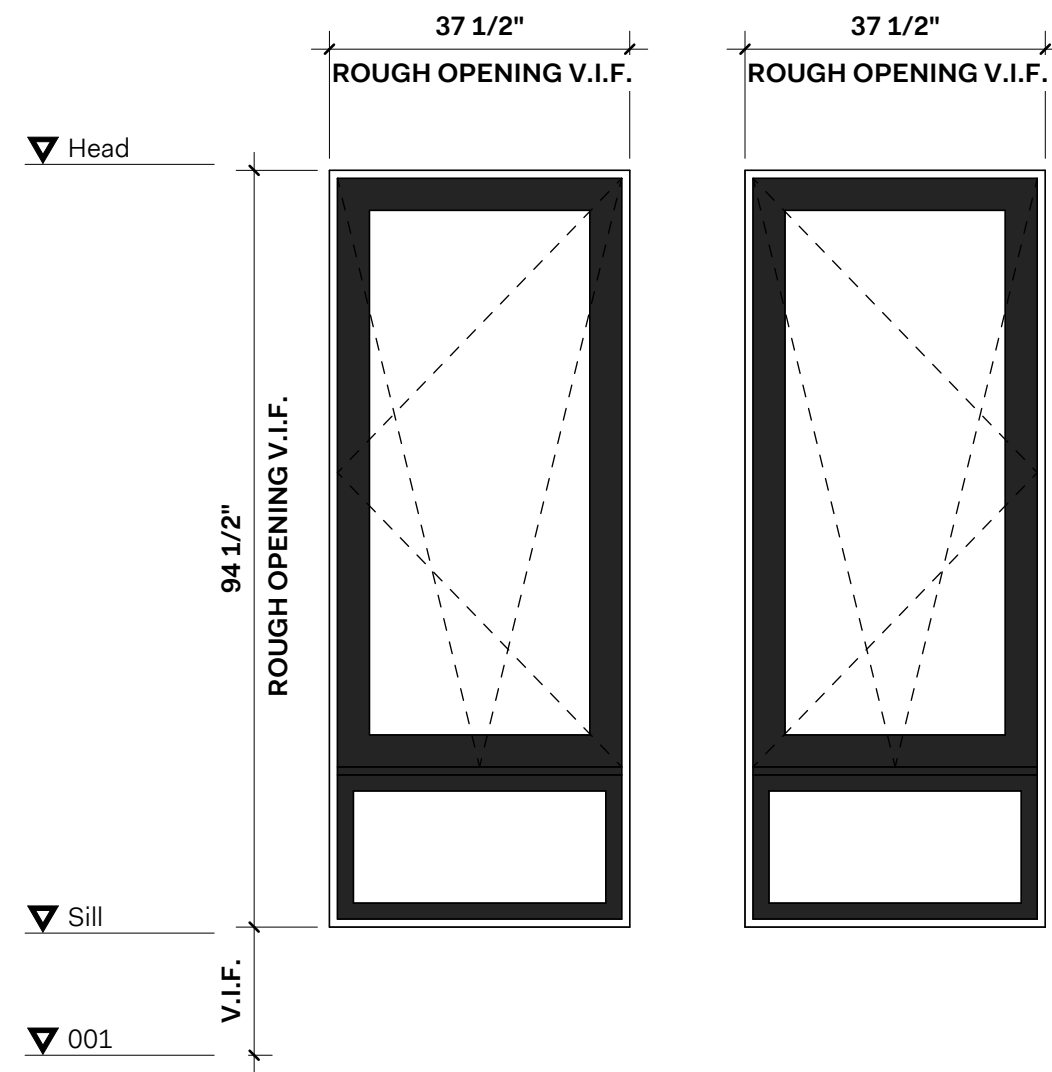
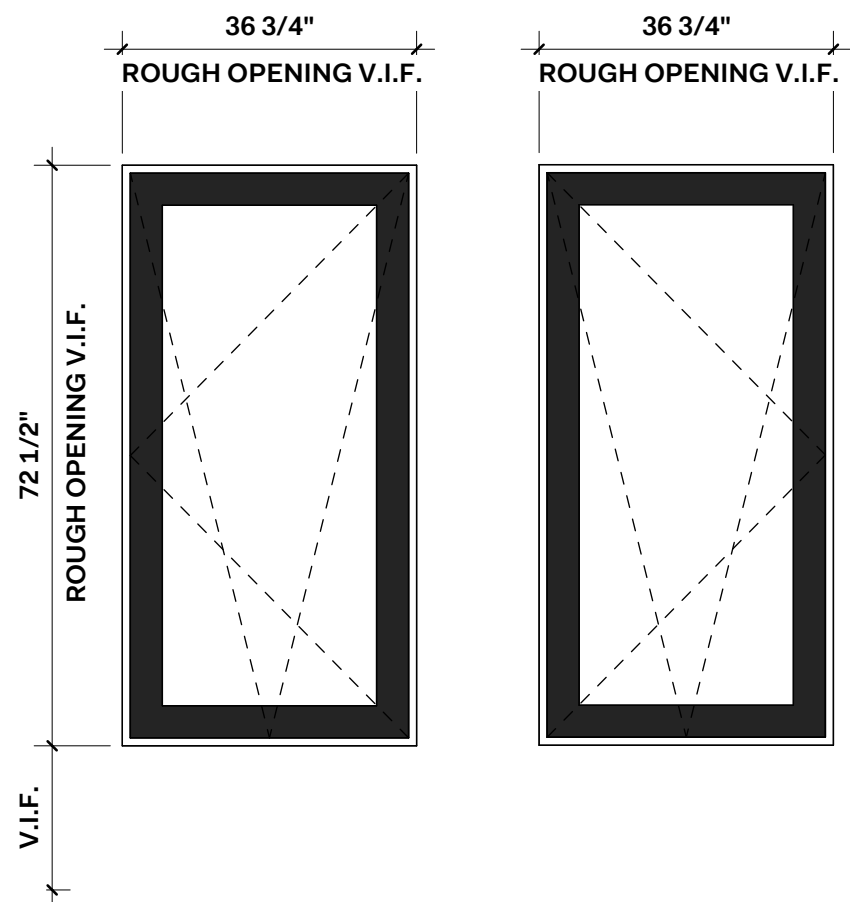
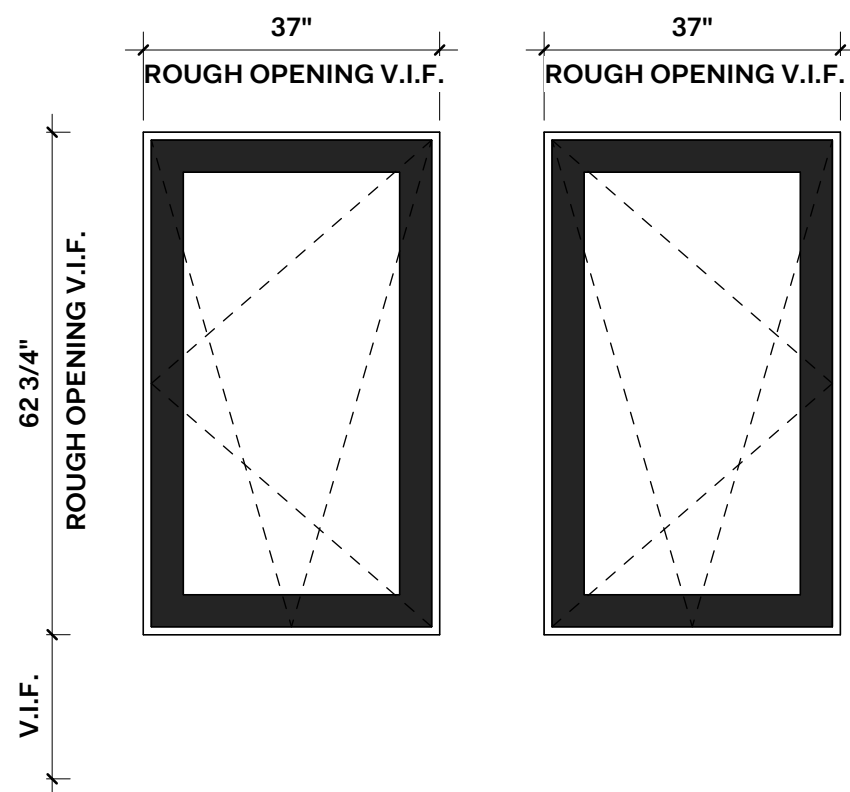
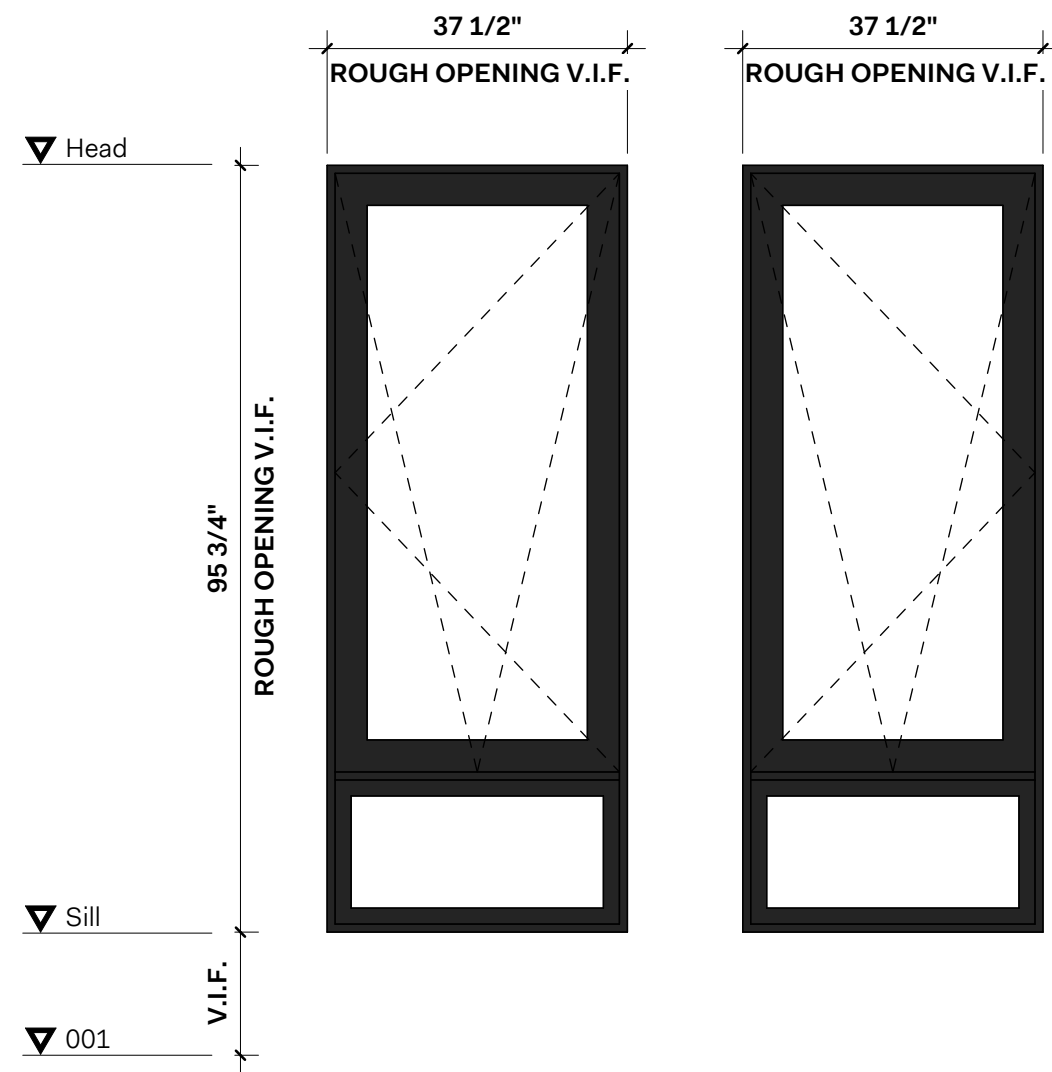
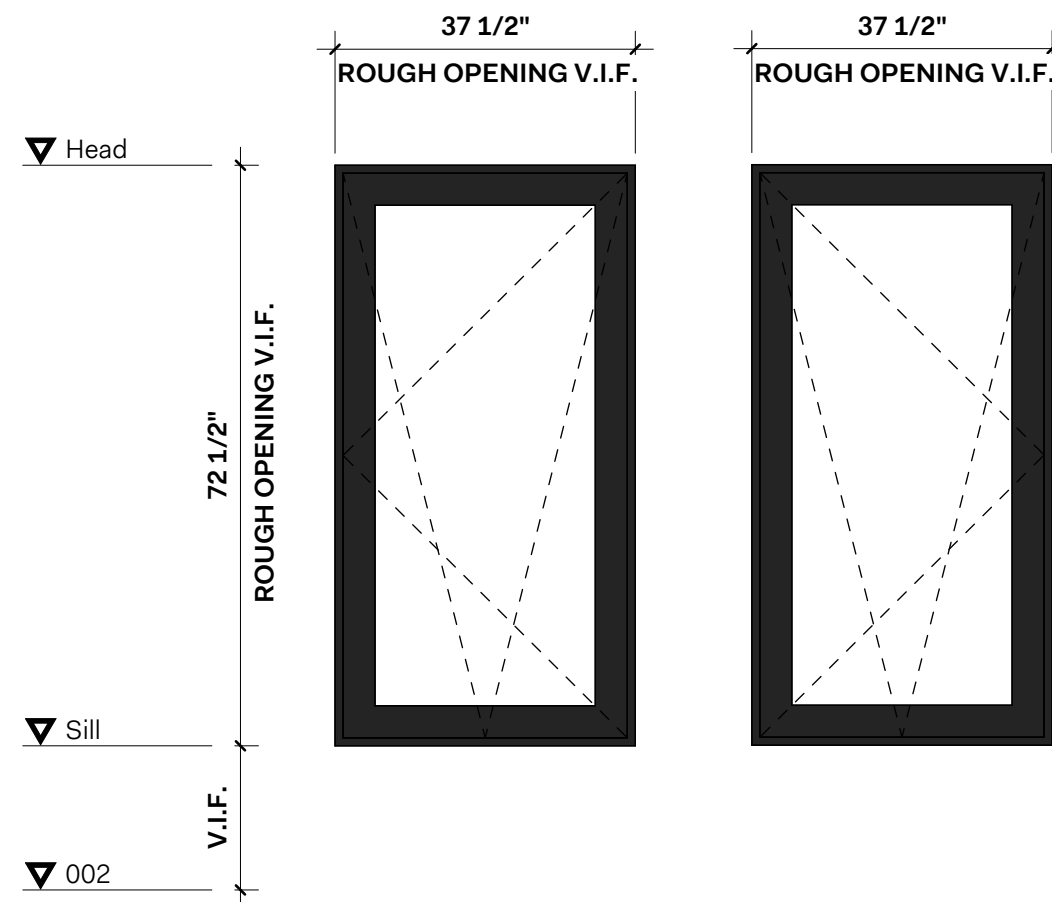


WINDOW SCHEDULE										
SEE A-520 SERIES FOR FULL SCHEDULE										
TAG	QTY	DESCRIPTION	Manufacturer	Model	WIDTH	HEIGHT	Heat Transfer Coefficient (U)	Solar Heat Gain Coefficient	Head/Sill Detail	Jamb Detail
Bas										
B1	1	TILT & TURN	Cembra		3' - 1 1/2"	4' - 9 1/2"				
B2	1	TILT & TURN	Cembra		3' - 1 1/2"	4' - 9 1/2"				
C1	1	TILT & TURN	Cembra		3' - 1"	4' - 10"				
C2	1	TILT & TURN	Cembra		3' - 1"	4' - 10"				
	4				12' - 5"	19' - 3"				
001										
H1	2	TILT & TURN WITH FIXED BOTTOM	Cembra		6' - 3"	15' - 10 1/4"				
H2	1	TILT & TURN WITH FIXED BOTTOM	Cembra		3' - 1 1/2"	7' - 10 1/2"				
H3	1	TILT & TURN WITH FIXED BOTTOM	Cembra		3' - 1 1/2"	7' - 11 3/4"				
U2	1	ARCHED FIXED	Cembra		4' - 3"	9' - 5 1/2"	0.9795	0.86		
	5				16' - 9"	41' - 2"				
002										
E1	3	TILT & TURN	Cembra		9' - 3"	18' - 1 1/2"				
E2	2	TILT & TURN	Cembra		6' - 2 1/4"	12' - 1"				
	5				15' - 5 1/4"	30' - 2 1/2"				
003										
F1	3	TILT & TURN	Cembra		9' - 3"	15' - 4 1/4"				
F2	3	TILT & TURN	Cembra		9' - 3"	15' - 0 1/4"				
	6				18' - 6"	30' - 4 1/2"				
ROOF										
K6	1	SKYLIGHT FIXED			1' - 5 3/8"	1' - 5 3/8"	0.6496	0.78		
	1				1' - 5 3/8"	1' - 5 3/8"				
	21				64' - 6 5/8"	122' - 5 3/8"				

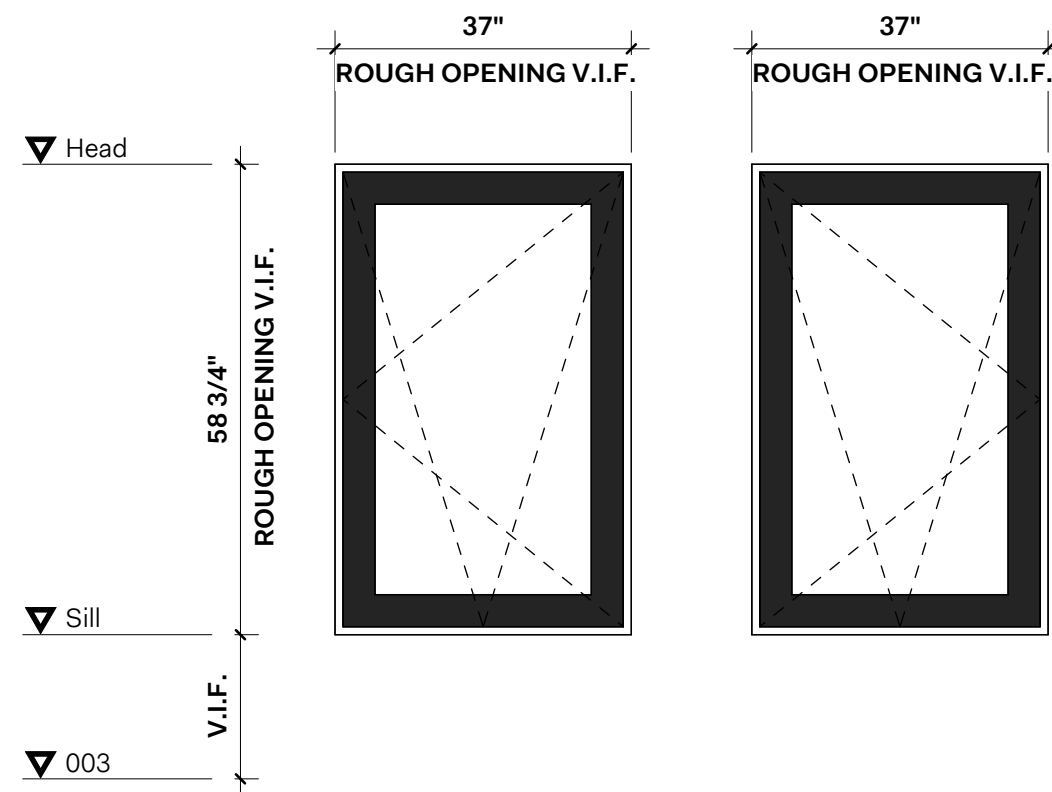

TYPE K6

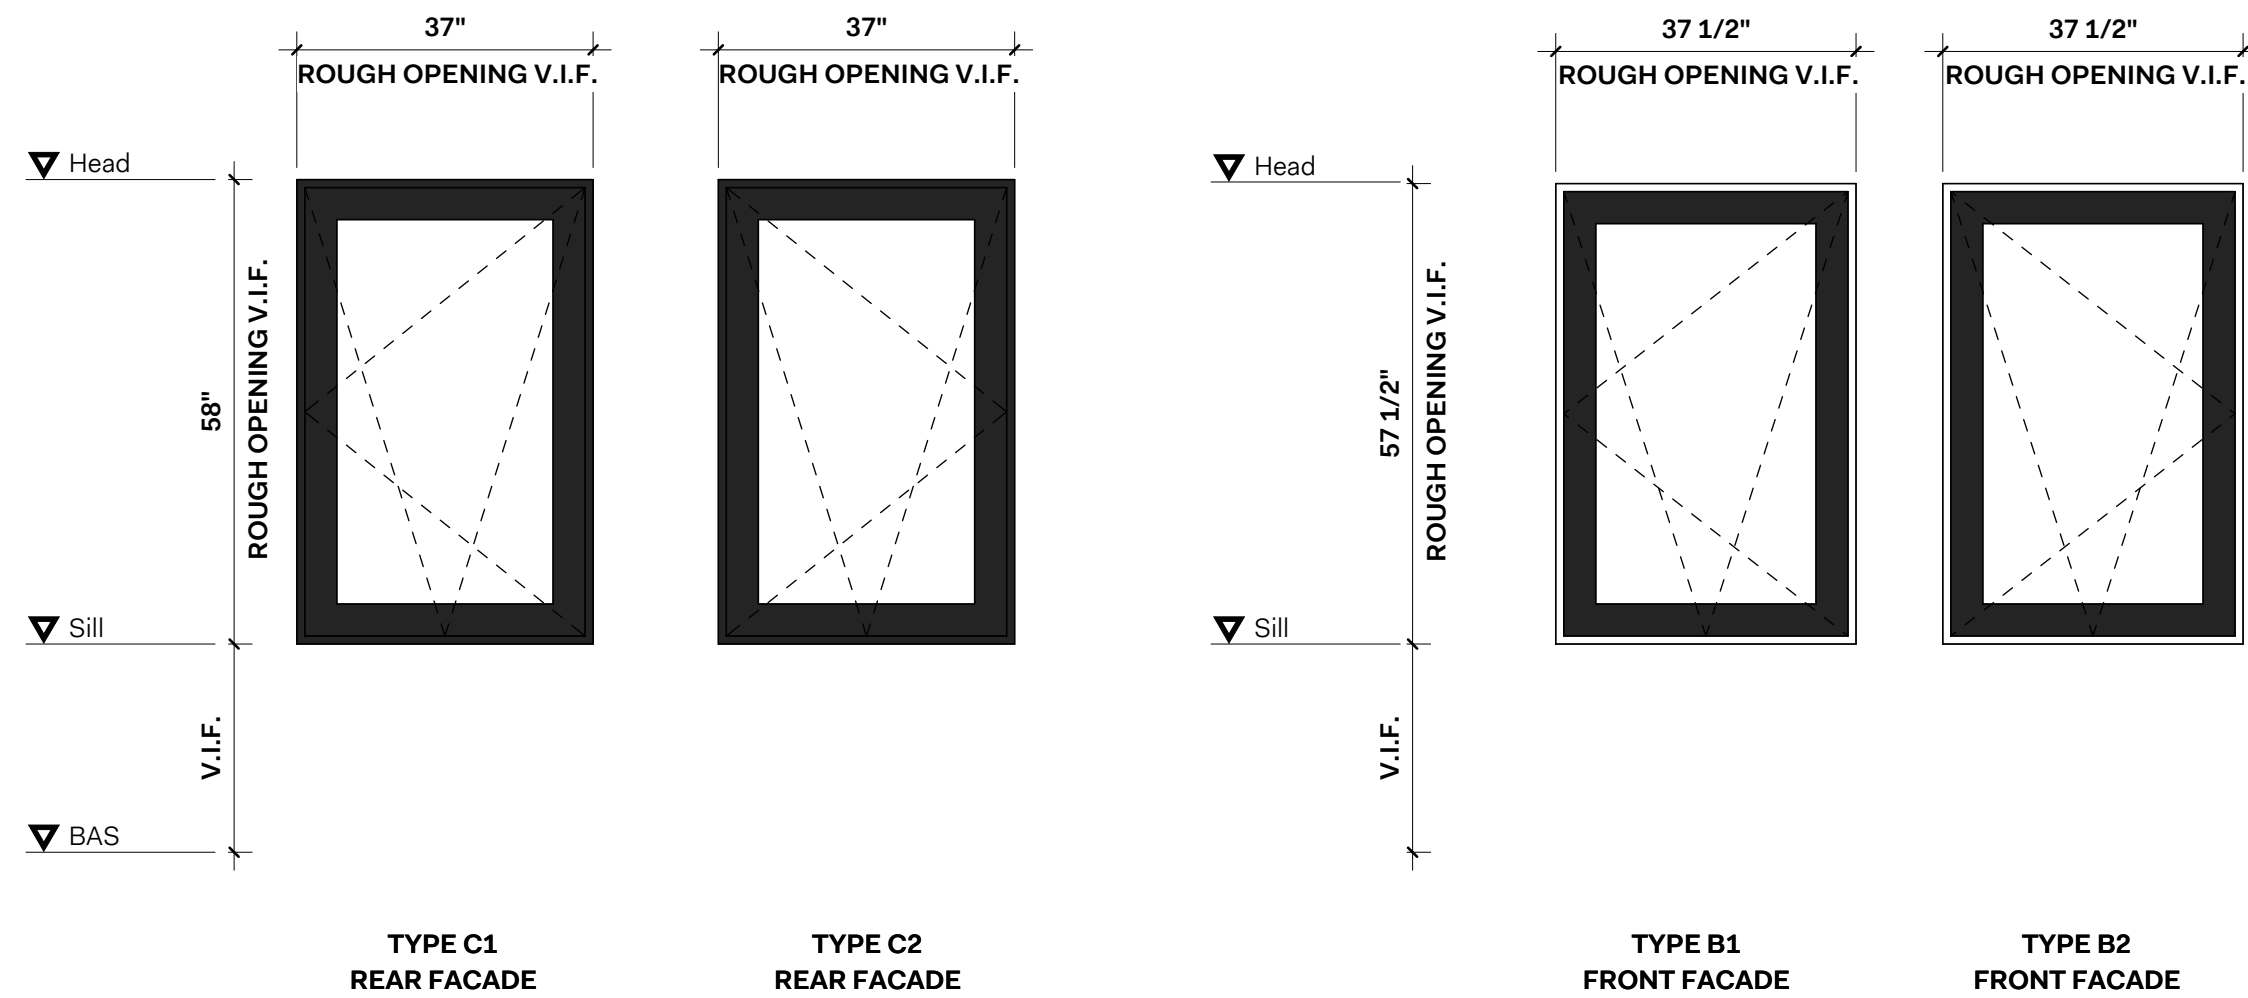

CO Adaptive

Architect
CO Adaptive Architecture PLLC
Building 303, Suite 603
63 Flushing Avenue
Brooklyn, NY 11238
t. 347.686.0465
hello@coadaptive.co

Mechanical/Electrical/Plumbing Engineer
ABS Engineering, PLLC
37 West 57th Street, 8th Floor
New York, NY 10018
t. 212.317.2361
info@absengineer.com

Structural Engineer
Nathaniel Bergan, P.E.
225 W. 34th Street, #922
New York, NY 10012
t. 860.598.0025
nathaniel.bergan@gmail.com

Rev. #	Date	Revision Description
4	08/27/2024	General Update

Owner & Project Information

Q142
142 QUINCY STREET, BROOKLYN, NY 11216

Ariel Azoff • Gabi Stein, Elizabeth Zehn • Will Cudney

DOB NOW #

80804896

Drawing Title
**EXTERIOR DETAILS -
WINDOWS - SCHEDULES**

Drawing Scale: 1/2" = 1'-0"
100% @ A1 (24" x 36")

Project Number

Q142

Issue Date

11-25-2024

Sheet Number

42 / 61

Drawing Number

A-522.00