

18
Exterior Deck
New
140 SF

17
Dining Room
New
95 SF

11
Powder Room
New
15 SF

10
Hallway
New
65 SF

12
Study
New
62 SF

14
Seating Area
New
59 SF

13
Living Room
New
169 SF

25
Primary Bedroom
New
172 SF

20
Laundry
New
12 SF

19
Hallway
New
76 SF



24
Bedroom 2
New
102 SF

21
Primary Bathroom
New
56 SF

22
Secondary Bathroom
New
43 SF

23
Bedroom 1
New
90 SF

1
003 RCP & Lighting Plan
1/4" = 1'-0"

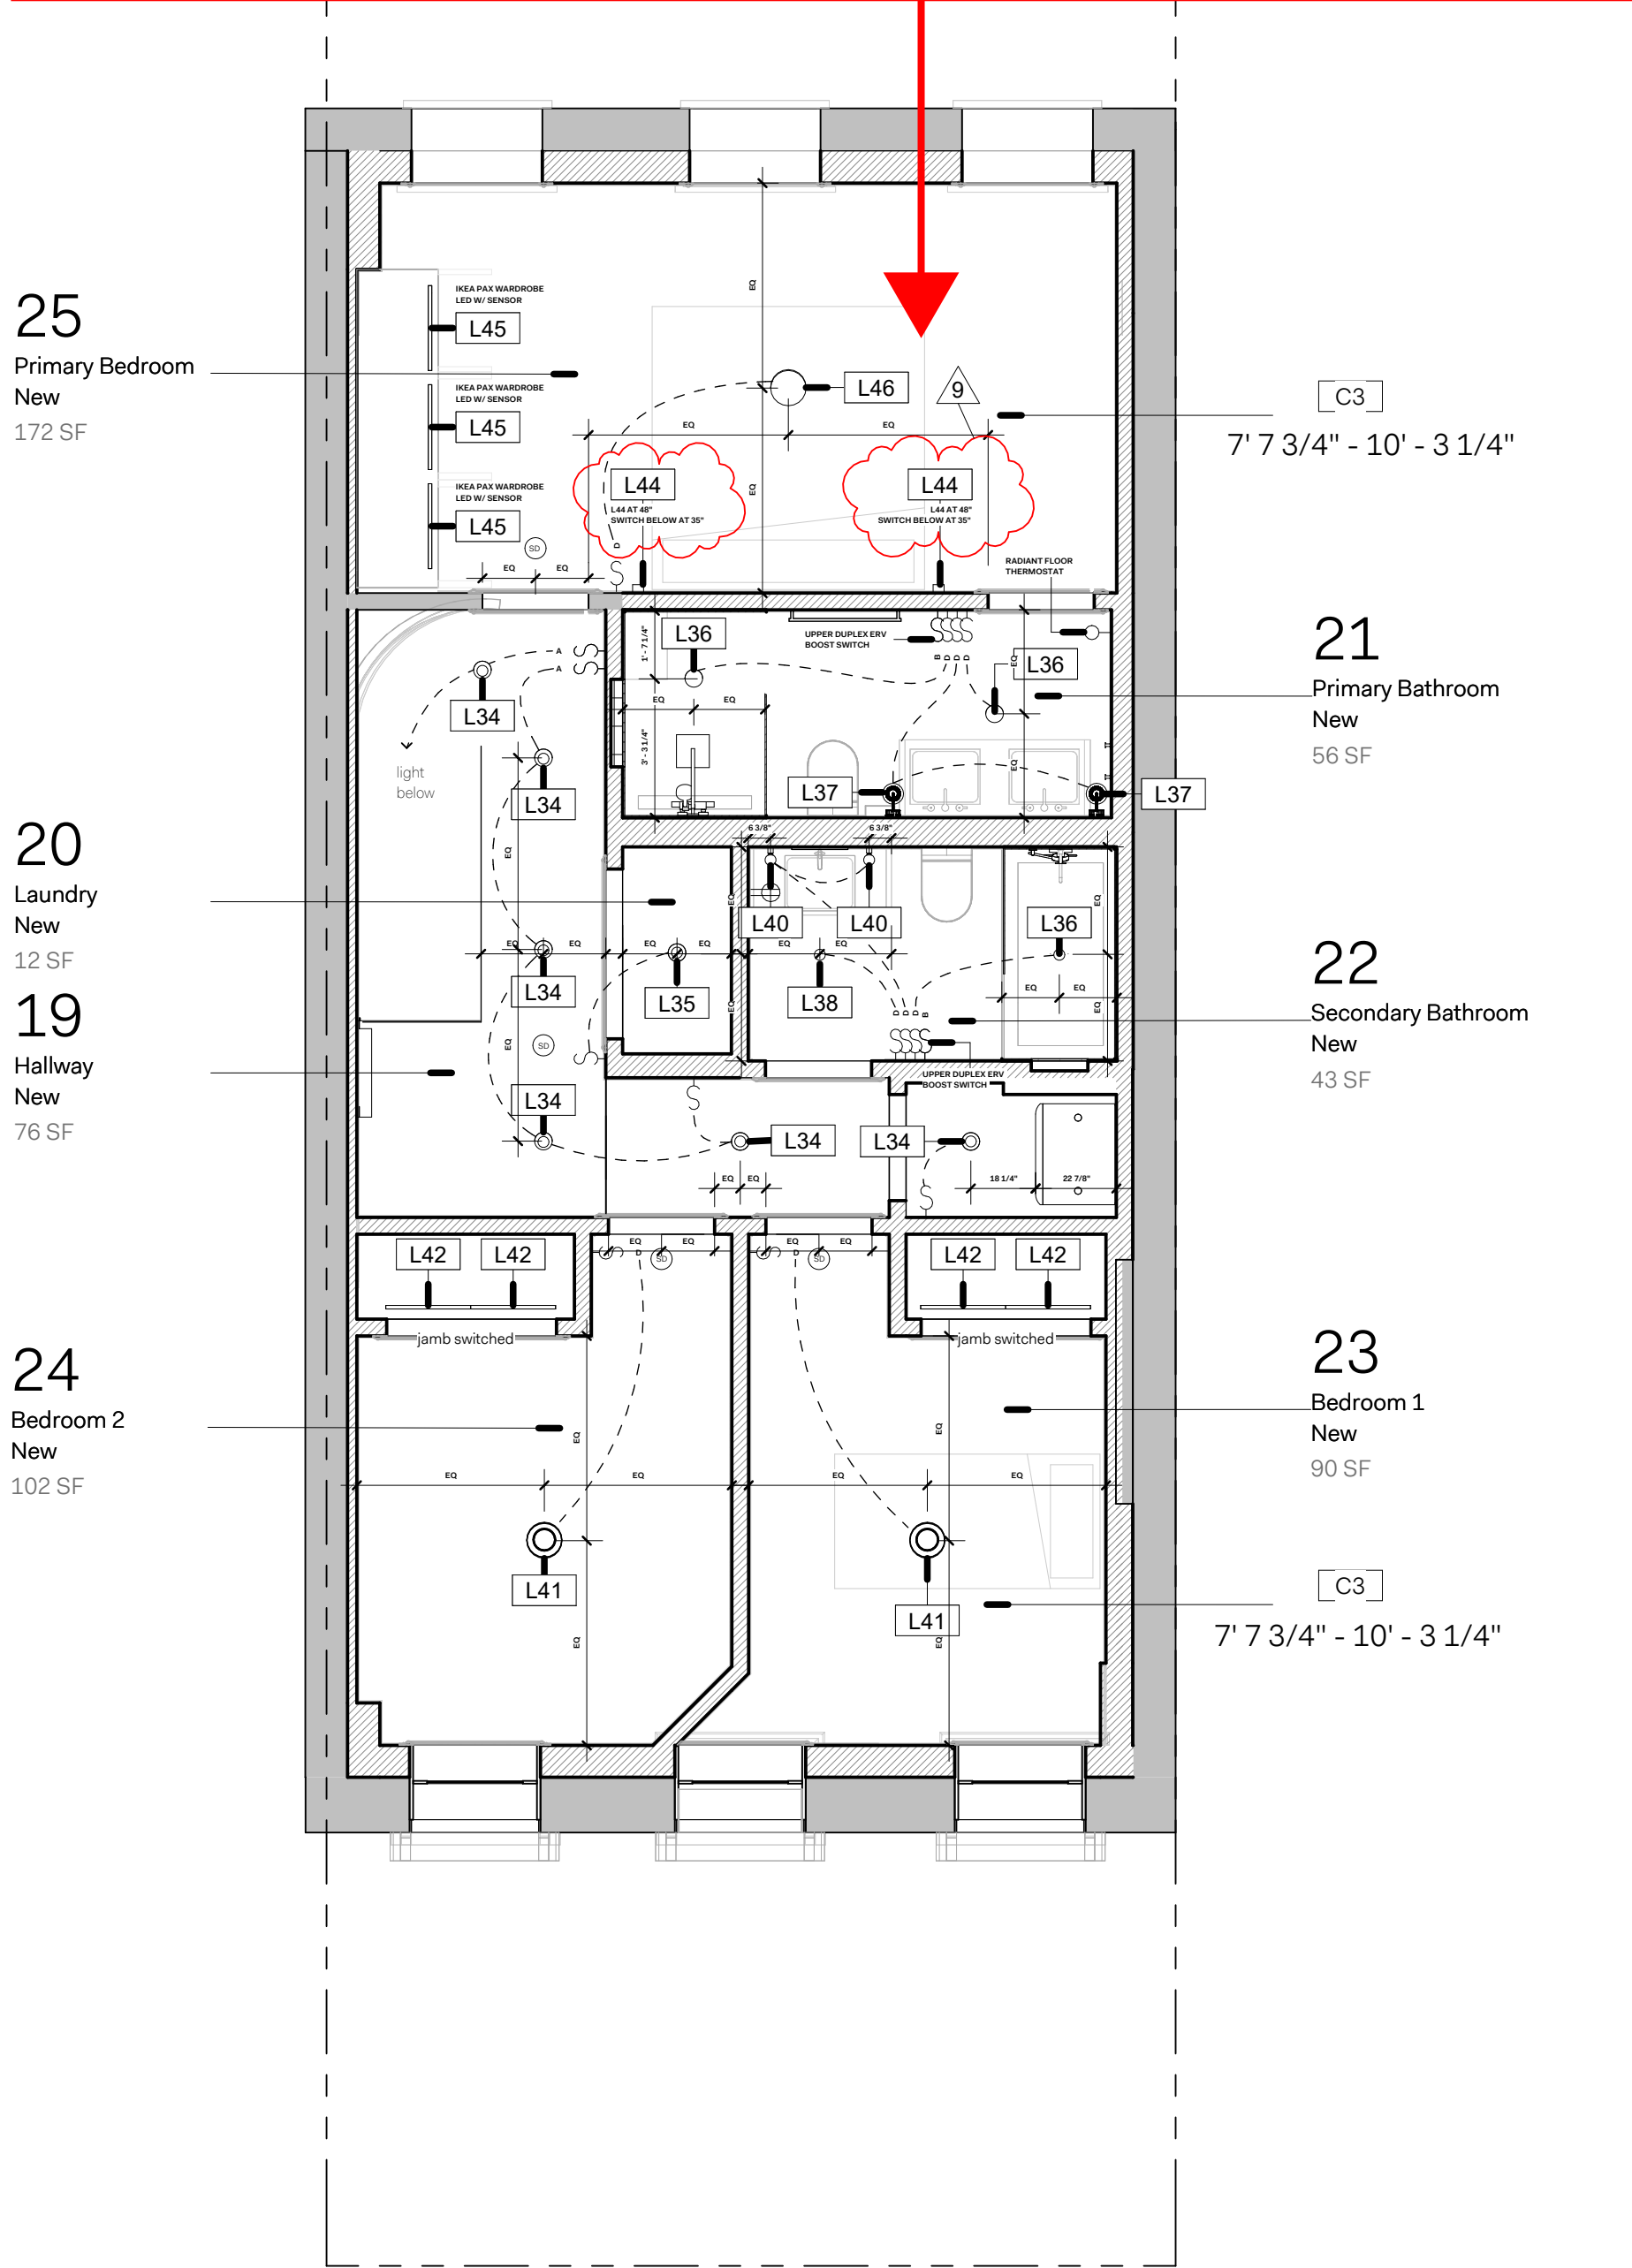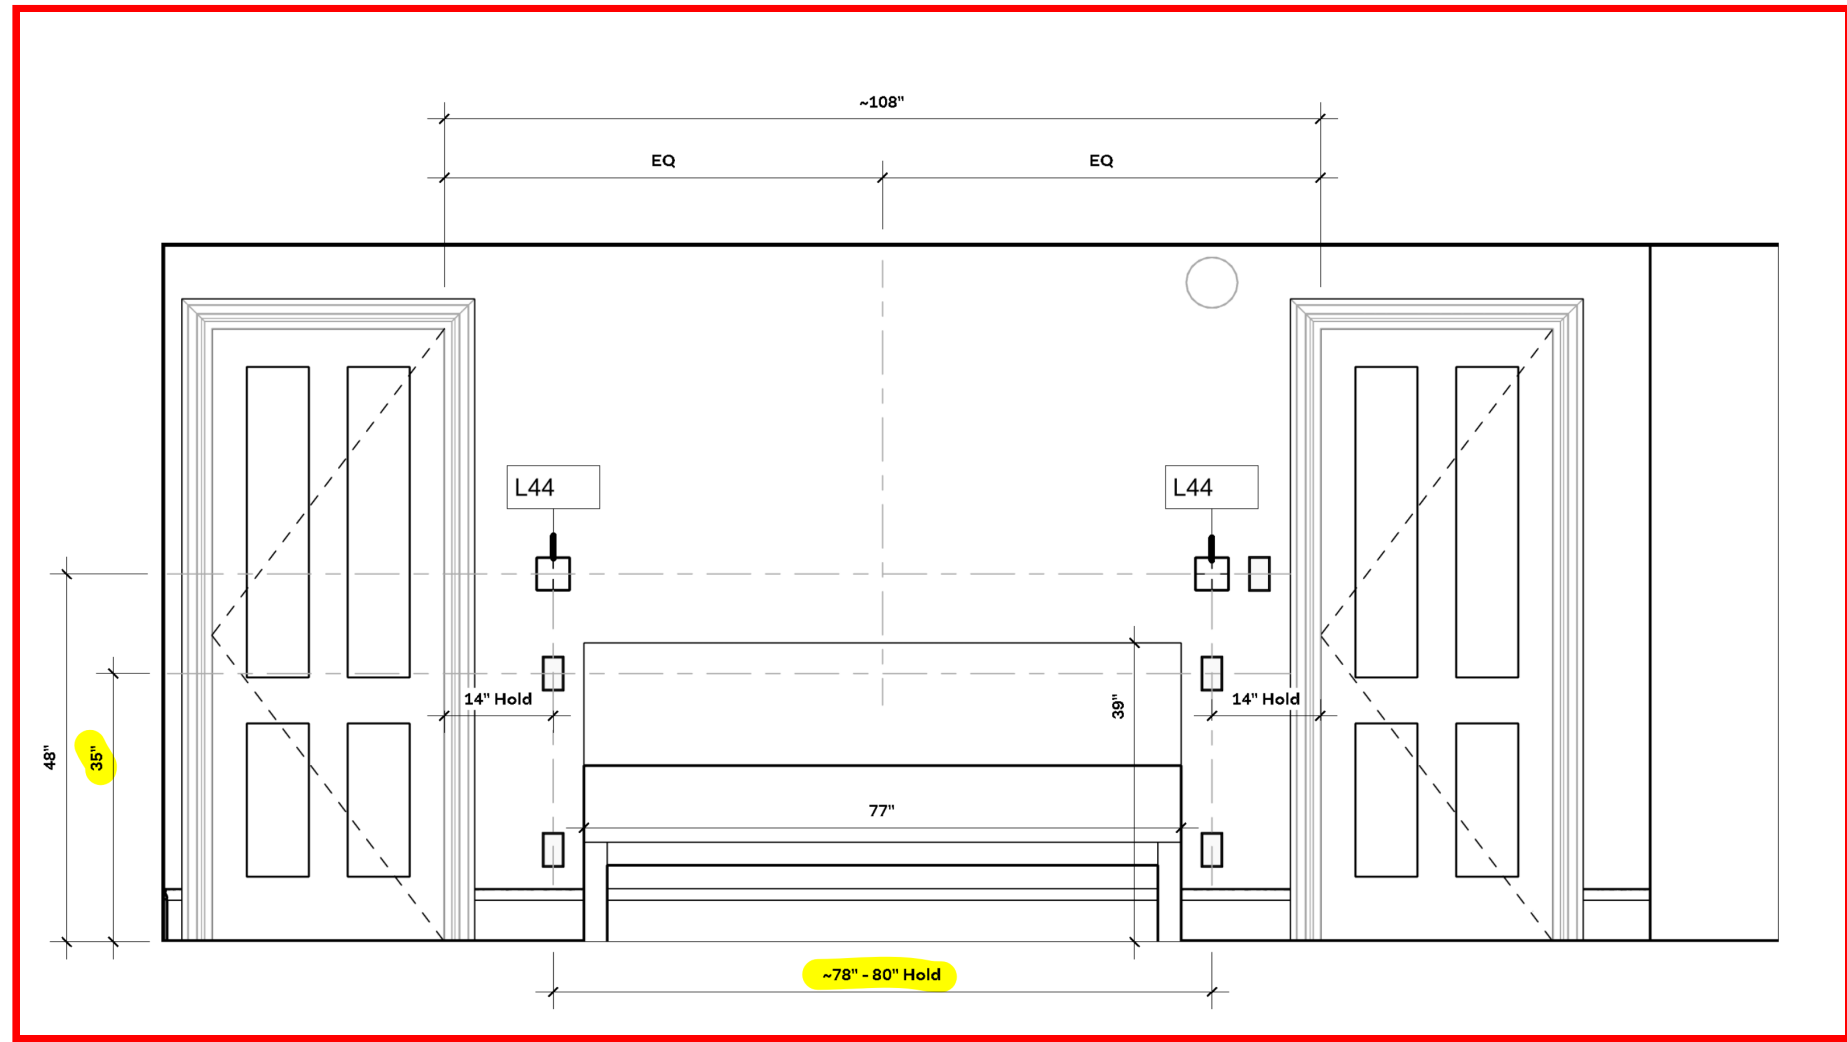

KEYNOTES_CONSTRUCTION	
1	NEW EXTERIOR-MOUNTED SOLAR SHADING DEVICE. REFER TO A-600 SERIES FOR MORE INFORMATION.
2	NEW MECHANICAL/VENTILATION EQUIPMENT. SEE RELATED MECHANICAL APPLICATION #B08050685 FOR ADDITIONAL INFORMATION.
3	NEW HIGH-PERFORMANCE WINDOWS WITHIN EXISTING OR NEW OPENING. SEE A-200 SERIES FOR ADDITIONAL INFORMATION. REFER TO EN-100 SHEET FOR ENERGY CODE COMPLIANCE.
4	NEW HIGH-PERFORMANCE EXTERIOR DOOR WITHIN EXISTING OR ENLARGED OPENINGS. SEE A-200 SERIES FOR ADDITIONAL INFORMATION. REFER TO EN-100 SHEET FOR ENERGY CODE COMPLIANCE.
5	NEW HIGH-PERFORMANCE SKYLIGHT/ROOF HATCH WITHIN EXISTING OPENING. REFER TO EN-100 SHEET FOR ENERGY CODE COMPLIANCE.
6	NEW EXTERIOR SHADING DEVICE
7	NEW DOOR AND TRIM IN NEW OPENING. SEE A-620 SERIES FOR ADDITIONAL INFORMATION.
8	SAVE AND PROTECT EXISTING FIREPLACE THROUGHOUT CONSTRUCTION.
9	NEW REFRIGERATOR, INDUCTION COOKTOP, WALL OVEN AND CABINETRY AS INDICATED. NEW DISHWASHER, SINK, AND FACUET ON NEW ROUGH INS. NEW BACKSPLASH AND COUNTERTOP. SEE A-400 SERIES FOR EXTENTS AND A-700 SERIES FOR SCHEDULES.
11	NEW STRUCTURAL WOODEN DECK. PRIMARY WOOD FRAME WITH STEEL / CABLE RAILINGS. SEE A-500 SERIES AND RELATED STRUCTURAL APPLICATION #... FOR ADDITIONAL INFORMATION.
12	NEW CEILING AS INDICATED THROUGHOUT ENTIRE FLOOR, UON. SEE A-110 SERIES AND A-600 SERIES FOR ADDITIONAL INFORMATION.
13	NEW WOOD FLOOR THROUGHOUT ENTIRE FLOOR. RED OAK TO MATCH EXISTING
14	NEW PAINT THROUGHOUT ENTIRE FLOOR, UON. SEE A-150 SERIES AND A-700 SERIES FOR ADDITIONAL INFORMATION.
15	NEW WOOD FLOOR FEATHERED IN AROUND EXISTING WOOD FLOOR. RED OAK TO MATCH EXISTING
16	NEW TOILET, SHOWER/BATHTUB, LAVATORY, AND VANITY ON NEW ROUGH INS. NEW WALL AND FLOOR TILES THROUGHOUT BATHROOM. SEE A-400 SERIES FOR EXTENTS AND A-700 SERIES FOR SCHEDULES.
17	NEW TOILET AND VANITY ON NEW ROUGH INS. NEW WALL AND FLOOR TILES THROUGHOUT BATHROOM. SEE A-400 SERIES FOR EXTENTS AND A-700 SERIES FOR SCHEDULES.
18	NEW PLUMBING RISER IN EXISTING BEARING WALL. FURR OUT WITH NEW FRAMING TO ENCAPSULATE NEW RISER AND ALL ASSOCIATED PIPING.
19	REINSTALL EXISTING MANTLE.
20	NEW CEILING WITH PASSIVE HOUSE MEMBRANE AND LIGHTING.
21	WALLS & FLOORS TO BE PATCHED.
22	NEW WASHER/DRYER.
23	NEW ETHERNET POINT
25	NEW RADIANT FLOOR HEATING SYSTEM.
26	REINSTALL EXISTING DOOR. SEE SHEET A-621 FOR MORE DETAILS.
27	EXISTING THREE FIXTURE BATHROOM, CONVERTED TO TWO FIXTURE POWDER ROOM. NEW WALL AND FLOOR TILE AT REMOVED SHOWER.
28	NEW HEAT PUMP WATER HEATER.
29	NEW EJECTOR PUMP IN EXISTING PIT LOCATION.
30	NEW CLOSET IN EXISTING BATHROOM. EXISTING THREE FIXTURE BATHROOM IN CELLAR TO BE MODIFIED TO TWO FIXTURE POWDER ROOM AS PER BB 2011-010. CLOSET PARTITION TO ENSURE MAXIMUM 5'-0" BATHROOM DEPTH.
31	NEW CONCRETE TO BE POURED IN HATCHED AREAS
32	INSTALL REINFORCED MASONRY INFILL AND FLOOR FRAMING INFILL PER STRUCTURAL DETAILS
33	NEW PLUMBING WALL, CEMENT BOARD, WATERPROOFING & TILE ABOVE DEMOLISHED DECORATIVE TILE DATUM LINE

ASBESTOS DISTURBANCE:
ANY DISTURBANCE OF ASBESTOS MATERIAL WILL REQUIRE ASBESTOS ABATEMENT AND FILINGS WITH NYCDEP. ASBESTOS ABATEMENT WILL REQUIRE A LICENSED ASBESTOS CONTRACTOR WITH CERTIFIED ASBESTOS WORKERS. THE UNIT OWNER IS ALSO RESPONSIBLE FOR ENGAGING THE SERVICES OF A THIRD PARTY INDEPENDANT ASBESTOS CONSULTANT TO PERFORM ASBESTOS PROJECT MONITORING AND CONTRACTOR OVERSIGHT DURING THE ABATEMENT PROCESS.

HARDWIRED COMBINED SMOKE AND CARBON MONOXIDE DETECTORS:
SHALL COMPLY WITH LL 62/81, RS 17-13 AND INSTALLED IN ACCORDANCE WITH RS 17-14, BC 907.2.11.1 AND BC 908.7.1.1.1

PER BC 901.9.5.1, WHERE ALTERATION WORK DOES NOT RESULT IN THE REMOVAL OF EXISTING AND/OR INSTALLATION OF NEW INTERIOR WALL OR CEILING FINISHES PERMITTING THE INSTALLATION OF CONCEALED WIRING FOR ALL THE REQUIRED ALARMS THROUGHOUT THE DWELLING UNIT, BATTERY OPERATED SMOKE DETECTORS SHALL BE PROVIDED.

DETECTORS SHALL BE PROVIDED IN EVERY DWELLING UNIT WITHIN FIFTEEN FEET OF THE PRIMARY ENTRANCE OF EACH BEDROOM, WITHIN EACH ROOM USED FOR SLEEPING PURPOSES AND AT EACH FLOOR. REFER TO PLAN FOR LOCATIONS.

LIGHTING FIXTURE SCHEDULE - ABBREVIATED						
TAG	QTY	DESCRIPTION	MANUFACTURER	MODEL #	COLOR TEMPERATURE	DIM MIN G
L1	15	Recessed Ultra-Thin Slim Round Baffle Trim	Goodlite	G-97824	2700K	Yes
L2	1	Wall Sconce	Access	ACC485672	2700K	No
L3A	3	Exterior Wall Sconce	Kichler	9654BK	by bulb	No
L3B	6	Exterior Wall Sconce	Bellevue	PWS1148BK	by bulb	No
L4	1	Basement Entry Vestibule Flush Mount	Pottery Barn	8265954	by bulb	No
L5A	1	Ceiling Flush Mount	Olde Brick Lighting	FM-Rutland-12	by bulb	Yes
L5B	3	Ceiling Flush Mount	Olde Brick Lighting	FM-4MinCI-8	by bulb	Yes
L6	5	Wall Sconce	Pottery Barn	545225	by bulb	Yes
L7	2	Ceiling Flush Mount	Olde Brick Lighting	FM-Linden-8	by bulb	Yes
L8	1	Vanity Sconce	Kichler	KHR579108	3000K	Yes
L10	2	Wall Sconce w/ Switch	Olde Brick Lighting	SSA2-Chaika-4	by bulb	No
L11	4	Door Switched Light Strip	Ikea	PAX LED	2700K	No
L12	1	Ceiling Flush Mount	Olde Brick Lighting	SMB-Belmt-14	by bulb	Yes
L13	1	Ceiling Flush Mount	Olde Brick Lighting	HG-Ellicot-12	by bulb	Yes
L14	1	Pendant	Color Cord	LF-001-100	by bulb	Yes
L15	1	Ceiling Flush Mount	Ikea	204.980.13	2700K	No
L17	1	Pendant	Olde Brick Lighting	CPD-Ryttenberg-8	by bulb	No
L18	8	3" Round Adjustable Downlight	USAI Lighting	BeveLED Mini Basic Pancake	Dim to Warm	Yes
L19A	6	Under Cabinet LED	Ikea	004.554.20	2700K	No
L20	1	Dining Area Pendant	Vakkerlight	VKK-DZ051908 3306	by bulb	Yes
L21	2	Island Pendant	Olde Brick Lighting	PD-Thaddeus-9	by bulb	Yes
L22	1	Ceiling Flush Mount	Olde Brick Lighting	ST-Ryttenberg-8	by bulb	No
L23	1	Pendant	Crystorama	ADD-306-AG-A-M	by bulb	Yes
L24	4	Flush Mount Small	Elegant Lighting	LD6054BR	by bulb	No
L25	1	Vanity Sconce	Ikea	204.316.35	by bulb	Yes
L26	1	Pendant	Progress Lighting	P500381	by bulb	Yes
L27	1	Pendant	Color Cord	LF-001-100	by bulb	Yes
L28	1	Flush Mount	Golden Lighting	0305-FM BCB-CLR	by bulb	Yes
L29	3	Flush Mount Small	Nuvo Lighting	60/4804	by bulb	Yes
L30	4	Under Cabinet LED	Ikea	004.554.20	2700K	No
L31	2	Pendant	MattAlfordStudio	Bistro Globe Pendant	by bulb	Yes
L33	1	Pendant	Color Cord	LF-001-100	by bulb	Yes
L34	6	Flush Mount Small	Nuvo Lighting	60/4804	by bulb	No
L35	1	Flush Mount Small	Ikea	204.980.13	No	
L36	3	Flush Mount Small	Maxim	57660WTWT	3000K	Yes
L37	2	Vanity Sconce	Ikea	204.316.35	by bulb	Yes
L38	1	Flush Mount Small	Golden Lighting	0305-FM BCB-CLR	by bulb	No
L40	2	Wall Sconce	Nuvo Lighting	60/4804	by bulb	Yes
L41	2	Flush Mount Large	Golden Lighting	0305-FM BCB-CLR	by bulb	Yes
L42	5	Door Switched Light Strip	Ikea	004.554.20	No	
L44	2	Wall Sconce	Astro Lighting	AST1118861	3000K	Yes
L45	3	Door Switched Light Strip	Ikea	PAX LED	2700K	No
L46	1	Flush Mount Large	Maxim	57664WTWT	3000K	Yes

Light Switch Schedule 002 & 003			
Level	Tag	Model	Qty
002	SA	Inovelli Aux Switch	7
002	SB	TBD	2
002	SD	Inovelli White Series Smart Dimmer	8
002	S	Inovelli White Series Smart Dimmer	3
003	SA	Inovelli Aux Switch	2
003	SB	TBD	2
003	SD	Inovelli White Series Smart Dimmer	11
003	S	Inovelli White Series Smart Dimmer	3

LEGEND			
SEE G-002 FOR FULL SYMBOLS LIST.			
SMOKE DETECTOR	RECESSED ELEC PANEL	CABLE TV / DATA RECEPTACLE 14" ABOVE FINISHED FLOOR UNLESS OTHERWISE NOTED	TEL DATA RECEPTACLE 14" ABOVE FINISHED FLOOR U.O.N.
LIGHT FIXTURES REFER TO SCHEDULE ON A-702	FLUSH MOUNT LIGHT	INOVELLI WHITE SERIES SMART DIMMER SET TO ON/OFF MODE	INOVELLI WHITE SERIES SMART DIMMER SET TO DIMMER MODE
PENDANT LIGHT	WALL-MOUNTED SCONCE	INOVELLI AUX SWITCH FOR MULTI-WAY CONFIGURATION	ERV BOOST SWITCH
CEILING TYPE TAG REFER TO A-602 FOR DETAILS	SMOKE AND CARBON MONOXIDE DETECTOR	PHOTOCELL FIXTURE	BUZZER W/ VIDEO
		THERMOSTAT	

DIMMING + NON-DIMMING FIXTURES TO UTILIZE THE SAME SWITCH TYPE. AN AUX ADD-ON SWITCH IS SPECIFIED IN MULTI-WAY SWITCHING CONFIGURATIONS. SEE PLANS FOR TYPES & LOCATIONS.

CO
Adaptive

Architect
CO Adaptive Architecture PLLC
Building 303, Suite 603
63 Flushing Avenue
Brooklyn, NY 11238
t. 347.686.0465
hello@coadaptive.co

Mechanical Electrical Plumbing Engineer
ABS Engineering, PLLC
37 West 57th Street, 8th Floor
New York, NY 10018
t. 212.317.2361
info@absengineer.com

Structural Engineer
Nathaniel Bergen, P.E.
225 W. 34th Street, #922
New York, NY 10012
t. 860.586.0025
nathaniel.bergen@gmail.com

Rev. # Date Revision Description
4 08/27/2024 General Update
8 03/20/2025 General Update
9 04/25/2025 Electrical Updates

Owner & Project Information

Q142

142 QUINCY STREET, BROOKLYN, NY 11216

Ariel Acoff • Gabe Stein, Elizabeth Zehn • Will Cudney

DOB NOW #

000049986

Drawing Title

RCP & LIGHTING PLAN 002 &

003

Drawing Scale 1/4" = 1'-0"

100% @ Arch D (24" x 36")

Project Number

Q142

Issue Date

04-15-2025

Sheet Number

19 / 61

Drawing Number

A-113.00

Copyright 2021 CO Adaptive Architecture PLLC All rights reserved